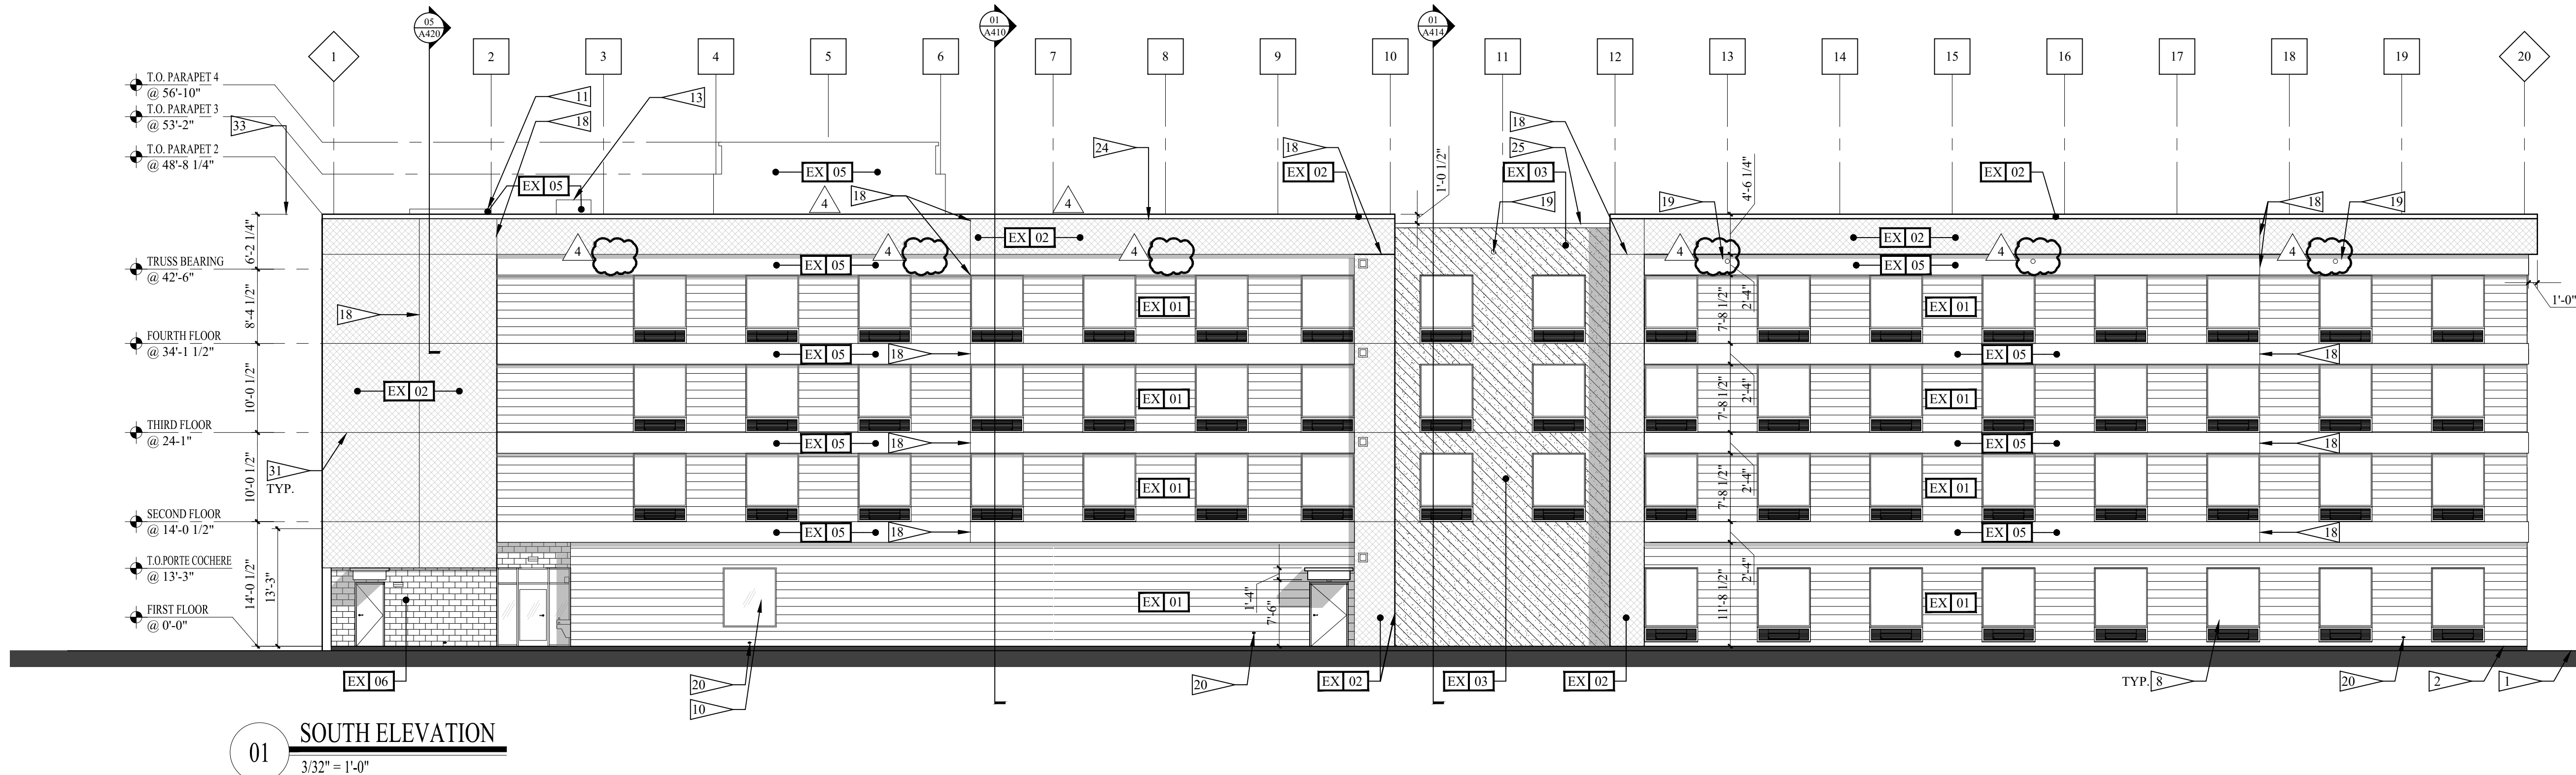
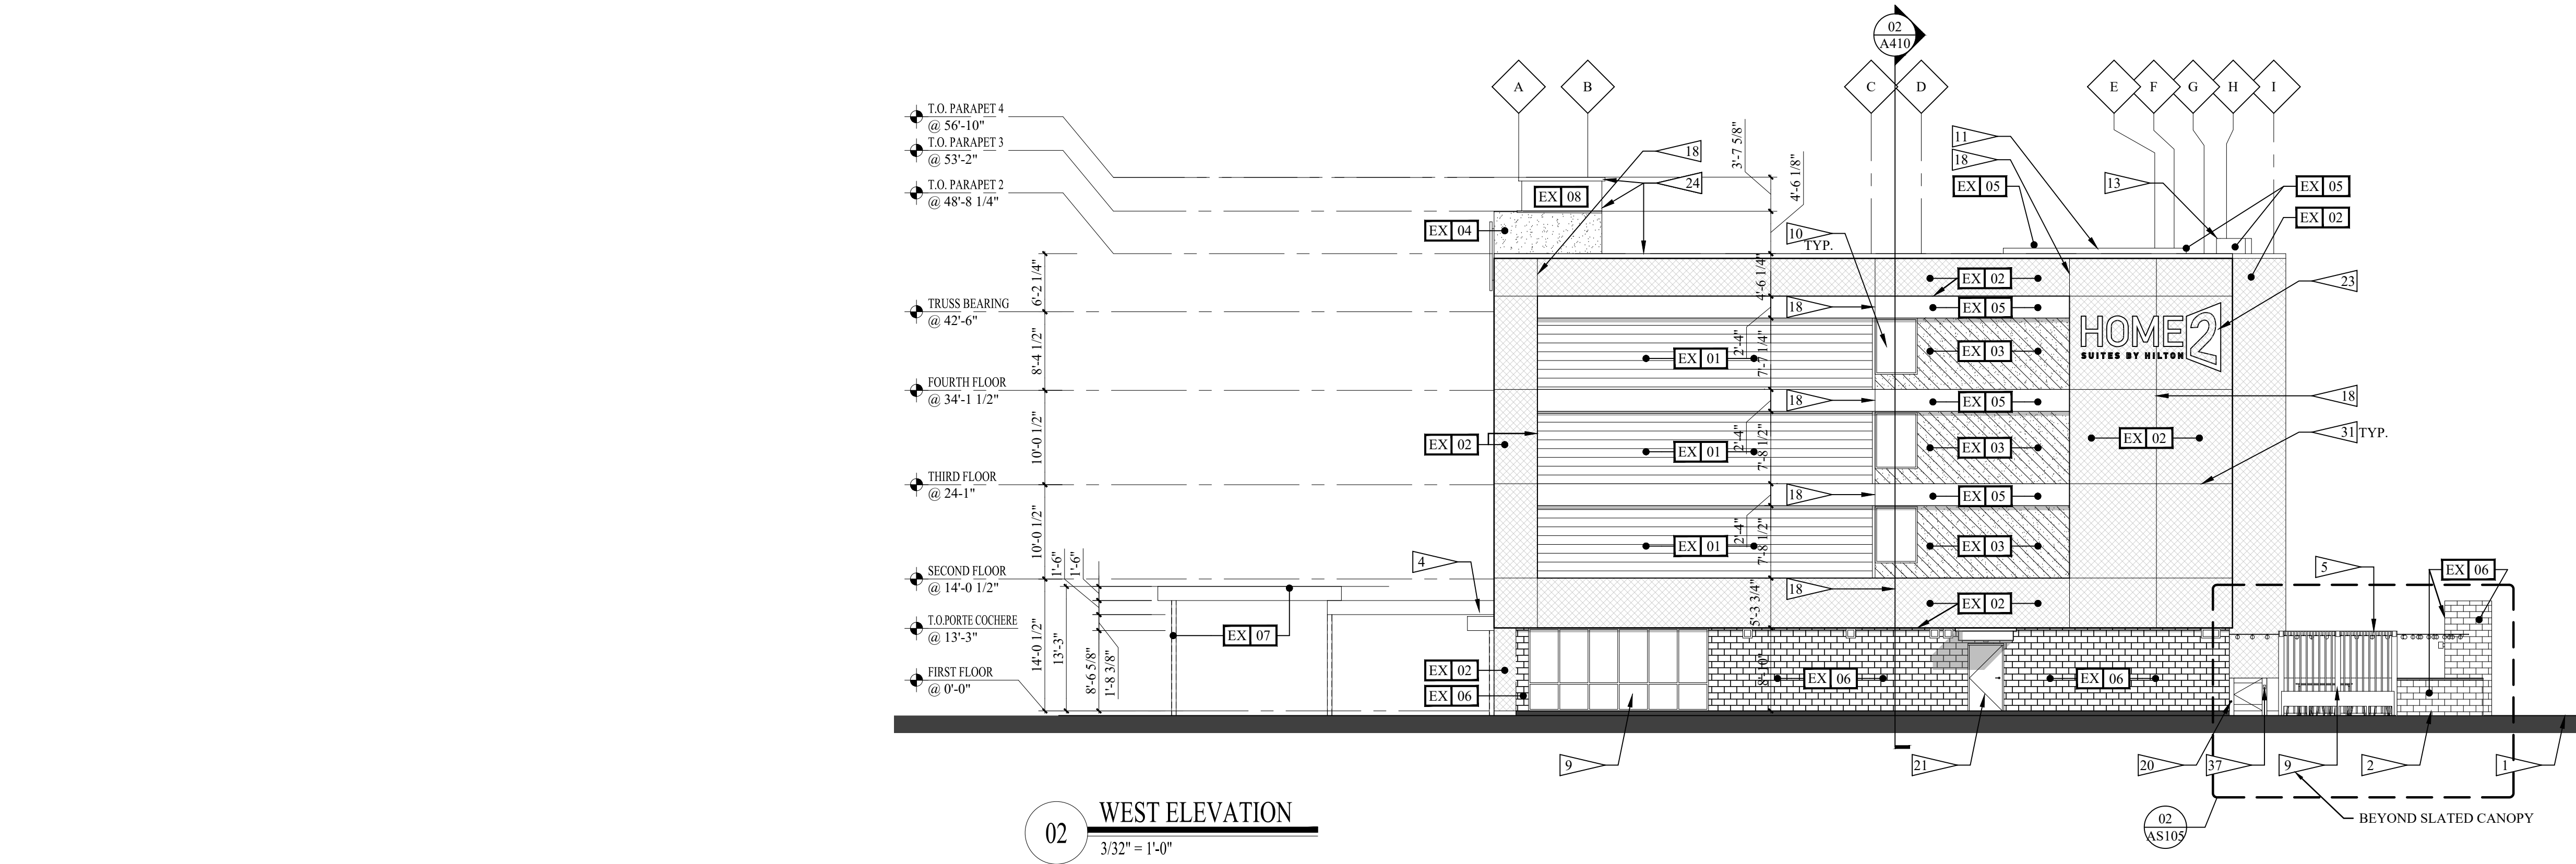


IMPORTANT NOTICE TO ALL CONTRACTORS AND OR SUBCONTRACTORS: (COMPLETE BUILDING SYSTEMS AND OR INSTALLATIONS)

IF AWARDED A CONTRACT FOR ANY PORTION OF WORK NEEDED TO COMPLETE THIS PROJECT YOU ARE AGREEING TO THE FOLLOWING TERMS:
1. YOU ARE A QUALIFIED CONTRACTOR AND OR SUBCONTRACTOR SPECIFICALLY IN PROVIDING A COMPLETE TURNKEY SERVICE IN YOUR TRADE OR PROFESSION FOR THE TYPE OF WORK AND SCOPE FOR THIS PROJECT.
2. YOU AGREE TO PROVIDE A COMPLETE DESIGN BUILD SOLUTION BASED ON THE ARCHITECT'S INTENDED DESIGN FOR THIS PROJECT.
3. YOUR BID INCLUDES ALL THE STEPS, PROCESSES, MATERIALS, PRODUCTS, GOVERNING PERMITS AND APPROVALS NECESSARY TO PROVIDE A COMPLETED AND WARRANTED SYSTEM OR INSTALLATION THAT DOES NOT REQUIRE ANOTHER CONTRACTOR OR PRODUCT TO COMPLETE YOUR SCOPE OF WORK.
4. YOUR BID MUST HAVE INCLUDED ANY DESIGN INFORMATION REFERENCED WITHIN ANY CIVIL, ARCHITECTURAL, STRUCTURAL, MECHANICAL, ELECTRICAL AND OR PLUMBING DRAWINGS; ALSO NOTE THESE DRAWINGS ARE SCHEMATIC AND ARE INTENDED TO SHOW ONLY BASIC CONCEPTS AND GENERAL INFORMATION; THE COMPLETION OF YOUR WORK MUST INCLUDE OTHER STEPS, PROCESSES, MATERIALS, PRODUCTS, LABOR, GOVERNING PERMITS AND OR APPROVALS NECESSARY TO PROVIDE A COMPLETE SYSTEM INSTALLATION WHETHER SUGGESTED ON THE DRAWINGS OR NOT.
5. AS AN EXAMPLE: ITEMS AND OR TASKS LIKE: FIRE CAULK, DRAFT STOPS, FASTENERS, ANCHORS, EMBEDMENTS, DUMPSTERS, DEBRIS CLEAN UP, ETC. ARE YOUR RESPONSIBILITY. ANY WORK NOT COMPLETED IN A TIMELY MANNER, OR INCOMPLETE WORK WILL BE BILLED BACK TO THE CONTRACTOR AND OR SUBCONTRACTOR, AT THE OWNER'S DISCRETION.

ARCHITECTURAL ELEMENTS

- EX-1 FIBER CEMENT SIDING
COLOR: SAN FRANCISCO BAY
TEXTURE: MEDIUM FINISH
CORE: BODY
BACKGROUND FOR LAYERING
OF ALL OTHER MATERIALS
- EX-2 EIFS. COLOR: MEDITERRANEAN
BREEZE
TEXTURE: FINE FINISH
WRAP: UNIFIED ELEMENT SET
PROUD (12" MIN) FROM THE CORE
- EX-3 EIFS. COLOR: DOWNPOUR BLUE
TEXTURE: SMOOTH FINISH
LINK: CONNECTION
PIECE TO BREAK UP LARGE
SEGMENTS OF THE WRAP
- EX-4 EIFS. COLOR: DOWNPOUR BLUE
TEXTURE: SMOOTH FINISH
KEEP: FOREGROUND ELEMENT OF
BEACON PLACED ON PRIMARY
BUILDING ENTRY ELEVATION IN
CONJUNCTION WITH THE PORT
COCHERE AND WITH CLEAR
VISIBILITY FROM THE FRONTAGE
ROAD. EXTENDS UP BEYOND THE
WRAP. BACKGROUND FOR
PRIMARY BUILDING SIGN.
- EX-5 EIFS. COLOR: WHITE
TEXTURE: SMOOTH FINISH
ACCENT BAND: ARTICULATION
HORIZONTAL 3D BAND PROUD OF
CORE. SUFFICIENT DEPTH (2" MIN)
TO CREATE DISTINCT SHADOW
LINE. NO VISIBLE JOINTS.
- EX-6 FACE BRICK. COLOR: STONE
TEXTURE: SANDSTONE LIKE
SUPPORT: BASE
- EX-7 CANOPY. COLOR: WHITE
TEXTURE: SMOOTH
- EX-8 EIFS. COLOR: BRIGHT LIME
TEXTURE: SMOOTH
BEAM: VERTICAL ELEMENT
SEE BACK IN PLANE FROM
THE KEEP. EXTENDS TO
THE GROUND. COMPOSED OF
THREE ELEMENTS:

GENERAL NOTES - ELEVATION

REFER TO HOME 2 SUITES BY HILTON STANDARDS
MANUAL GUIDE FOR ADDITIONAL INFORMATION
REGARDING EXTERIOR MATERIALS, CONSTRUCTION
REQUIREMENTS AND SIGNAGE REQUIREMENTS.

GROUT COLOR TO MATCH EXTERIOR TILE
OR MASONRY.

BUILDING HEIGHT DIMENSIONS ARE BASED ON
WOOD FRAME CONSTRUCTION. THESE DIMENSIONS
WILL VARY BASED ON FINAL BUILDING
CONSTRUCTION. INTERIOR CEILING HEIGHTS ARE
CRITICAL TO MAINTAIN AS MINIMUMS.

KEYED NOTES

- 1 APPROXIMATE LINE OF GRADE
2 ABOVE GRADE EXPOSED FOUNDATION WALL
4 PAINTED TUBE STEEL CANOPY WITH WOOD
FINISHED SOFFIT
5 MODIFIED WOOD CANOPY WITH STEEL SUPPORT
6 UNUSED - MECHANICAL EQUIPMENT SCREEN -
REVIEW ALL VIEWS AROUND PROPERTY BEFORE
LOCATING ALL ROOF TOP MECHANICAL UNITS.
VERIFY ALL EQUIPMENT IS ADEQUATELY SCREENED
8 ALUMINUM FIXED WINDOW WITH THERMAL
BROKEN FRAME, INSULATED GLAZING WITH
INTEGRAL ALUMINUM LOUVER AT PTAC UNITS - SEE
SHEET A-601 FOR SIZES.
9 ALUMINUM STOREFRONT SYSTEM WITH THERMAL
BROKEN FRAME AND INSULATED GLAZING
10 ALUMINUM FIXED WINDOW WITH THERMAL
BROKEN FRAME AND ULATED GLAZING
11 ELEVATOR OVERRUN
13 LAUNDRY CHUTE OVERRUN
18 FINISH CONTROL JOINT
19 OVERFLOW SCUPPER - BASIS OF DESIGN NESCO MFG
INC. - MODEL # SCT914R - REFER ALSO TO DETAIL
7/A-303
20 TAMPER RESISTANT, RECESSED HOSE BIBB - MOUNT
TOP AT +12" A.F.F
21 PAINTED EXT. DOOR&FRAME. COLOR TO MATCH
WITH ADJACENT EXTERIOR MATERIAL
23 SIGNAGE - REFER TO EXTERIOR SIGNAGE
SPECIFICATIONS. PROVIDE 5/8" TYP. X SHEATHING
FOR SUPPORT
24 KYNAR FINISH ALUMINUM COPING SYSTEM --COLOR
TO MATCH ADJACENT MATERIAL
25 KYNAR FINISH ALUMINUM GRAVEL STOP --COLOR
TO MATCH ADJACENT MATERIAL
30 LIGHT FIXTURE - REFER TO CEILING PLAN
31 EXPANSION JOINT AT FLOOR LINE W/ BACKER ROD
32 ALUMINUM LOUVER - COLOR TO MATCH ADJACENT
MATERIAL MATCHING ADJACENT WALL
33 BUILDING HEIGHT DIMENSIONS ARE BASED ON
WOOD FRAME CONSTRUCTION. DIMENSIONS WILL
VARY BASED ON FINAL BUILDING CONSTRUCTION.
INTERIOR CEILING HEIGHT DIMENSIONS ARE
CRITICAL TO MAINTAIN AS MINIMUMS.
36 ALUMINUM GUTTER AND DS. COLOR TO MATCH ADJ.
MATERIAL
37 ACCESSIBLE KEY CARD READER WIRED TO
ELECTRIC STRIKE IN DOOR - TOP OF READER AT 48"
MAX. HEIGHT
38 POOL PERIMETER FENCE AS REQUIRED BY CODE
WITH 3'-0" GATE
39 PRECAST COPING



3827 BILLO ROAD
ALDEN, NY, 14004
716-631-0600
ARCHITECT OF RECORD

DONALD M. EDWARD
LICENSE #: 20212
10800 ALABASTER DR.
DAVIDSON, NC 28036
donedwardarchitect@gmail.com



WARNING
IT IS A VIOLATION OF THE LAW FOR ANY
PERSON, UNLESS ACTING UNDER THE
DIRECTION OF THE ARCHITECT OR ENGINEER,
TO ALTER OR REPRODUCE THESE DRAWINGS
IN ANY WAY.

DRAWING QUESTIONS
CA@MWTUSA.COM
1-800-717-5816

ISSUED FOR :

CONSTRUCTION AND BID SET



EAGLE PASS, TX 78852
PROTOTYPE VERSION: 3.0

REVISIONS

NO.	DESCRIPTION	DATE	BY
1	FF&E FRANCHISE UPDATE	-	-
2	PER STRUCTURAL UPDATE	-	-
3	REVISED PER CITY COMMENT	-	-
4	REVISED	08/09/24	-

PROJECT NO.: 22-014

DATE: 08/09/24

DRAWN BY: RH/AA/BS

CHKD. BY: AS

**BUILDING
ELEVATION**

SHEET

A201

22-014 A200-A201 BUILDING ELEVATION.dwg