



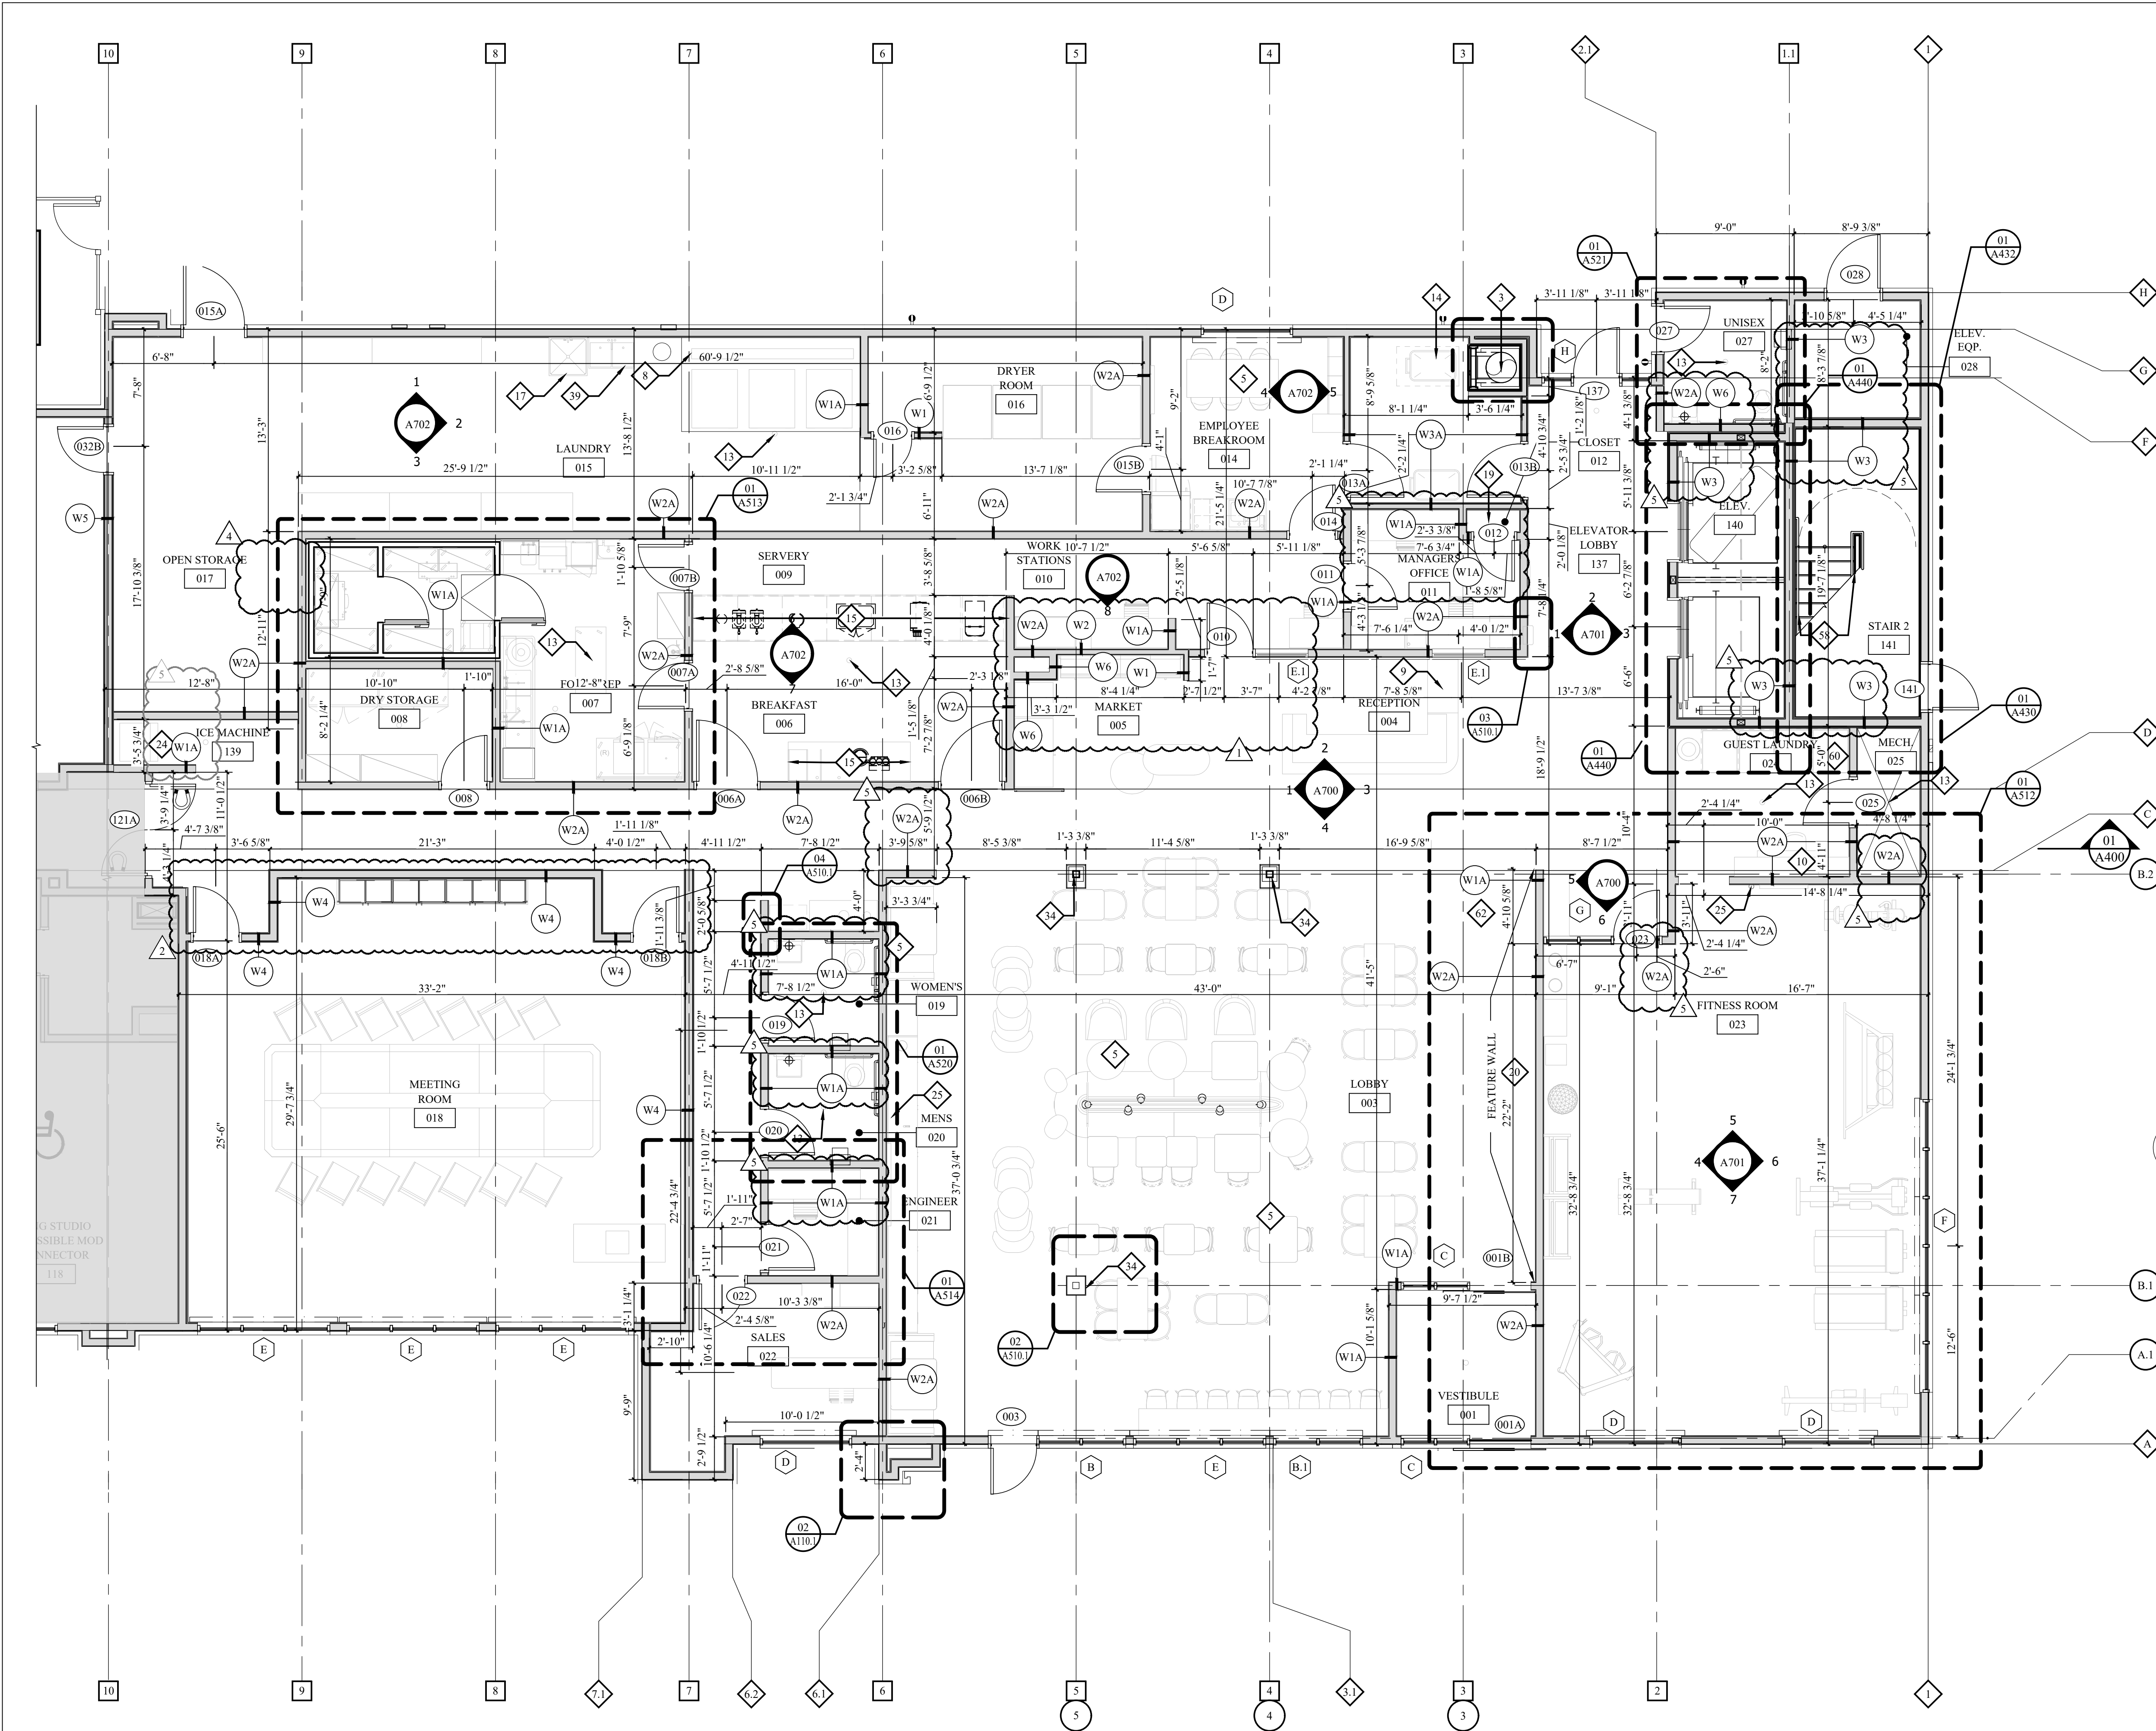


01 LOBBY AREA - CONSTRUCTION PLAN
3/16" = 1'-0"


- ### GENERAL NOTES - ENLARGED PLAN
- A. ENLARGED PLAN KEYED NOTES APPLY TO A510.1 - A511.1. ALL KEYED NOTES MAY NOT OCCUR ON THIS SHEET AND DO NOT APPLY TO ANY OTHER SHEETS EXCEPT THOSE NOTED.
- ### KEYED NOTES - ENLARGED PLAN
- | | |
|----|--|
| 1 | WALL CENTERED ON COLUMN LINE |
| 3 | LAUNDRY CHUTE LOCATION CONTAINED WITHIN RATED SHAFT WITH RATED DOOR. RATING VARIES DEPENDING ON BUILDING HEIGHT PER STANDARDS. |
| 5 | ACCESSIBLE TABLE, REFER TO FF&E SPECIFICATIONS |
| 6 | PHONE RACK |
| 8 | TRENCH DRAIN FOR WASHING MACHINES |
| 9 | REGISTRATION DESK WITH ACCESSIBLE APPROACH; REFER TO FF&E PACKAGE AND HADG FOR FURTHER INFORMATION |
| 10 | ACCESSIBLE WORK TABLE |
| 13 | FLOOR DRAIN |
| 14 | LINEN CART STORAGE AREA |
| 15 | BREAKFAST COUNTER |
| 16 | LUGGAGE CART STORAGE |
| 17 | 36" x 36" MOP SINK LOCATION |
| 18 | MATV RACK |
| 19 | SAFETY DEPOSIT BOX LOCATION |
| 20 | FEATURE WALL |
| 21 | MAINTENANCE DESK |
| 22 | FIRE EXTINGUISHER |
| 24 | ACCESSIBLE ICE MACHINE WITH REQUIRED ACCESSIBLE APPROACH AREA. PROVIDE FLOOR DRAIN CENTERED UNDER ICE MACHINE AND PROVIDE POSITIVE SLOPE TOWARDS DRAIN WITHOUT AFFECTING ACCESSIBLE REQUIREMENTS, INSULATE DRAIN PIPES. REFER TO HOME 2 SUITES BY HILTON STANDARDS MANUAL AND HADG FOR ADDITIONAL REQUIREMENTS FOR ICE MACHINE AREA. |
| 25 | TV LOCATION |
| 32 | WORK BENCH PER STANDARDS |
| 33 | ON RACK |
| 34 | STRUCTURAL COLUMNS - FINISH: WC-01 |
| 35 | 4' X 8' PLYWOOD SHEET |
| 39 | TWO (2) COMPARTMENT SINK |
| 43 | VANITY AND MIRROR (VANITY MUST NOT ENCRATCH INTO CLEAR FLOOR SPACE FOR ACCESSIBLE TOILET) |
| 44 | ACCESSIBLE LOW FLOW TOILET |
| 45 | TOWEL DISPENSER / TRASH CAN |
| 46 | SOAP DISPENSER |
| 53 | PROVIDE POWER FOR PLUG IN STRING LIGHT |
| 58 | PAINT UNDERSIDE OF STAIR TO MATCH STAIR RAILING |
| 60 | PROVIDE AT LEAST ONE ACC WASHING MACHINE AND DRYER; FRONT LOAD WITH OPENING LOCATED 15" MIN & 36" MAX AFF |
| 61 | SLOPE FLOORS TO DRAIN - MAX 2% |
| 62 | HOUSE PHONE |

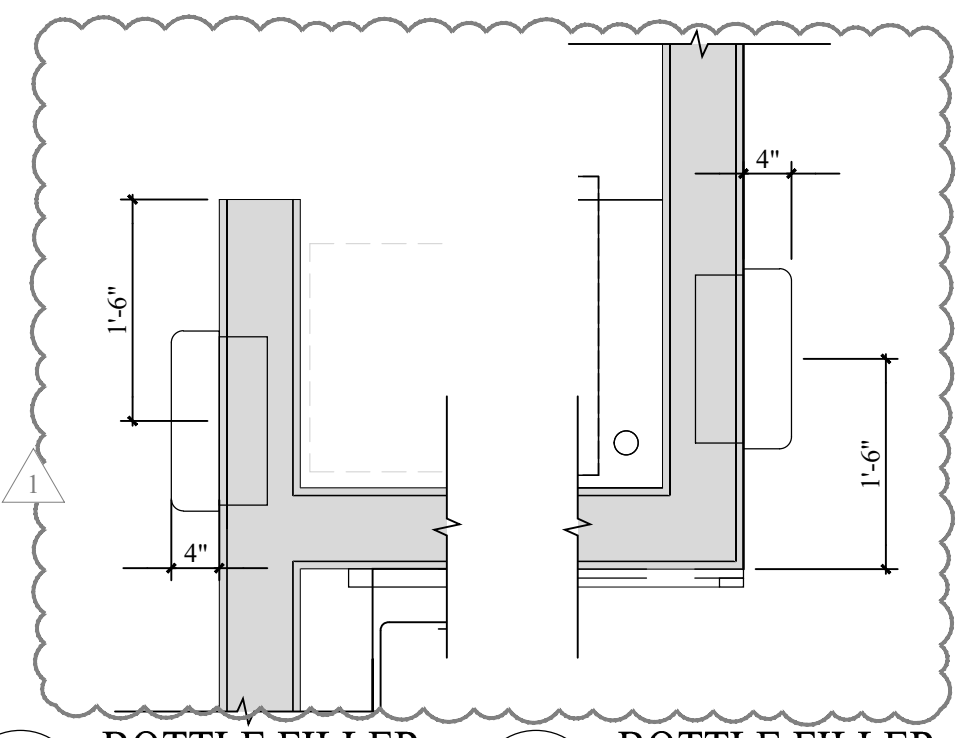

04 BOTTLE FILLER 3/4" = 1'-0"
03 BOTTLE FILLER 3/4" = 1'-0"

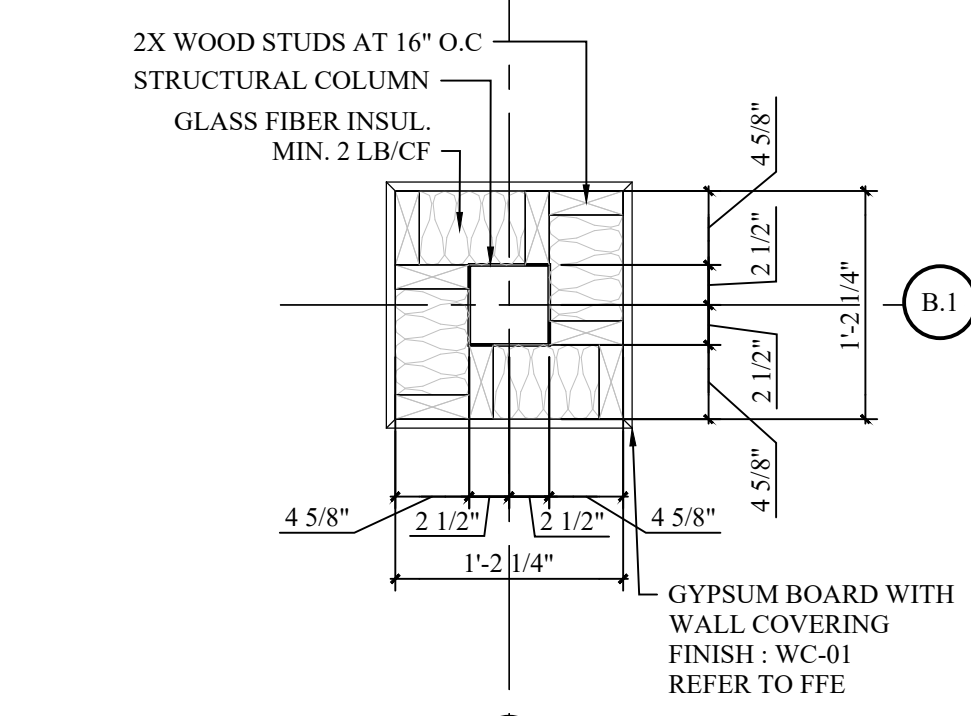

02 COLUMN DETAIL
1" = 1'-0"

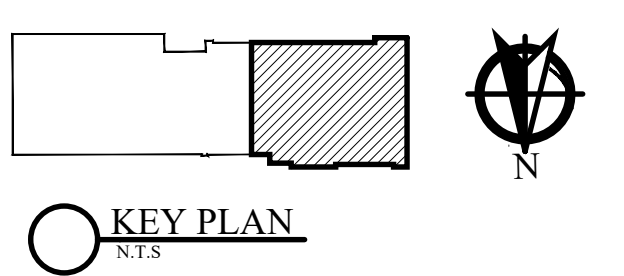

IMPORTANT NOTICE TO ALL CONTRACTORS AND OR SUBCONTRACTORS: (COMPLETE BUILDING SYSTEMS AND OR INSTALLATIONS)

IF AWARDED A CONTRACT FOR ANY PORTION OF WORK NEEDED TO COMPLETE THIS PROJECT YOU ARE AGREEING TO THE FOLLOWING TERMS:

- YOU ARE A QUALIFIED CONTRACTOR AND OR SUBCONTRACTOR SPECIFICALLY IN PROVIDING A COMPLETE TURNKEY SERVICE IN YOUR TRADE OR PROFESSION FOR THE TYPE OF WORK AND SCOPE FOR THIS PROJECT.
- YOU AGREE TO PROVIDE A COMPLETE DESIGN BUILD SOLUTION BASED ON THE ARCHITECT'S INTENDED DESIGN FOR THIS PROJECT.
- YOUR BID INCLUDED ALL THE STEPS, PROCESSES, MATERIALS, PRODUCTS, GOVERNING PERMITS AND OR APPROVALS NECESSARY TO PROVIDE A COMPLETED AND WARRANTED SYSTEM OR INSTALLATION THAT DOES NOT REQUIRE ANOTHER CONTRACTOR OR PRODUCT TO COMPLETE YOUR SCOPE OF WORK.
- YOUR BID MUST INCLUDE ANY DESIGN INFORMATION REFERENCED WITHIN ANY CIVIL, ARCHITECTURAL, STRUCTURAL, MECHANICAL, ELECTRICAL AND OR PLUMBING DRAWINGS; ALSO NOTE THESE DRAWINGS ARE SCHEMATIC AND ARE INTENDED TO SHOW ONLY BASIC CONCEPTS AND GENERAL INFORMATION. THE COMPLETION OF YOUR WORK NOT INCLUDING STEPS, PROCESSES, MATERIALS, PRODUCTS, LABOR, GOVERNING PERMITS AND OR APPROVALS NECESSARY TO PROVIDE A COMPLETE SYSTEM INSTALLATION WHETHER SUGGESTED ON THE DRAWINGS OR NOT.
- AS AN EXAMPLE: ITEMS AND OR TASKS LIKE: FIRE CAULK, DRAFT STOPS, FASTENERS, ANCHORS, EMBEDEDMENTS, DUMPSTERS, DEBRIS CLEAN UP, ETC. ARE YOUR RESPONSIBILITY. ANY WORK NOT COMPLETED IN A TIMELY MANNER, OR INCOMPLETE WORK WILL BE BILLED BACK TO THE CONTRACTOR AND OR SUBCONTRACTOR, AT THE OWNERS' DISCRETION.

3827 BILLO ROAD
ALDEN, NY, 14004
716-631-0600
ARCHITECT OF RECORD

DONALD M. EDWARD
LICENSE #: 20212
10800 ALABASTER DR.
DAVIDSON, NC 28036
donedwardarchitect@gmail.com

08/09/2024

WARNING:
IT IS A VIOLATION OF THE LAW FOR ANY PERSON, UNLESS ACTING UNDER THE DIRECTION OF THE ARCHITECT OR ENGINEER, TO ALTER OR REPRODUCE THESE DRAWINGS IN ANY WAY.

DRAWING QUESTIONS
CA@MWTUSA.COM
1-800-717-5816

ISSUED FOR :
CONSTRUCTION AND BID SET

HOME 2
SUITES BY HILTON

EAGLE PASS, TX 78852
PROTOTYPE VERSION: 3.0

REVISIONS			
NO.	DESCRIPTION	DATE	BY
1	FF&E FRANCHISE UPDATE	08/04/23	-
2	PER STRUCTURAL UPDATE	10/20/23	-
3	REVISED PER CITY COMMENT	-	-
4	REVISED	08/09/24	-
5	REVISED PER RFI	12/12/24	-

PROJECT NO.: 22-014
DATE: 08/09/24
DRAWN BY: MA/RH/BS
CHKD. BY: AS

ENLARGED LOBBY - CONST. PLAN

SHEET
A510.1

22-014 A510.1 ENLARGED LOBBY - CONST.dwg