

DRAWING QUESTIONS
CA@MWTUSA.COM
1-800-717-5816

ISSUED FOR :
CONSTRUCTION AND BID SHEET



EAGLE PASS, TX 78852
PROTOTYPE VERSION: 3.0

REVISIONS		
NO.	DESCRIPTION	DATE
1	FF&E FRANCHISE UPDATE	08/04/23
2	PER STRUCTURAL UPDATE	-
3	REVISED PER CITY COMMENT	-
4	REVISED	08/09/24

PROJECT NO.: 22-014
DATE: 08/09/24
DRAWN BY: MA/RH/BS
CHKD. BY: AS

ENLARGED LOBBY
FURNITURE &
EQUIPMENT PLAN

SHEET
A510.3

22-014 A510.3 ENLARGED LOBBY • FURNITURE & EQUIPMENT PLAN.

A. ENLARGED PLAN KEYED NOTES APPLY TO A510.1 - A511.1. ALL KEYED NOTES MAY NOT OCCUR ON THIS SHEET AND DO NOT APPLY TO ANY OTHER SHEETS EXCEPT THOSE NOTED.

1	TRASH CAN, RECYCLING BIN, & ASH BIN
2	GENERAL CONTRACTOR TO PROVIDE PLATE MIRROR FOR RECEIPT OF DECORATIVE FRAME (REFER TO HOME FITNESS GUIDE FOR ADDITIONAL INFO.
3	THIS UNIT CONTAINS A DISH RECOVERY CART & (2) TRASH CANS, COORDINATE W/ MILLWORK VENDOR RECEPTION OF DECORATIVE FRAME (REFER TO HOME FITNESS GUIDE FOR ADDITIONAL INFO.
4	OFFICE FURNITURE BY OWNER AS REQ'D
6	EMPLOYEE LOCKERS SHALL COMPLY W/ ACCESSIBILITY STANDARDS FOR PERCENTAGE OF ACCESSIBLE STORAGE -REFER TO HADG FOR REQ'S
7	AN EMERGENCY TELEPHONE MUST BE PROVIDED, MOUNTED WITHIN ACCESSIBLE REACH RANGE. PHONE MUST BE PROVIDED WITH VOLUME CONTROL & A MIN. 28" LOUVERED, AN ACCESSIBLE ROUTE MUST BE PROVIDED TO THE EMERGENCY HOUSE PHONE WITH A CLEAR FLOOR SPACE TO THE PHONE.
8	PROVIDE OPENINGS FOR TRASH, RECYCLING AND COMPOST AS NECESSARY
9	SEE FOOD SERVICE DWGS FOR EQUIPMENT INFORMATION
10	OS&S DISH RECOVERY CART

 FURNITURE & EQUIPMENT TAGS

 KEYED NOTES

300 SHELVING
301 NOT USED
302 NOT USED
303 SAFE
304 LOCKER

400 FIRE PIT WITH FITTED SCREEN
401 COMMERCIAL WASHER
402 COMMERCIAL DRYER
403 WALL MOUNTED TELEVISION
404 STORAGE SHELVING
405 BREAKROOM SINK
406 COIN OPERATED WASHER
407 COIN OPERATED DRYER
408 DECORATIVE TRASHCAN
409 COMMERCIAL TOP LOAD WASHER

431 WALL MOUNTED TELEVISION
432 ICE DISPENSER

500 TOWEL HAMPER
501 WATER & CUP DISPENSER
502 GYM WIPES DISPENSER
503 TREADMILL
504 FITNESS TRAINER ELLIPTICAL
505 RECUMBENT CYCLE
506 FREE WEIGHTS & RACK
507 WEIGHT BENCH
508 STRENGTH SYSTEM
509 MEDICINE BALLS & RACK
510 EXERCISE BALL
511 EXERCISE MAT
512 RULES SIGN
513 WALL MOUNTED TELEVISION
514 EMERGENCY TELEPHONE
516 TOWEL HOOK
517 WALL MOUNTED MIRROR
519 WALL MOUNTED CLOCK
520 HYDRATION STATION
521 BOTTLE FILLING STATION


[illegible]

PROJECT NO.: 22-014
DATE: 08/09/24
DRAWN BY: MA/RH/BS
CHKD. BY: AS

ENLARGED LOBBY
FURNITURE &
EQUIPMENT PLAN

SHEET
A510.3

22-014 A510.3 ENLARGED LOBBY • FURNITURE & EQUIPMENT PLAN.

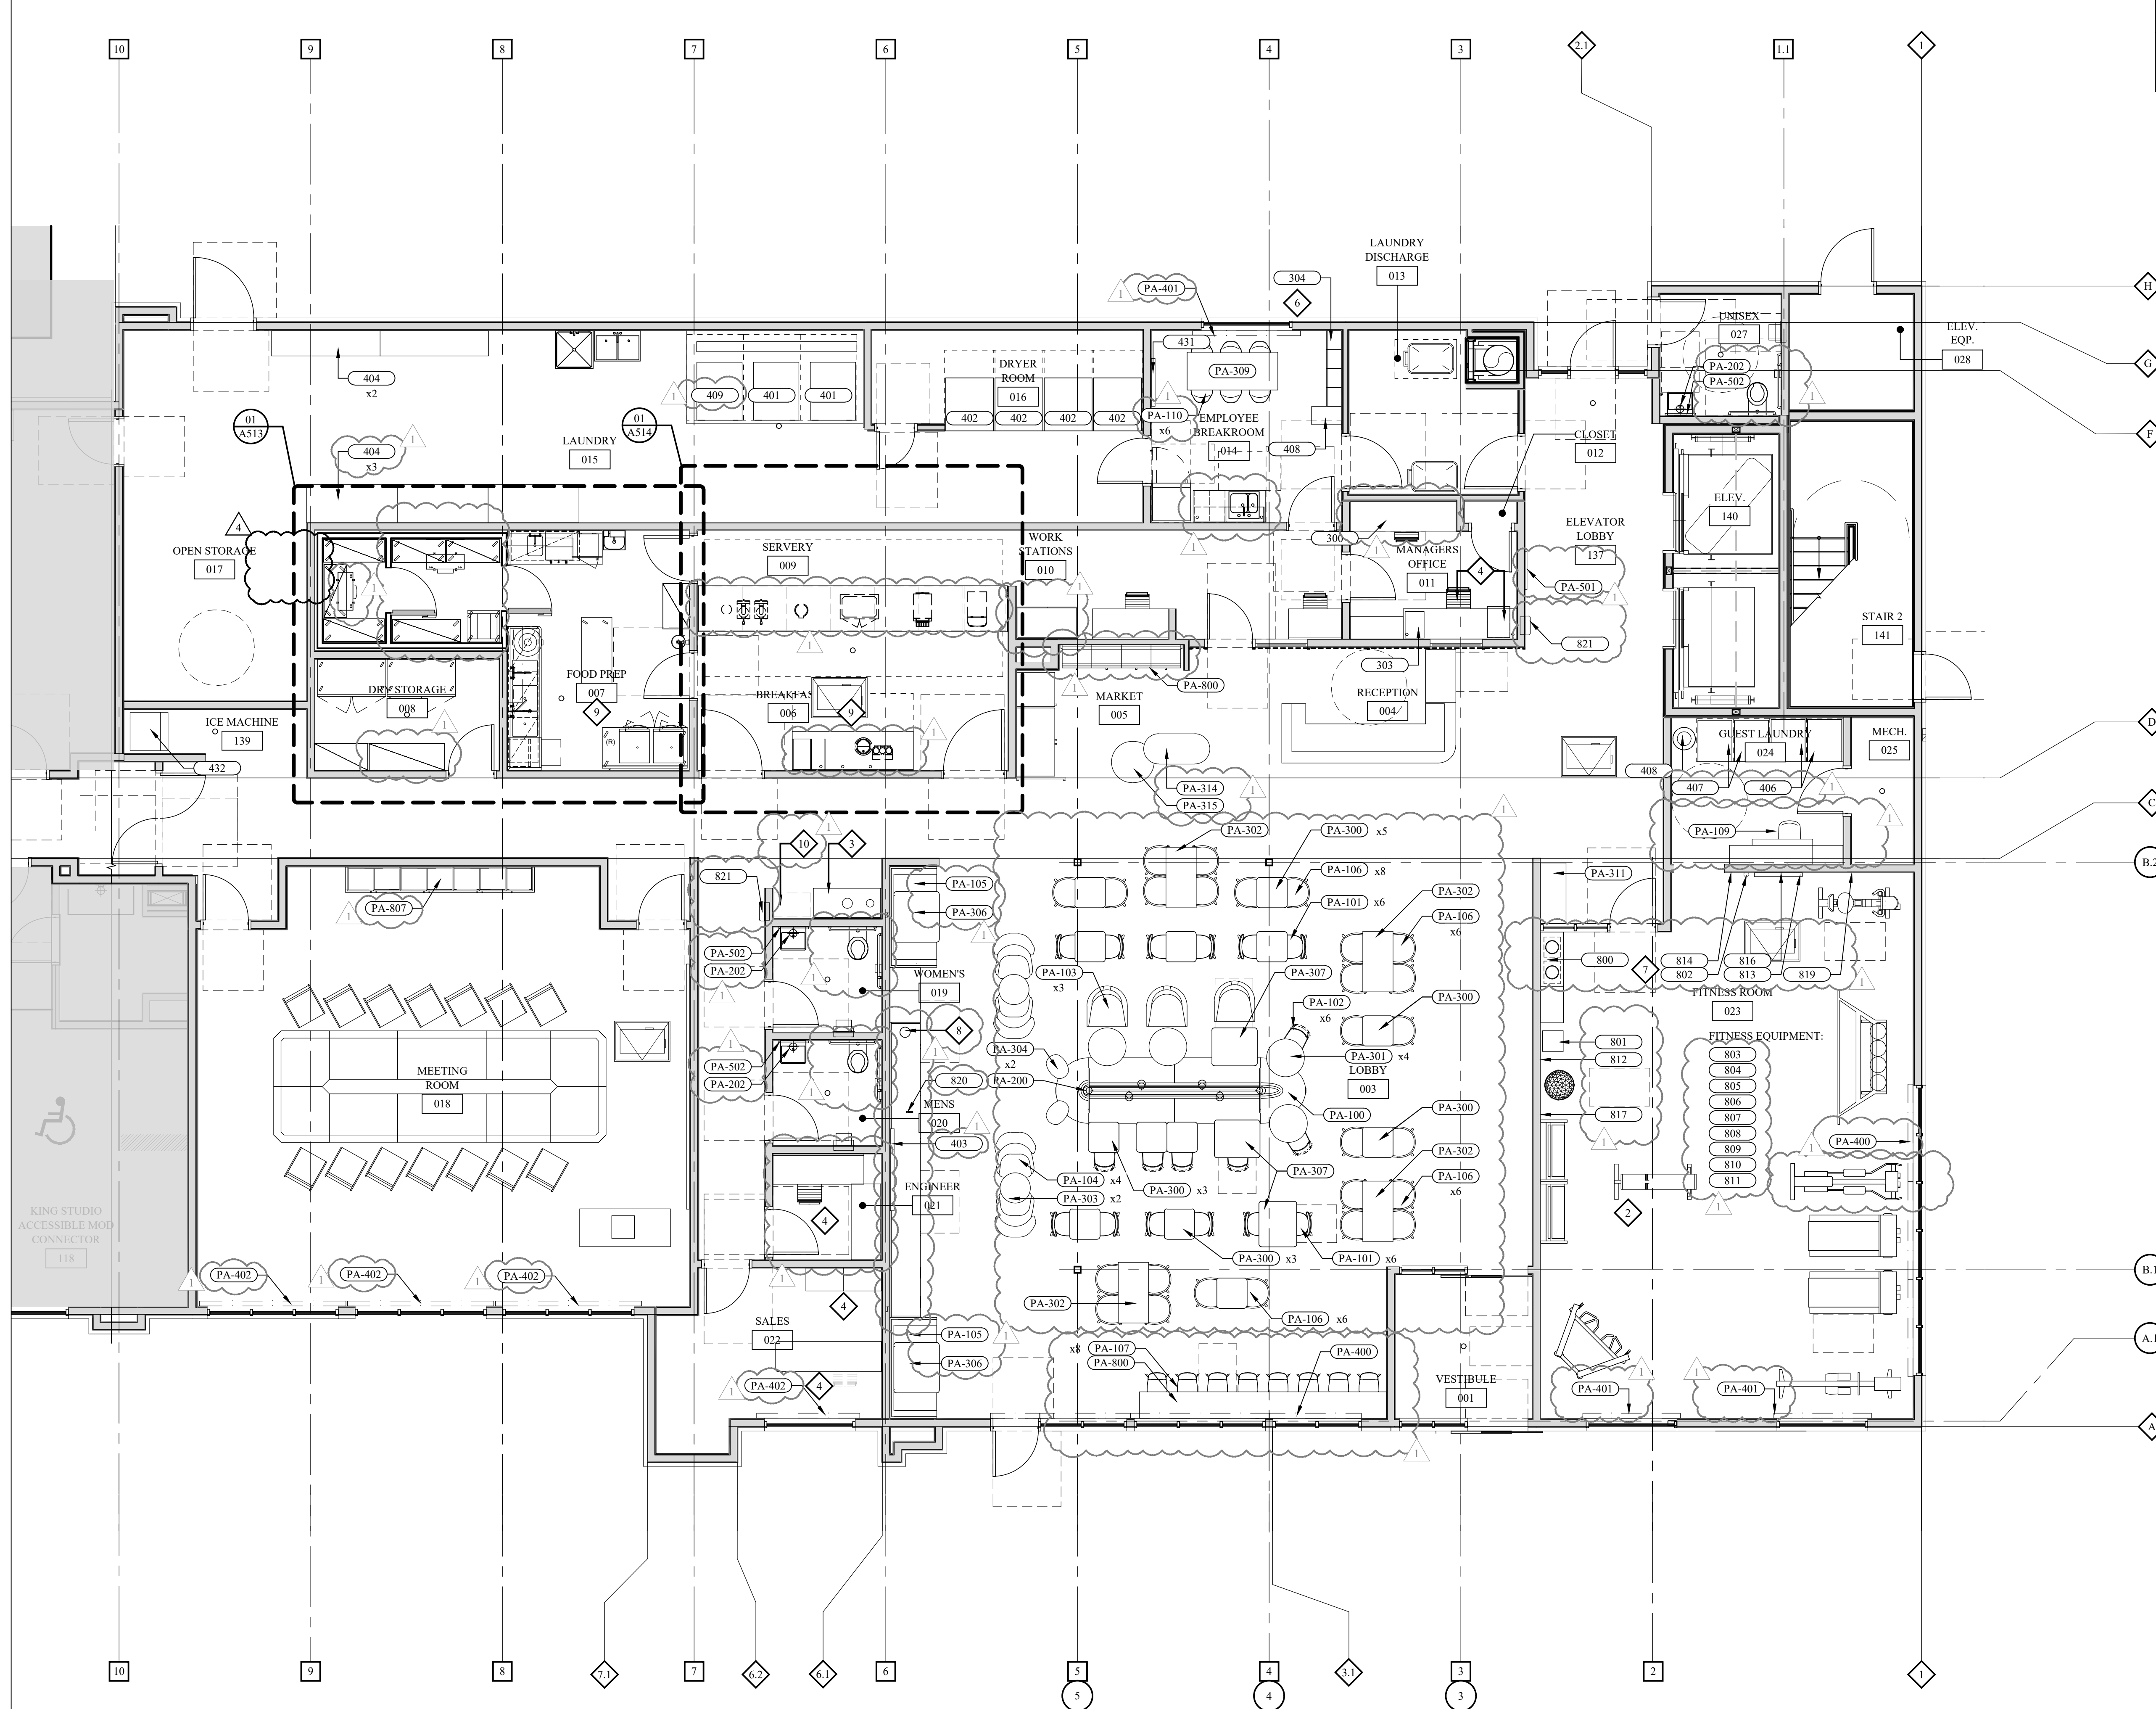

01 LOBBY AREA - FURNITURE & EQUIPMENT PLAN
3/16" = 1'-0"

01 $3/16'' = 1'-0''$

IMPORTANT NOTICE TO ALL CONTRACTORS AND OR SUBCONTRACTORS: (COMPLETE BUILDING SYSTEMS AND OR INSTALLATIONS

IF AWARDING A CONTRACT FOR ANY PORTION OF WORK NEEDED TO COMPLETE THIS PROJECT YOU ARE AGREEING TO THE FOLLOWING TERMS:

1. YOU ARE QUALIFIED CONTRACTOR AND YOUR SUBCONTRACTORS ARE QUALIFIED CONTRACTORS TO COMPLETE THIS PROJECT UNDER YOUR TRADE OR PROFESSION FOR THE TYPE OF WORK AND SCOPE OF PROJECT.

2. YOU AGREE TO PROVIDE A COMPLETE DESIGN BUILD SOLUTION BASED ON THE ARCHITECT'S INTENDED DESIGN FOR THIS PROJECT.

3. YOU AGREE TO OBTAIN ALL NECESSARY PERMITS, INSURE, POST BOND, AND OBTAIN A COMPLETE AND WARRANTY STATE OR INSTALLATION THAT DOES NOT REQUIRE ANOTHER CONTRACTOR OR PRODUCT TO COMPLETE YOUR SCOPE OF WORK.

4. YOUR BID MUST HAVE INCLUDED ANY INTERDEPENDENT INFORMATION REFERENCED WITHIN ANY CIVIL, ARCHITECTURAL, STRUCTURAL, MECHANICAL, ELECTRICAL AND/OR PLUMBING DRAWINGS; ALSO NOTE THESE DRAWINGS ARE SCHEMATIC AND ARE INTENDED TO SHOW ONLY A BASIC CONCEPTS AND GENERAL INFORMATION. **THE COMPLETION ON**

5. **AS AN EXAMPLE: ITEMS OR TAGS LIKE:** FIRE ALARM, DRAFT STOP, FASTENERS, ANCHORS, EMBLEMMENTS, DUBBING, DEBRIS CLEAN UP, ETC. ARE YOUR RESPONSIBILITY. ANY WORK NOT COMPLETED IN A TIMELY MANNER, OR INCOMPLETE WORK WILL BE LIAED BACK TO THE CONTRACTOR AND/OR SUBCONTRACTOR. AT THE OWNER'S