



LEGEND - CEILING FIXTURES	
SYMBOL	DESCRIPTION
	SURFACE LINEAR STRIP
	EMERGENCY EXIT LIGHT
	2'x2' TROFFER CEILING LIGHTING

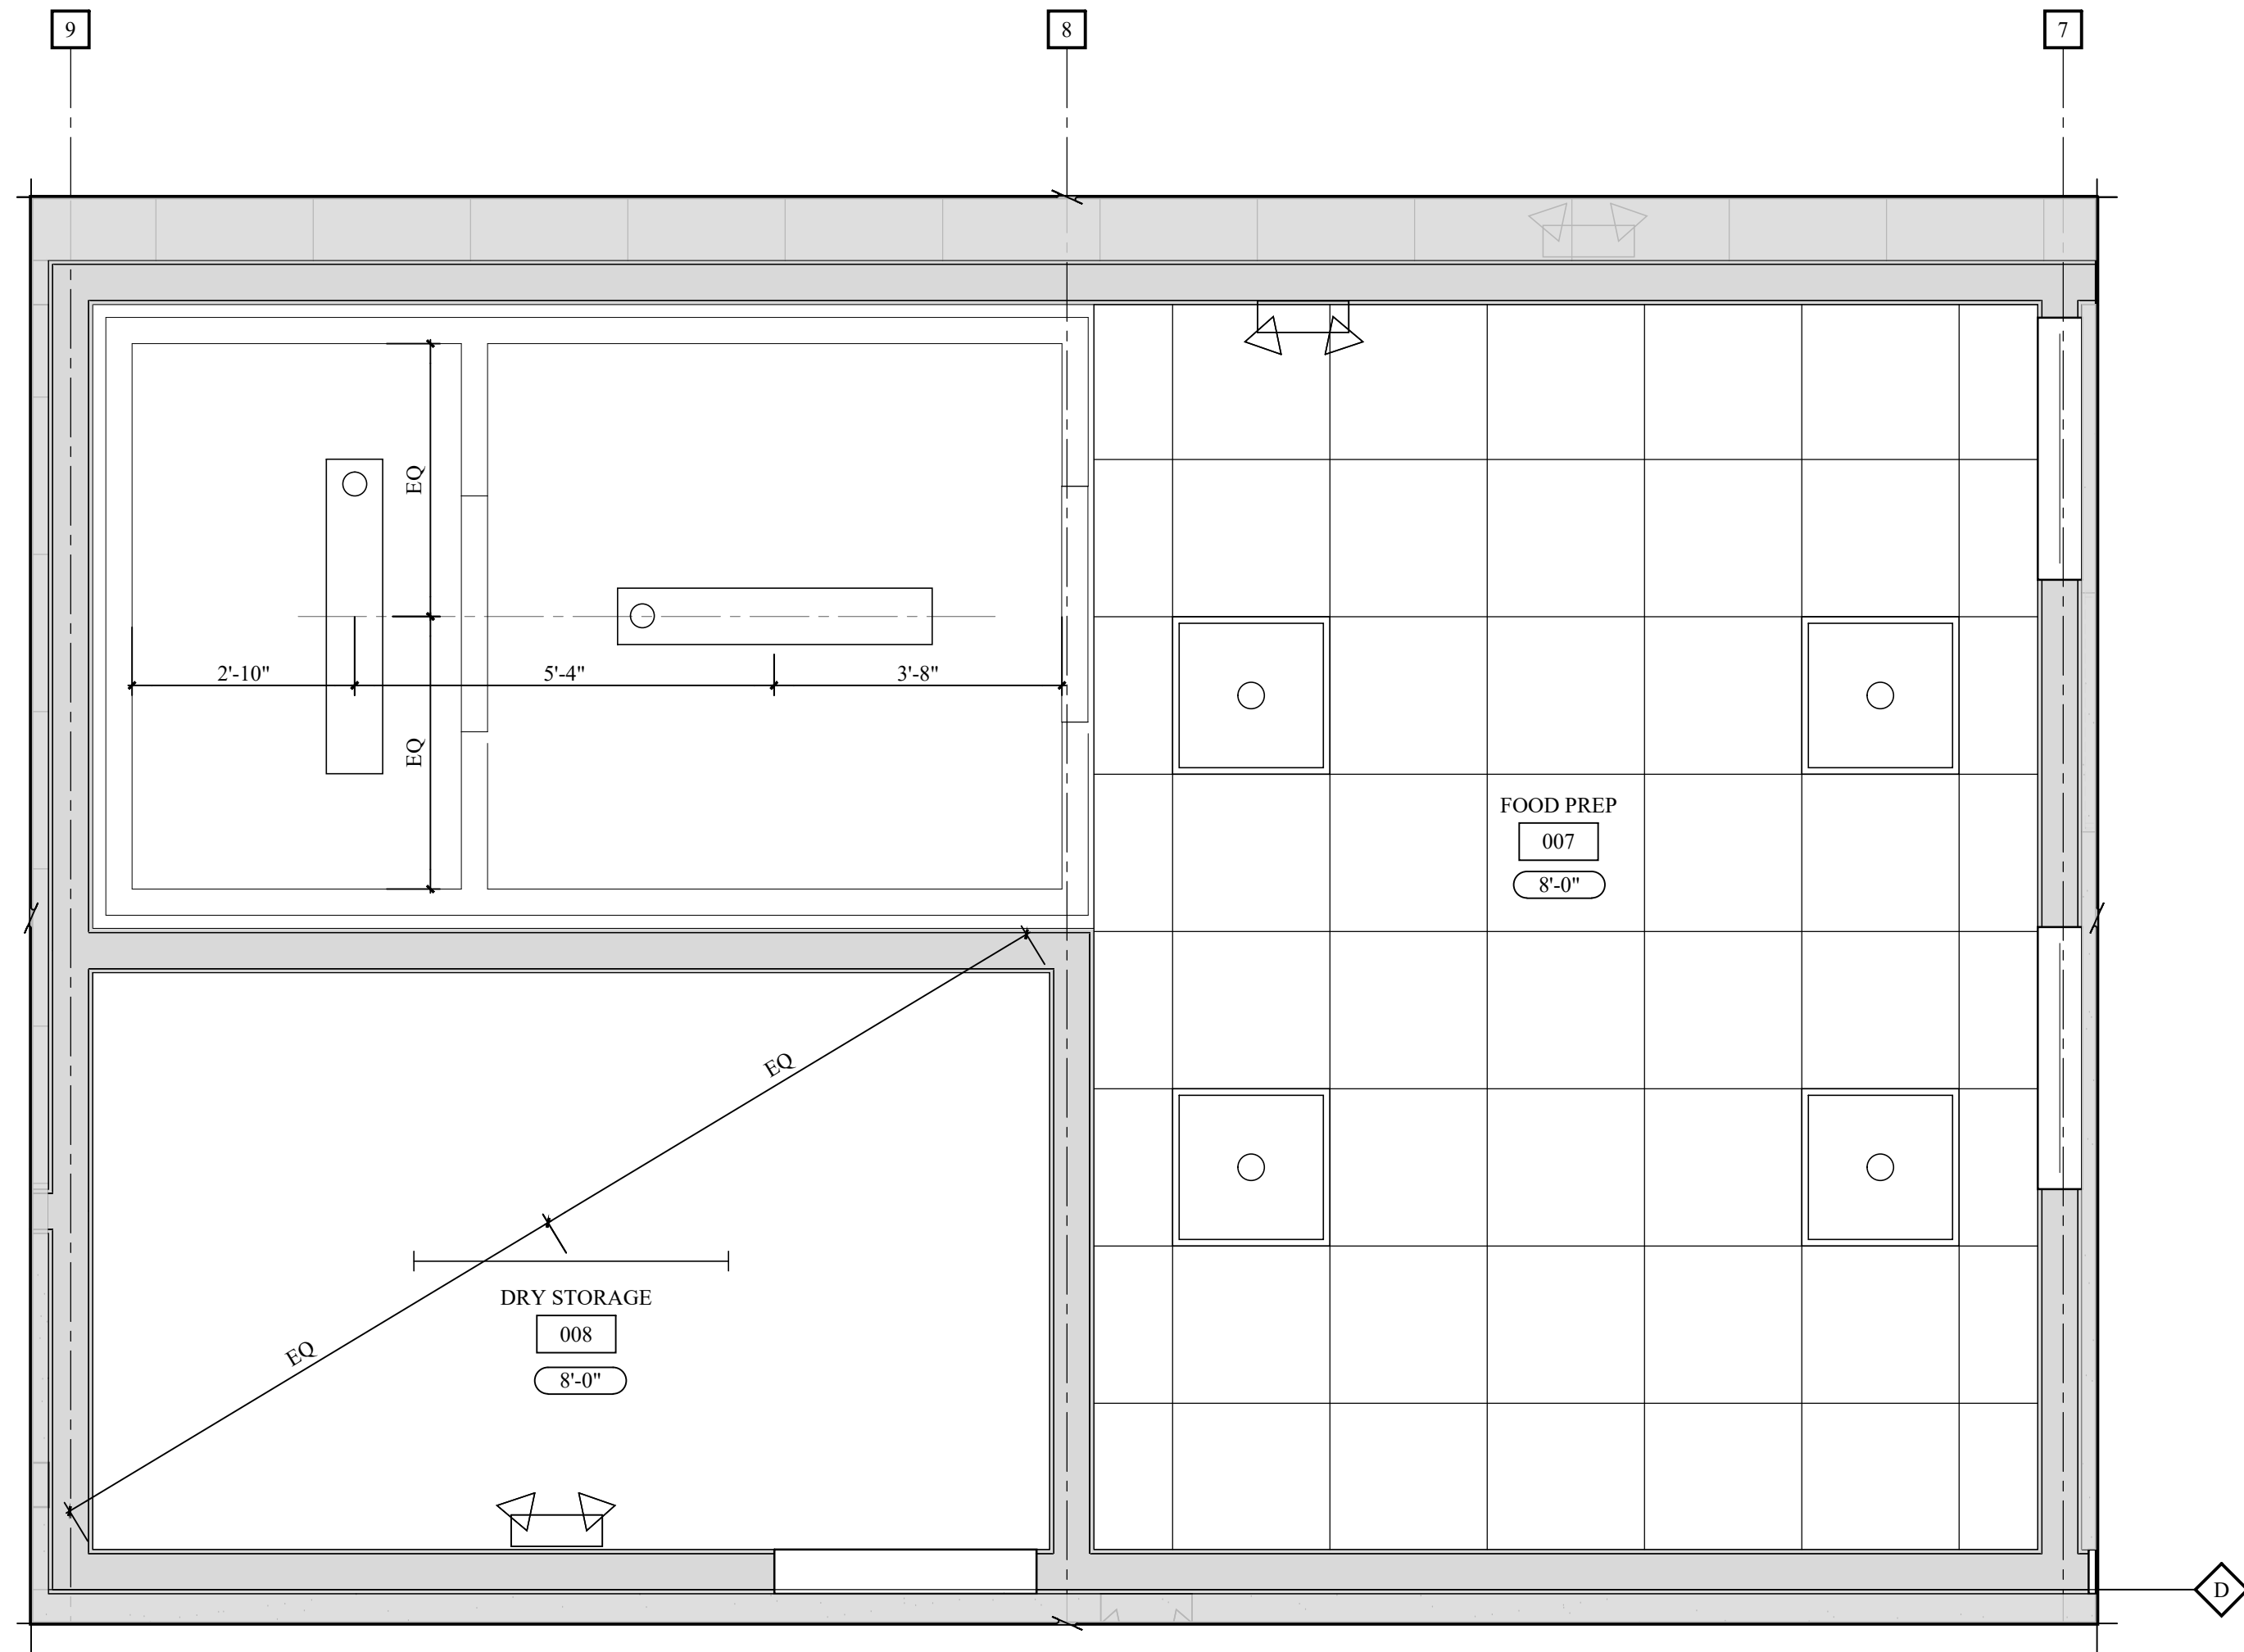

2 FOOD PREP & DRY STORAGE RCP PLAN
1/2" = 1'-0"

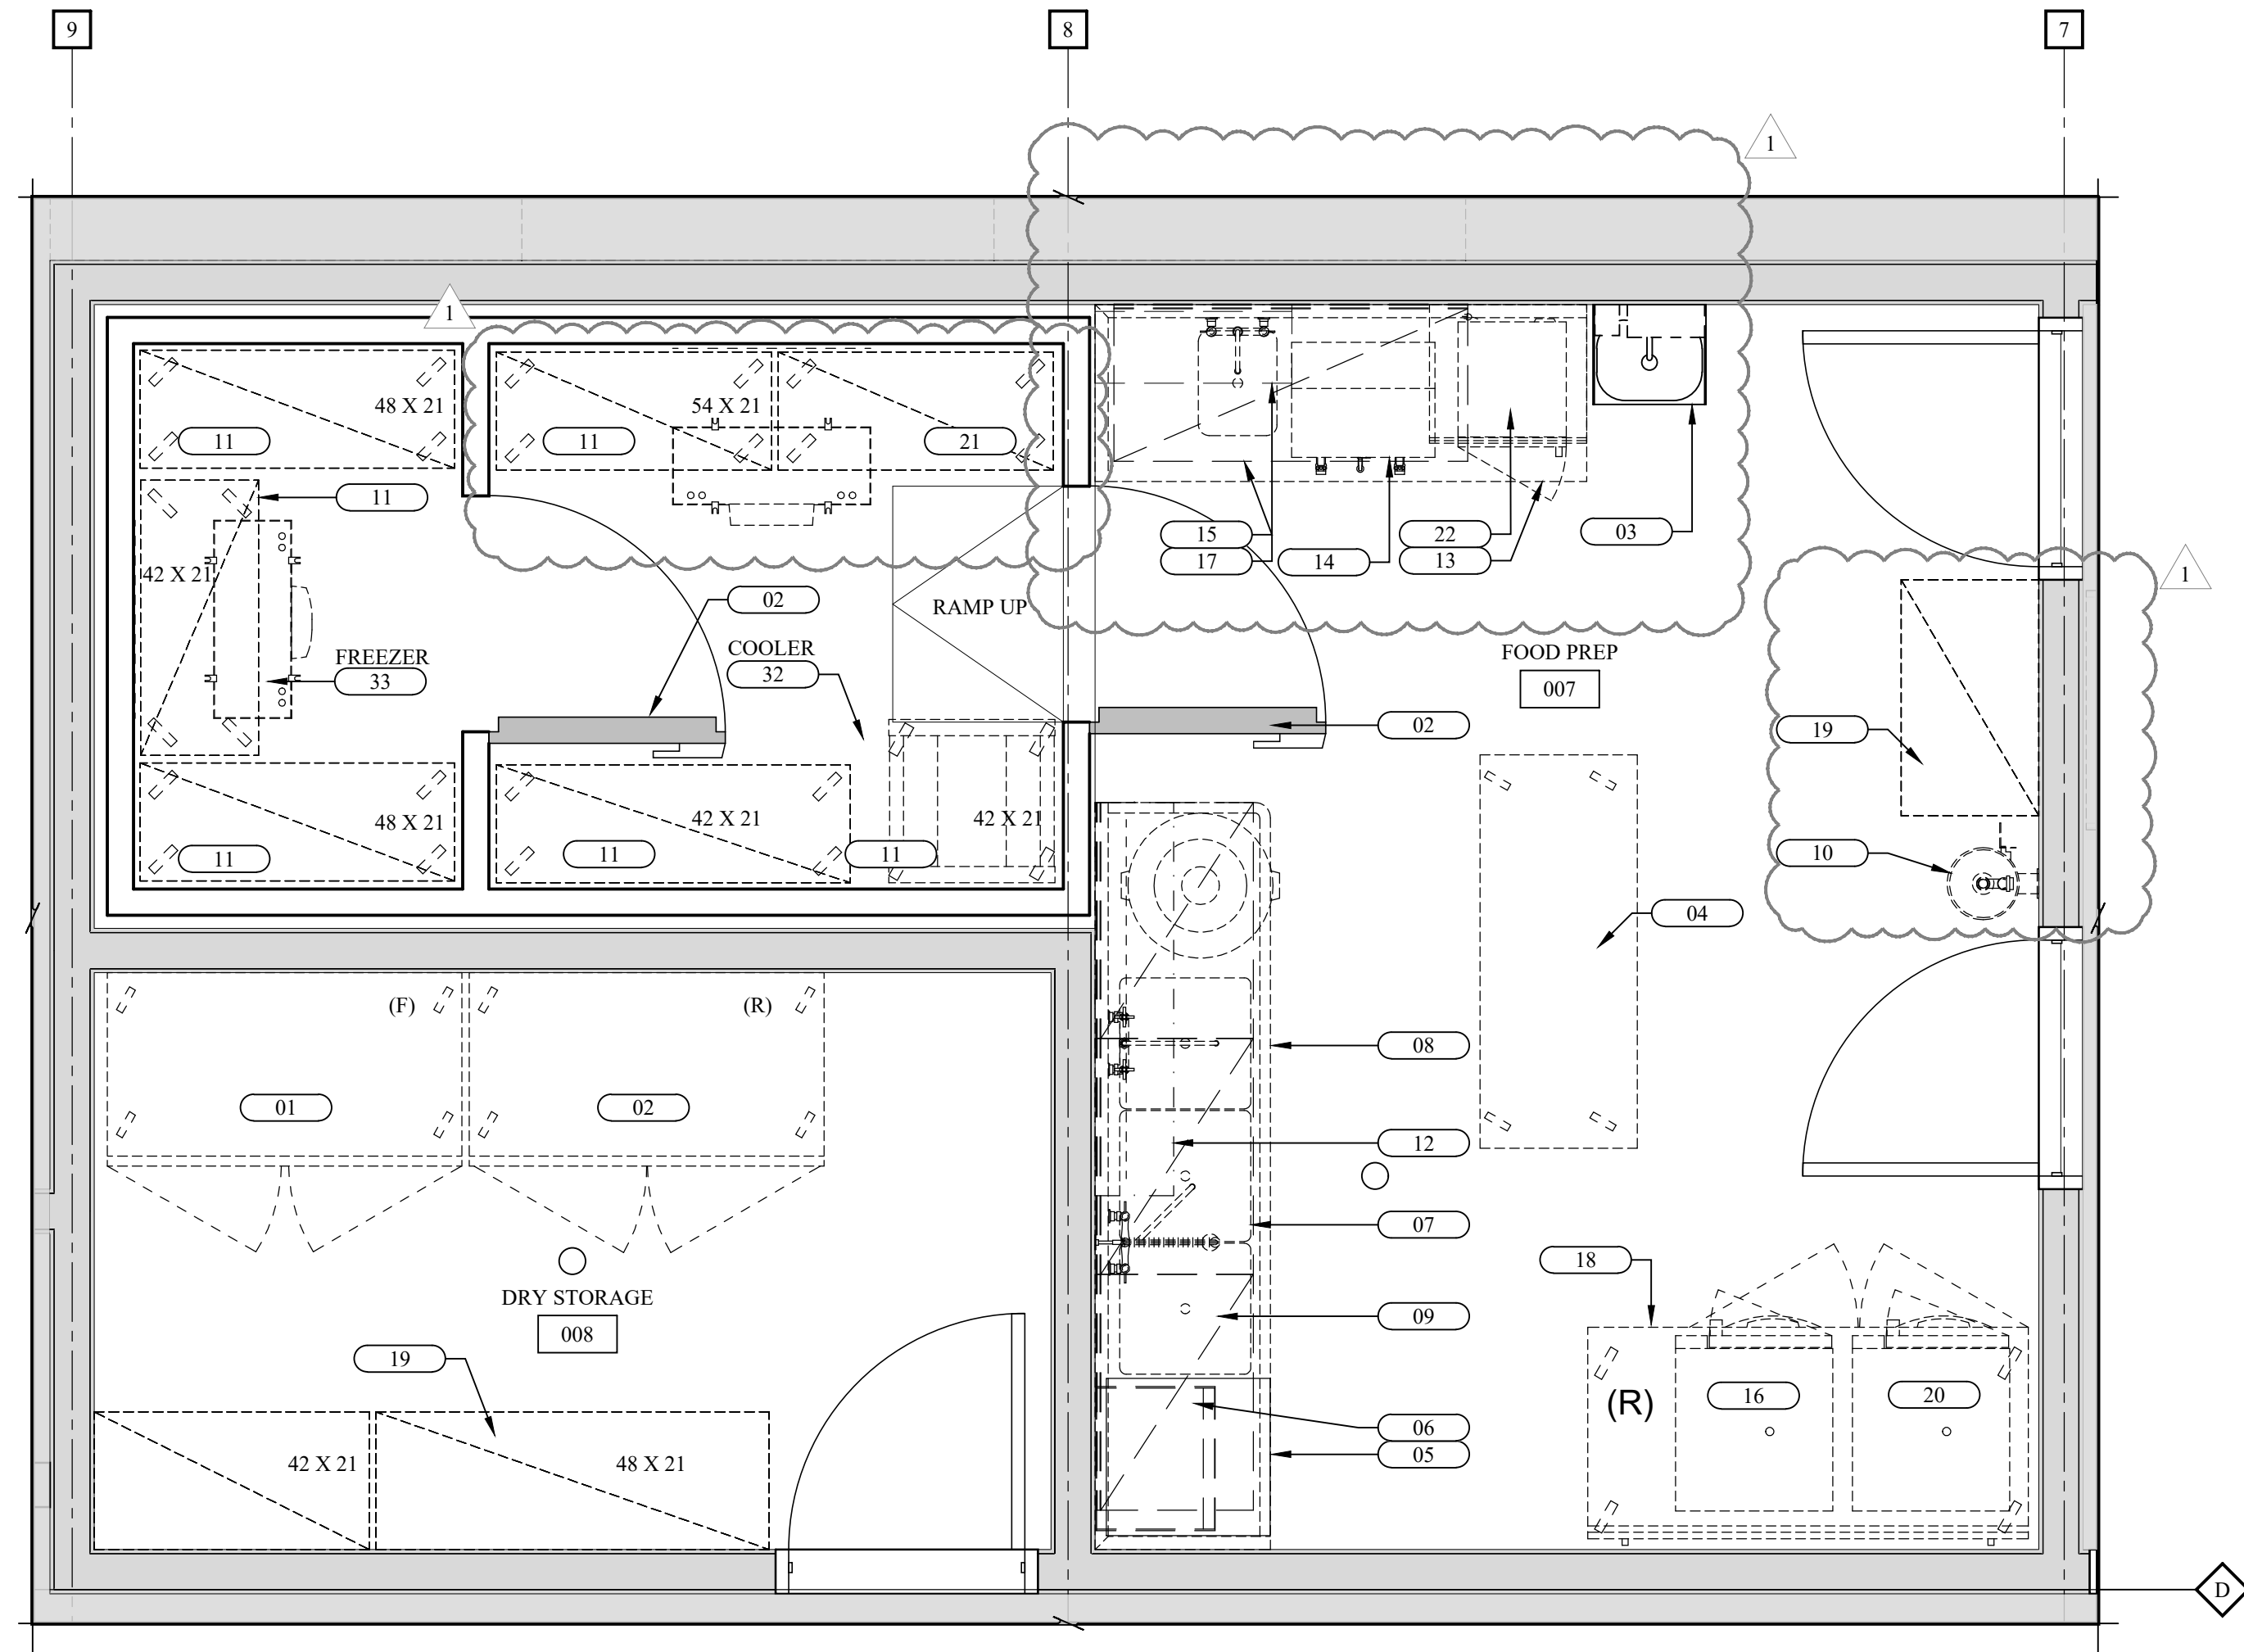

1 FOOD PREP & DRY STORAGE PLAN
1/2" = 1'-0"

EQUIPMENT SCHEDULE - WALK-IN				
ITEM	QTY	DESCRIPTION	MANUFACTURER	MODEL
02	1	WALK-IN COOLER / FREEZER ASSEMBLY	AMERICAN PANEL	CUSTOM
03	1	HAND SINK W/ SOAP AND TOWEL DISPENSER	ADVANCE TABCO	7-PS-87
04	1	MOBILE WORK TABLE	CUSTOM FABRICATED	
05	1	UNDERCOUNTER DISHMACHINE (HIGH TEMP)	CHAMPION	UH-100B
06	1	DISHTABLE RACK SHELF	ADVANCE TABCO	DT-68R-11
07	3	WALL SHELF (HIGH MOUNT)	METRO	1WD24K3/2WD24K3/2436NK3
08	1	DISH / POT WASHING SINKS	CUSTOM FABRICATED	
09	1	PREF-RINSE W/ALICET	T&S BRASS	B-2278-A17-FL
10	1	EYE WASH STATION	HAWS	7360BT-7460BT
11	6	MOBILE COOLER/FREEZER SHELVING	METRO	METROMAX Q
12	1	UTENSIL RACK W/ SHELF	ADVANCE TABCO	PS-12-60
13	1	WORKTABLE WITH SINK	CUSTOM FABRICATED	
14	1	COFFEE MAKER (OPERATOR FURNISHED)	PETCO	CBS-3125XTS
15	1	WALL SHELF (HIGH MOUNT)	METRO	1WD24K3/2436NK3
16	1	CONVECTION OVEN (VENTLESS)	MOFFAT (TURBOFAN)	E3D5H2
17	2	WALL SHELF	CUSTOM FABRICATED	
18	1	WORKTOP REFRIGERATOR	TRUE FOOD SERVICE	TWT-67-HC-SPEC3
19	4	STORAGE SHELVING	METRO	METROMAX Q
20	1	CONVECTION OVEN (VENTLESS)(OPTIONAL)	MOFFAT (TURBOFAN)	E3D5H2
21	1	SPEED RACK	CRES COR	207-UA-13A
22	1	MICROWAVE OVEN (BELOW)	AMANA	HDC12A7/BMS/024
32	1	UNIT COOLER (COOLER)	OMNITEMP	KLP106MA-SID1
33	1	UNIT COOLER (FREEZER)	OMNI	KLP106LE-S2D
EQUIPMENT SCHEDULE - DRY STORAGE				
ITEM	QTY	DESCRIPTION	MANUFACTURER	MODEL
01	1	MOBILE REACH-IN FREEZER	TRUE	T-49F-HC
02	1	REACH-IN REFRIGERATOR	TRUE	TS-49-HC
19	2	STORAGE SHELVING	METRO	METROMAX Q



3827 BILLO ROAD
ALDEN, NY, 14004
716-631-0600
ARCHITECT OF RECORD

DONALD M. EDWARD
LICENSE #: 20212
10800 ALABASTER DR.
DAVIDSON, NC 28036
donedwardarchitect@gmail.com



WARNING
IT IS A VIOLATION OF THE LAW FOR ANY
PERSON, UNLESS ACTING UNDER THE
DIRECTION OF THE ARCHITECT OR ENGINEER,
TO ALTER OR REPRODUCE THESE DRAWINGS
IN ANY WAY.

DRAWING QUESTIONS
CA@MWTUSA.COM
1-800-717-5816

ISSUED FOR :
CONSTRUCTION AND BID SET



EAGLE PASS, TX 78852
PROTOTYPE VERSION: 3.0

[illegible]

PROJECT NO.: 22-014

DATE: 06/09/23


DRAWN BY: RH/BS

CHECKED BY: AS/FS

ENLARGED
FOOD PREP
& DRY STORAGE

SHEET
A513

22-014 A513-A513.1 ENLARGED FOOD PREP & DRY STORAGE.dwg

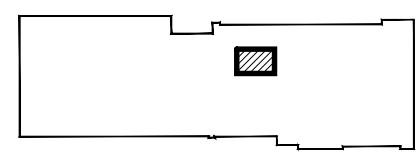

KEY PLAN
N.T.S.

IMPORTANT NOTICE TO ALL CONTRACTORS AND OR SUBCONTRACTORS: (COMPLETE BUILDING SYSTEMS AND OR INSTALLATIONS)

IF YOU AGREE TO PROVIDE ANY PORTION OF WORK NOTED TO COMPLETE THIS PROJECT YOU ARE AGREEING TO THE FOLLOWING:

THE CONTRACTOR AND/OR SUBCONTRACTOR SHALL COMPLETE THE PROJECT IN ACCORDANCE WITH THE TERMS OF THE WORK ORDER AND/OR CONTRACT FOR THIS PROJECT.

IF YOU AGREE TO PROVIDE A COMPLETE DESIGN-BUILD SOLUTION BASED ON THE ARCHITECT'S INTENDED DESIGN FOR THIS PROJECT:

THE CONTRACTOR AND/OR SUBCONTRACTOR SHALL COMPLETE THE PROJECT IN ACCORDANCE WITH THE TERMS OF THE WORK ORDER AND/OR CONTRACT FOR THIS PROJECT.

IF YOU AGREE TO PROVIDE A PORTION OF THE PROJECT, THE CONTRACTOR AND/OR SUBCONTRACTOR SHALL PROVIDE A COMPLETE DESIGN AND WARRANTY SYSTEM OR INSTALLATION THAT DOES NOT REQUIRE ANOTHER CONTRACTOR OR PROVIDER TO COMPLETE YOUR SCOPE OF WORK.

YOU MAY NOT HAVE INCLUDED ANY INFORMATION REFERENCED WITHIN ANY ARCHITECTURAL, STRUCTURAL, MECHANICAL, ELECTRICAL AND/OR PLUMBING DRAWINGS, ALSO NOTE THESE DRAWINGS ARE SCHEMATIC AND ARE INTENDED TO SHOW ONLY BASIC CONCEPTS AND GENERAL INFORMATION. THE COMPLETION OF ANY AND ALL WORK SHALL BE THE RESPONSIBILITY OF THE CONTRACTOR AND/OR SUBCONTRACTOR.

YOUR DESIGN, ITEMS AND/OR TASKS (I.E. FIRE ALARM, DRAFT STOPS, PATENTERS, ANCHORS, EMBLEMENTS, DOWNS, DEBRIS CLEAN UP, ETC.) ARE YOUR RESPONSIBILITY. ANY WORK NOT COMPLETED IN A TIMELY MANNER, OR INCOMPLETE WORK WILL BE RELEGED BACK TO THE CONTRACTOR AND/OR SUBCONTRACTOR, AT THE OWNERS RISK.