
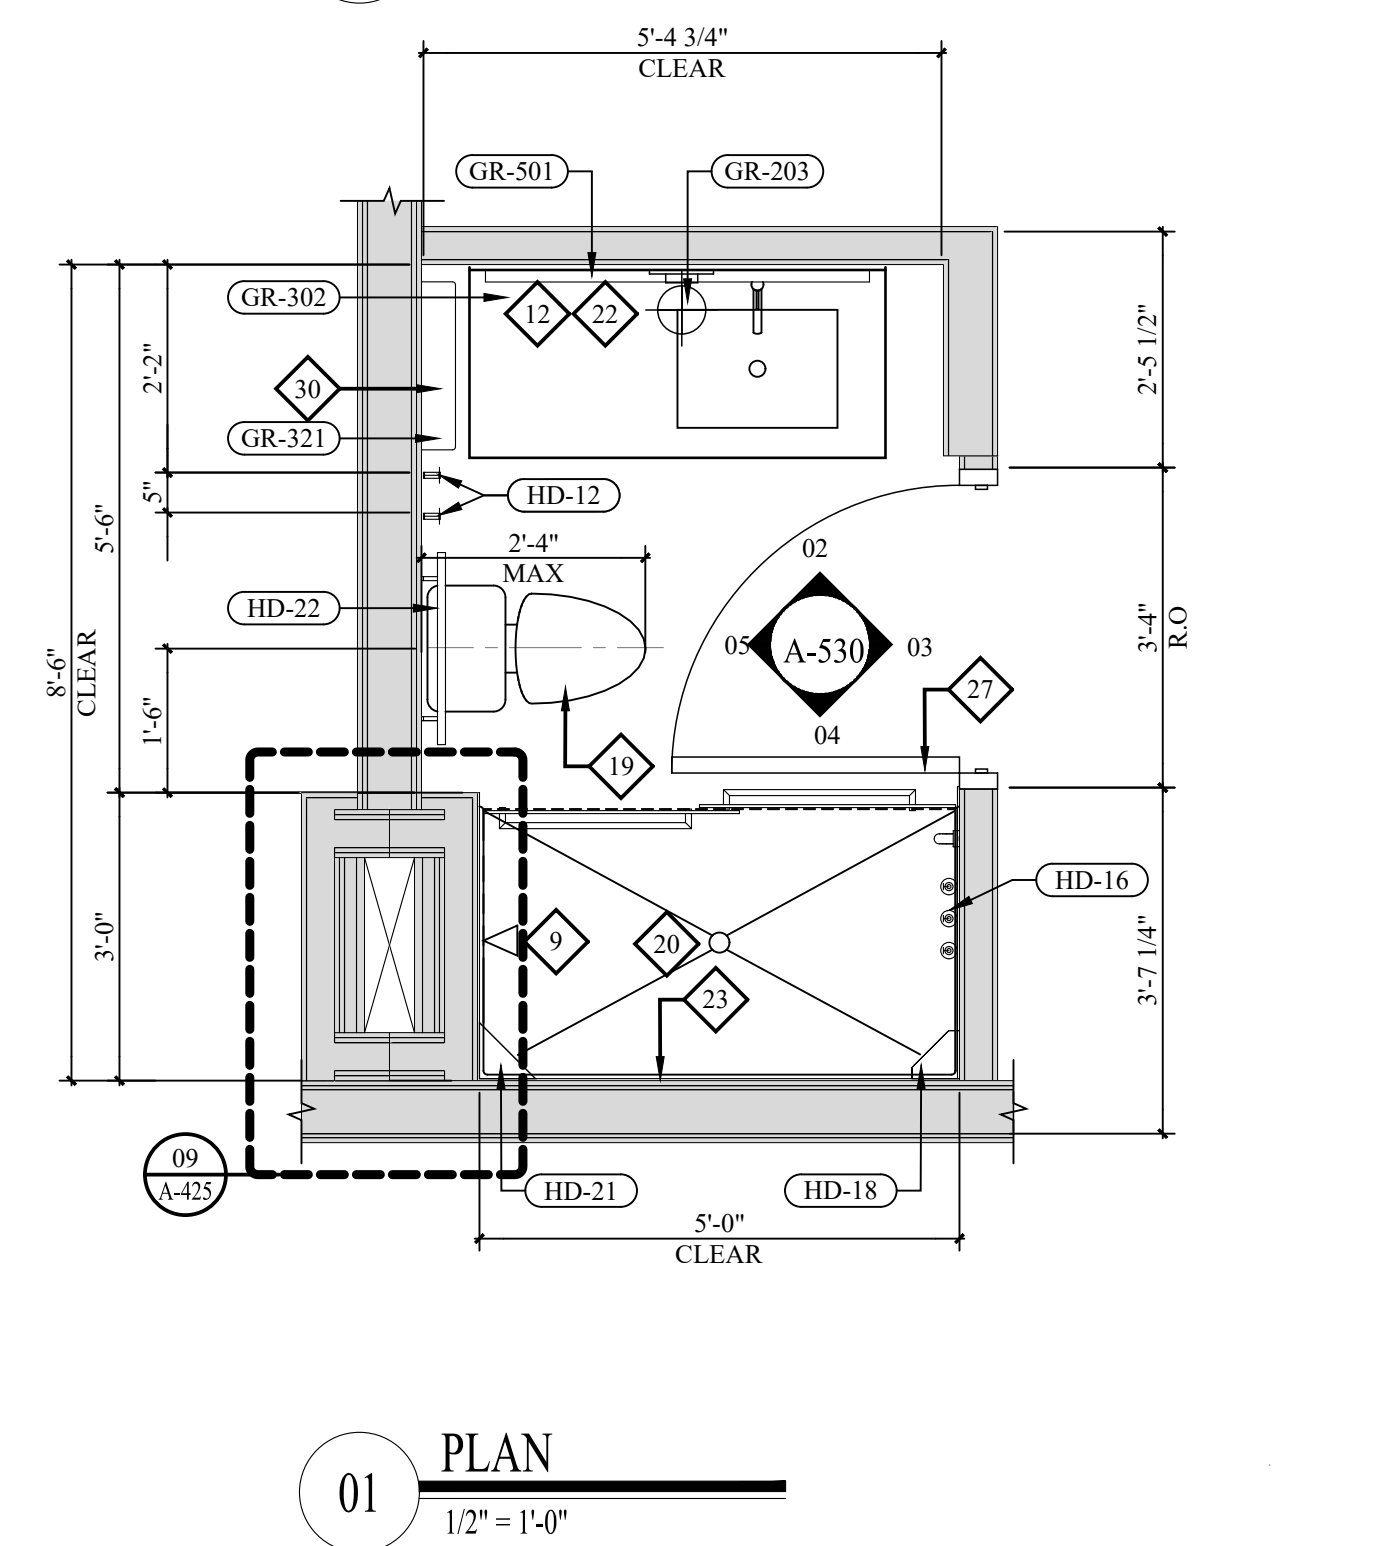
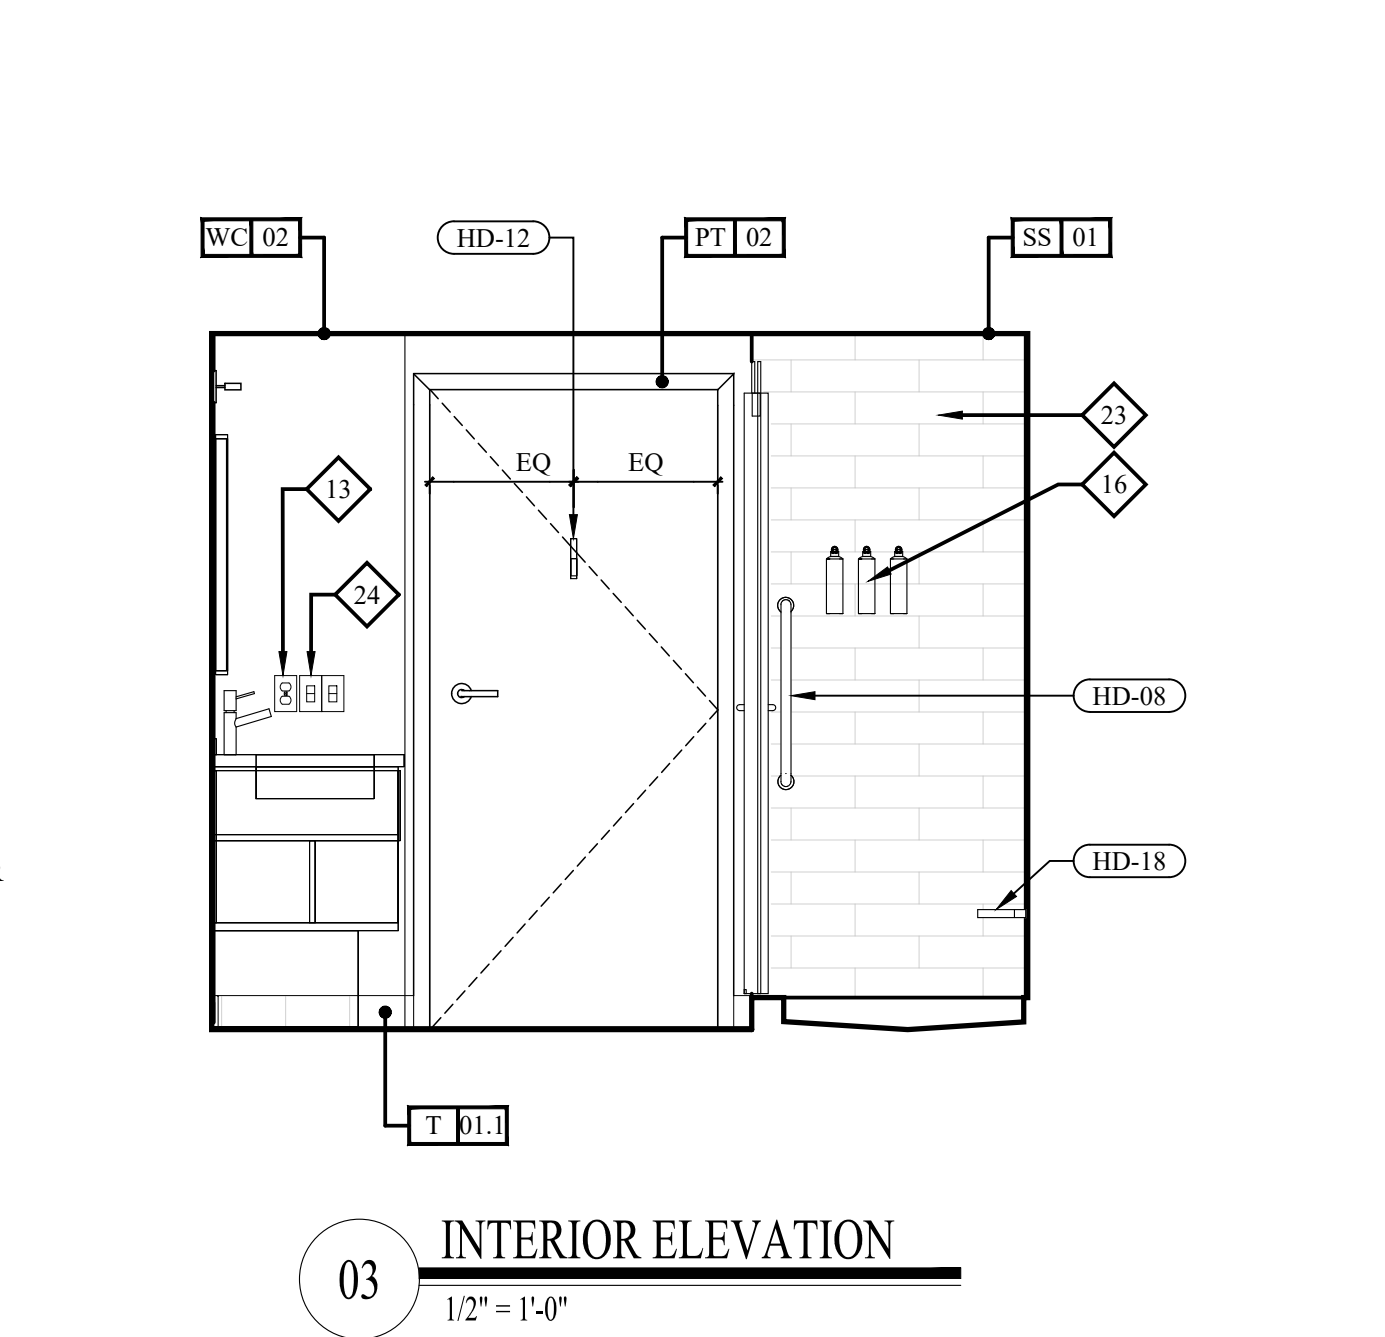
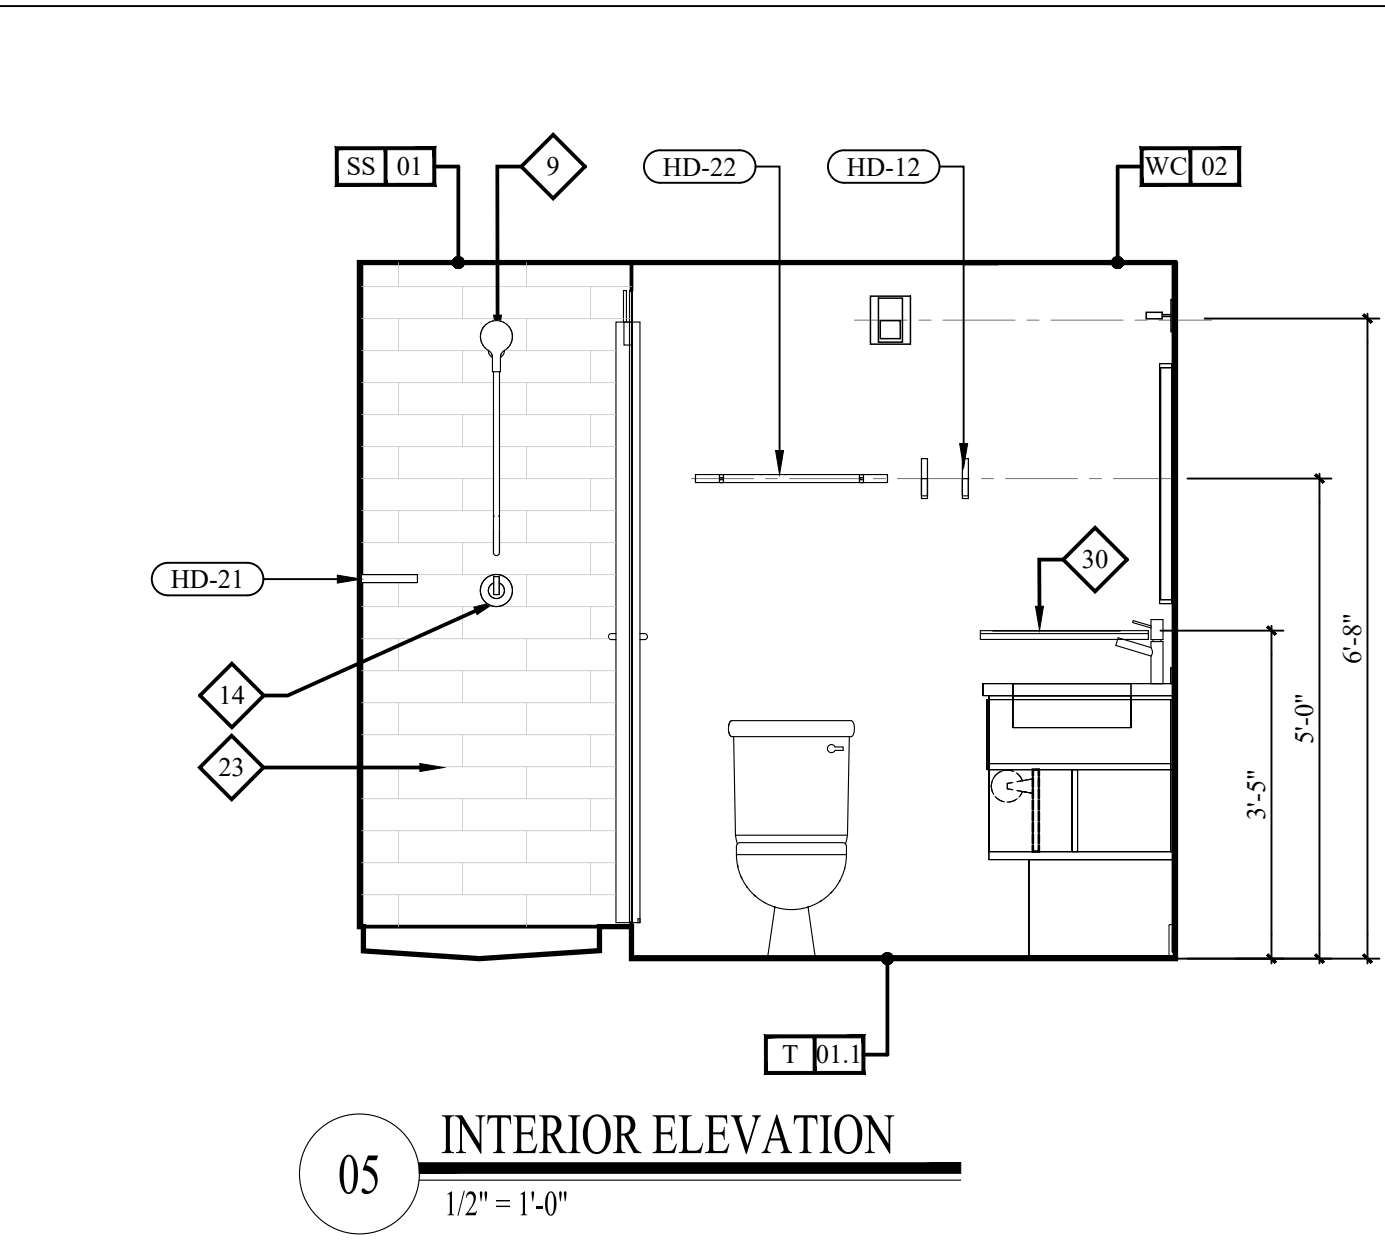
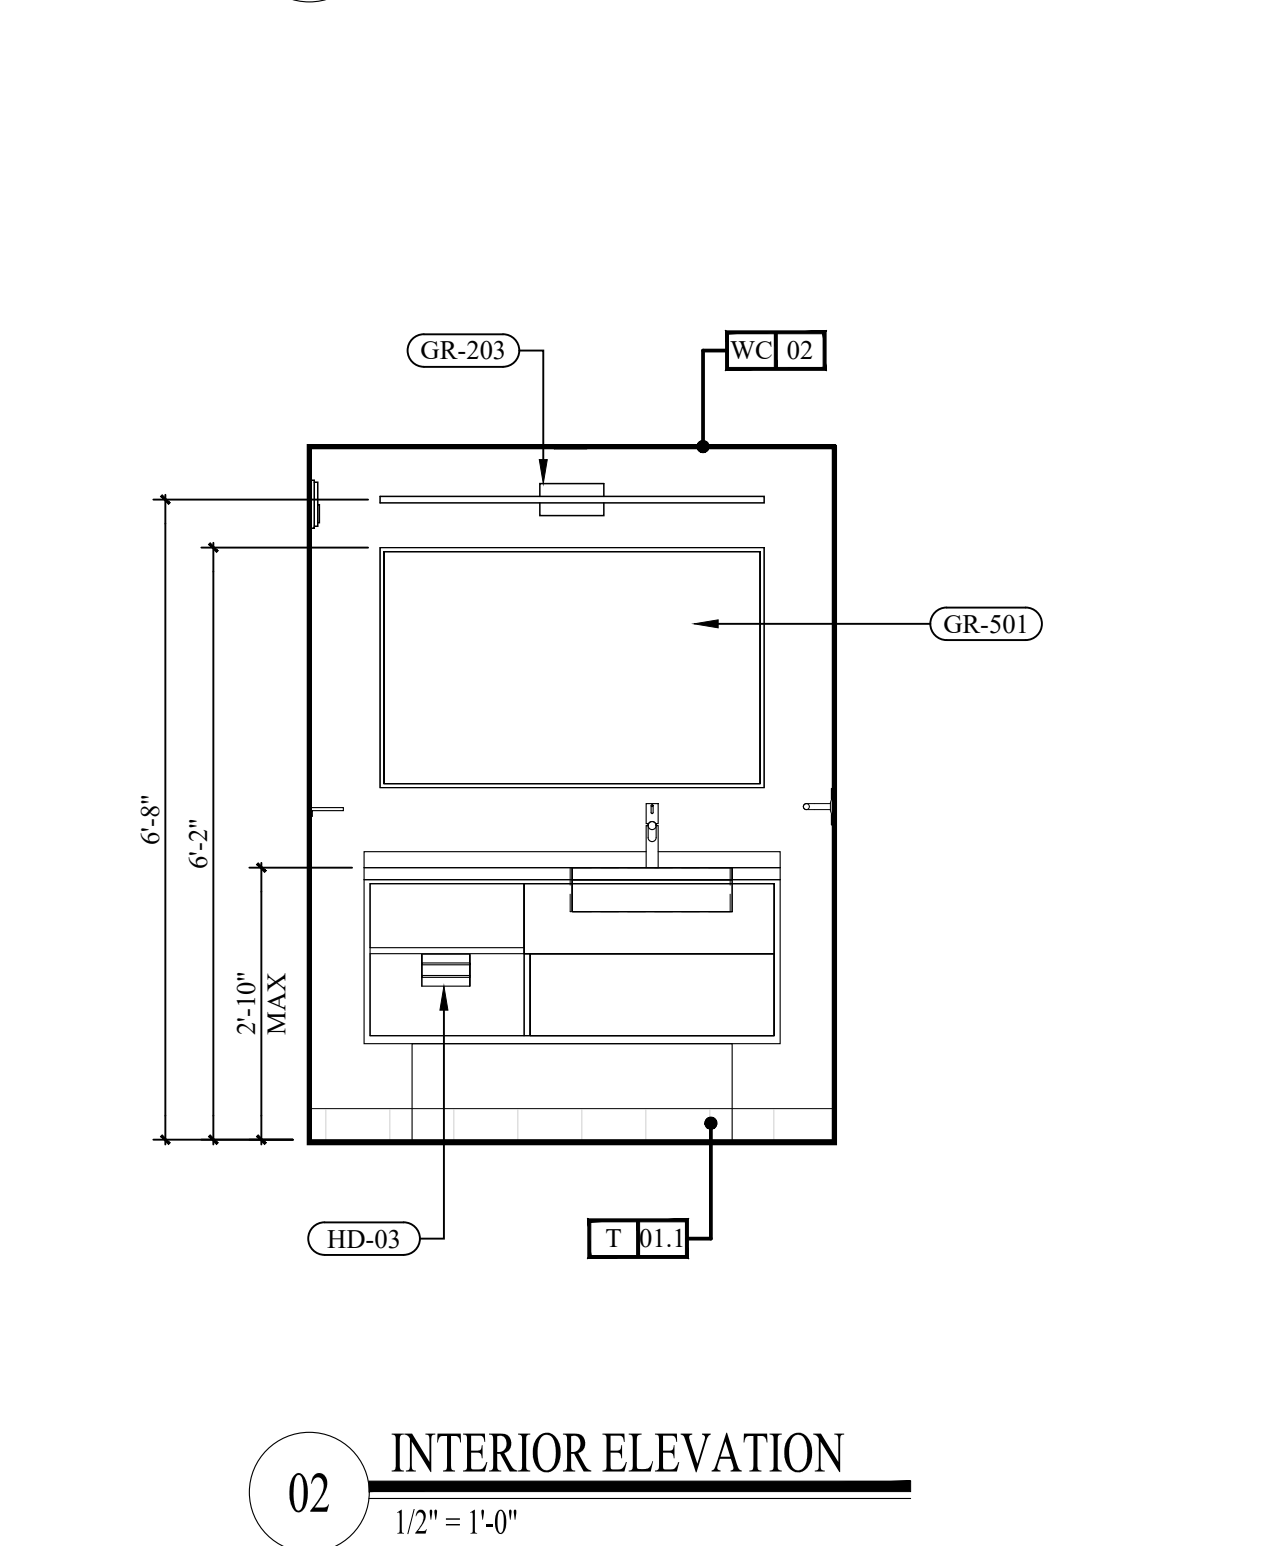
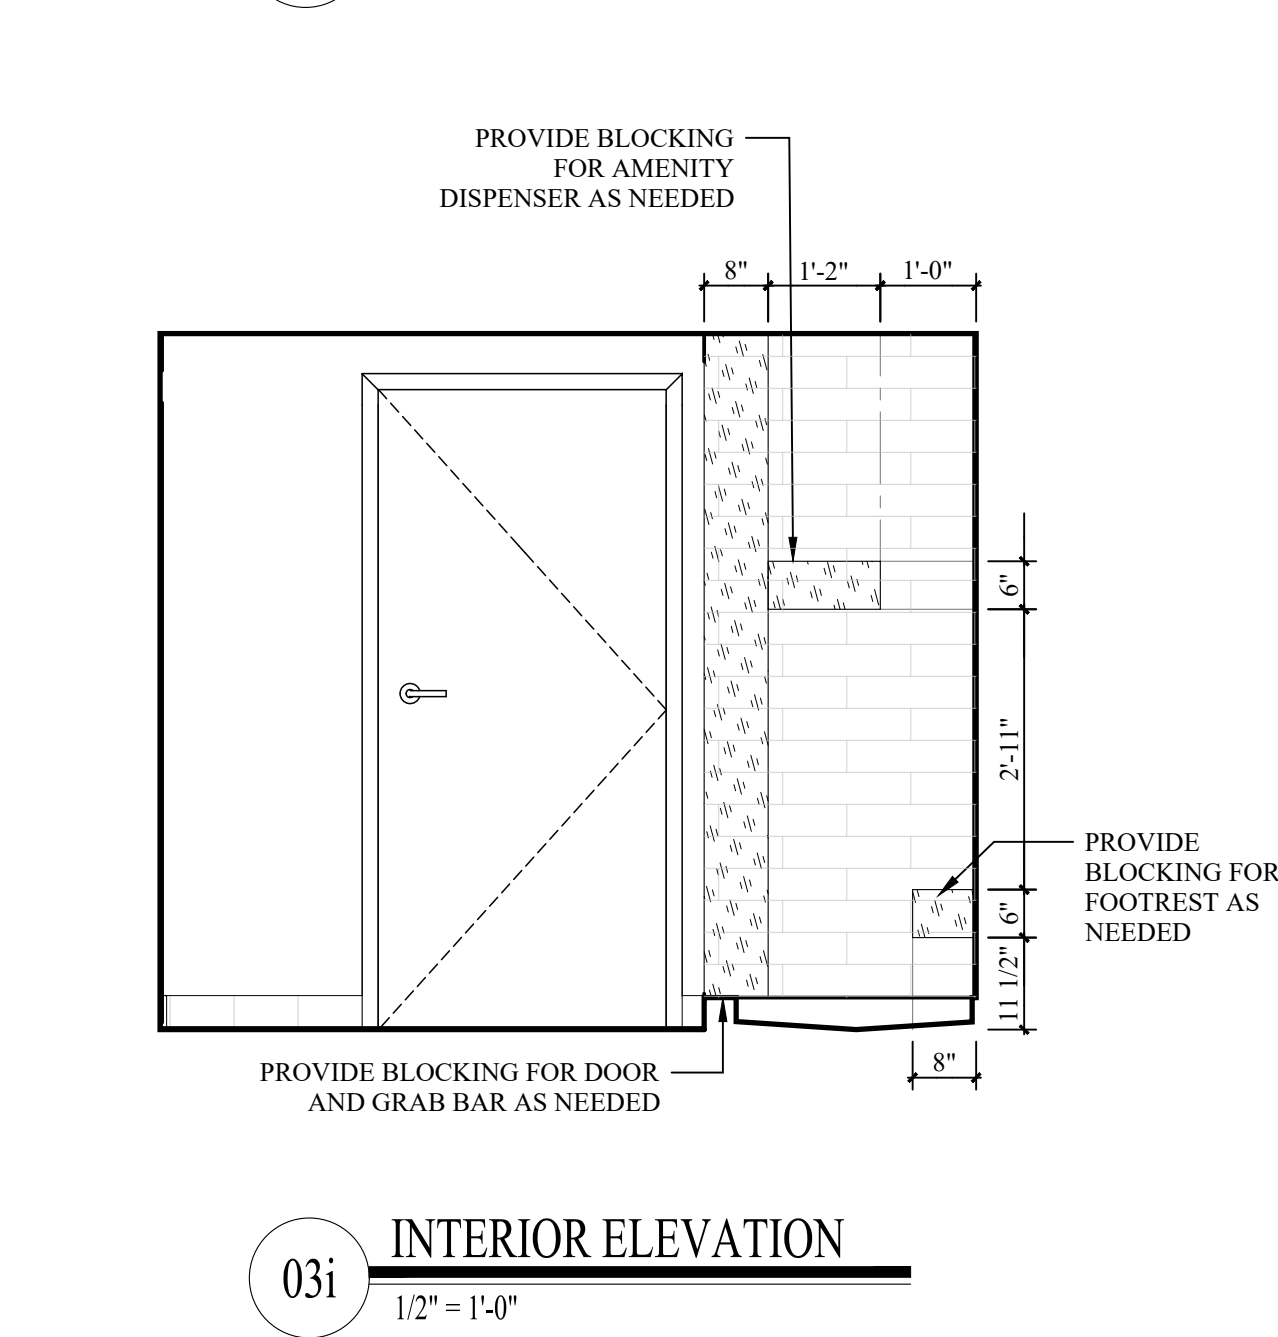
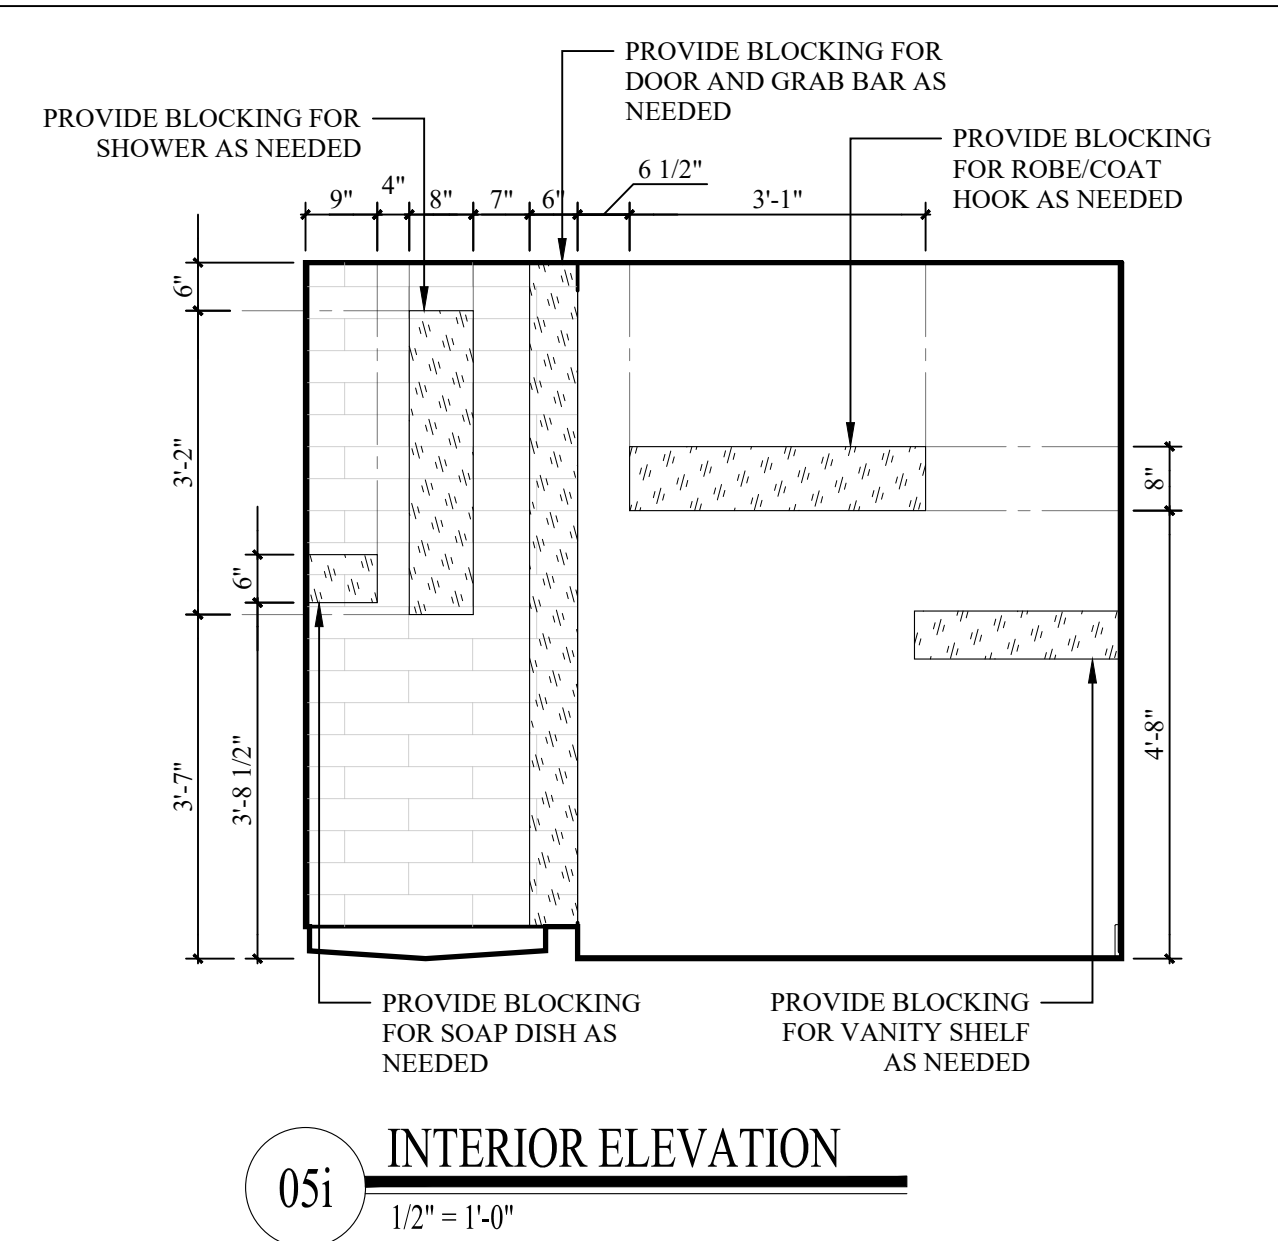
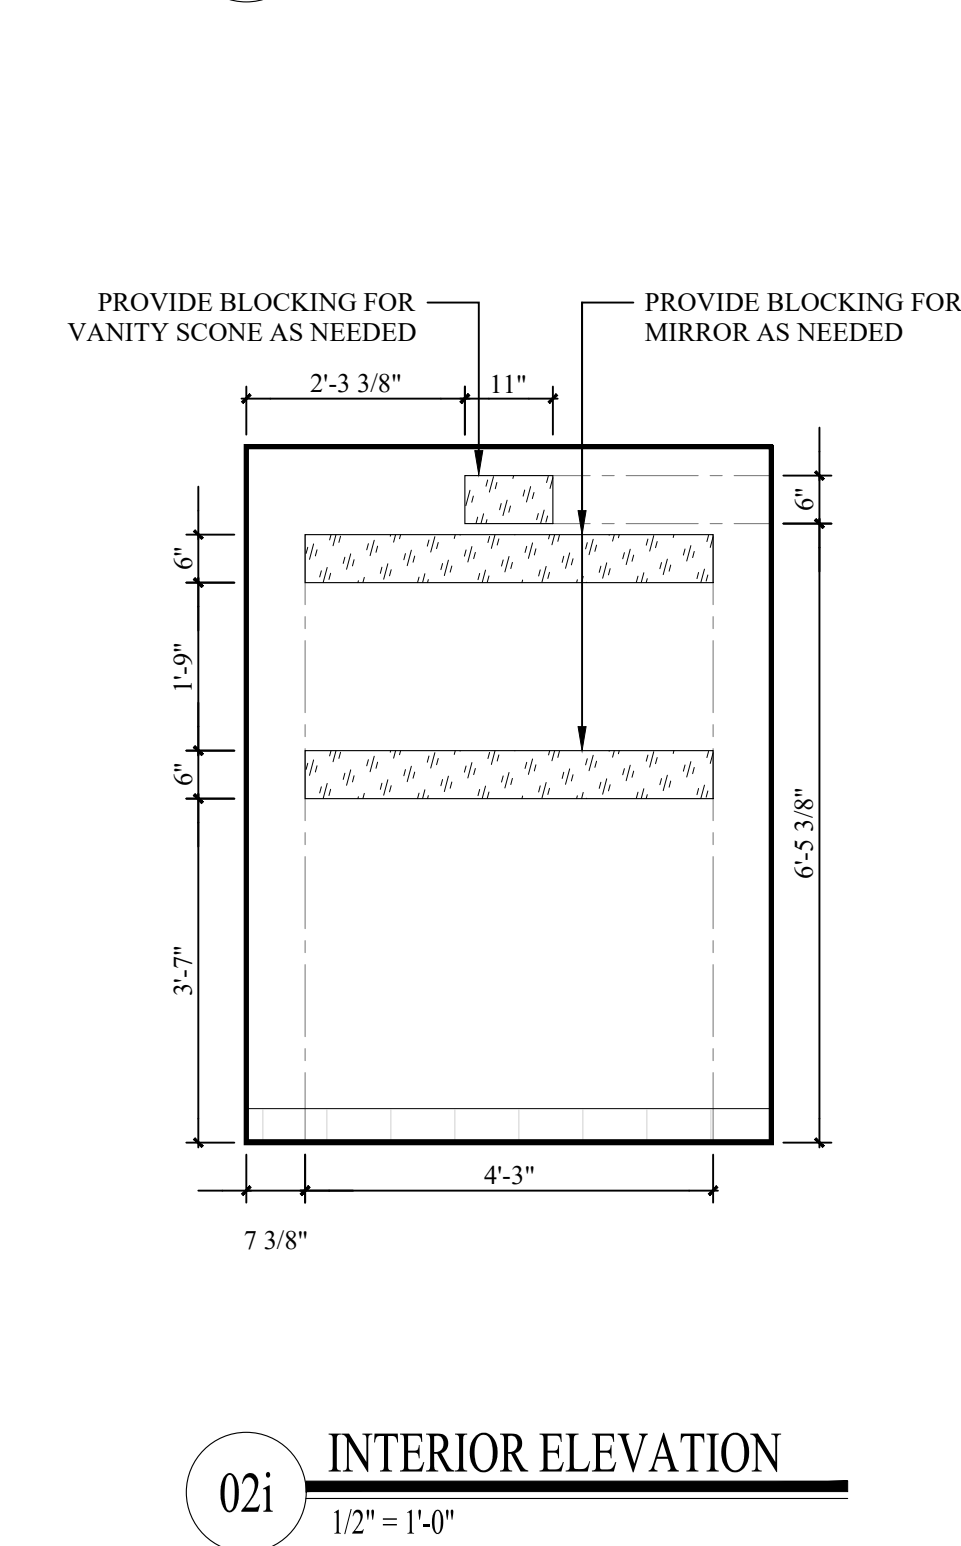


	BATHROOM KEYED NOTES :	GENERAL NOTES - GUESTROOMS	FURNISHINGS LEGEND:
	WALL MOUNTED GRAB BARS W/ REQUIRED CLEARANCES - 12" ABOVE AND 1-1/2" BELOW. REFER TO ACCESSIBILITY STANDARDS & HADG.	A. REFER TO FF&E PACKAGE FOR FURNITURE, BUILT-IN MILLWORK & FINISH SPECS	GR-100 OTTOMAN
	ACCESSIBLE VANITY UNIT, REFER TO FURNITURE DWGS.	B. SMOKE DETECTORS, SPRINKLERS, AND OTHER EMERGENCY DEVICES TO BE LOCATED PER LOCAL CODE- INDICATED FOR DESIGN INTENT ONLY	GR-101 SLEEPER SOFA
	ACCESSIBLE REMOVABLE TUB/SHOWER SEAT. SHOWER SEAT IS WALL MOUNTED. REFER TO ACCESSIBILITY STANDARDS AND HADG FOR REQUIREMENTS	C. PROVIDE EMERGENCY LIGHTING PER LOCAL CODE	GR-102 DINING CHAIR
	CLEAR AREA OF SINK/VANITY MUST BE ACCESSIBLE	D. A F.F. WALL RECEPTACLES/DATA PORTS TO E MOUNTED @ 12" TYPICAL U.N.O - REFER ALSO TO HADG	GR-103 TASK CHAIR
	SHOWER HEAD	E. REFER TO HOME 2 SUITES BY HILTON STANDARDS MANUAL FOR ADDITIONAL GUESTROOM, GUESTROOM BATH, GUESTROOM KITCHEN & INDOOR POOL REQ'S	GR-200 SIDE TABLE LAMP
	SHOWER DIVERTER VALVE	F. ALL CONTROLS FOR USE BY GUESTS MUST BE MOUNTED @ B/T 15" A.F.F. & 48" A.F.F. & PROVIDE A 30"X48" CLEAR FLOOR AREA IN COMPLIANCE W/ ACCESSIBLE STANDARDS. OPERABLE CONTROLS LOCATED OVER AN OBSTRUCTION DEEPER THAN 10" MUST BE MOUNTED NO HIGHER THAN 46" A.F.F. -ACCESSIBLE CONTROLS MUST NOT REQUIRE TIGHT GRASPING, PINCHING OR TWISTING OF THE WRIST. ACCESSIBLE CONTROLS SHALL COMPLY W/ THE HADG	GR-201 DESK LAMP
	HAND SHOWER AND SIDE BAR. HAND-HELD SHOWER UNIT REQUIRED TO HAVE ON/OFF CONTROL WITH NON-POSITIVE SHUT OFF.	G. IN ACCESSIBLE ROOMS AT LEAST ONE OUTLET & DATA CONNECTION FOR USE BY GUEST MUST BE MOUNTED B/T 15" & 48" A.F.F. AND PROVIDE A CLEAR FLOOR AREA IN COMPLIANCE W/ ACCESSIBLE STANDARDS. SEE HADG FOR FURTHER REQ'S.	GR-202 NIGHTSTAND SCONE
	VANITY MIRROR AND LIGHT FIXTURE	H. OBJECTS MOUNTED W/IN THE CIRCULATION PATH IN ACCESSIBLE ROOMS B/T 27" & 80" A.F.F. SHALL NOT PROTRUDE FARTHER THAN 4" FROM WALL REFER TO HADG FOR FURTHER REQ'S	GR-203 VANITY SCONE
	GFCI OUTLET	I. FOR ALL ITEMS MOUNTED TO THE WALL (SHELVES, FF&E, MIRRORS, ART, ETC.; PROVIDE BLOCKING AS REQUIRED	GR-204 SCONE @WALL HOOK
	ON/OFF - PRESSURE BALANCING VALVE		GR-205 FLOOR LAMP
	TOILET		GR-206 TABLE LAMP
	FLOOR DRAIN LOCATION - MAINTAIN ACCESSIBLE COMPLIANT SLOPES TO DRAIN		GR-207 @ACCESSIBLE WORKING WALL NIGHTSTAND SCONE
	LEVER REQUIRED ON THE SIDE OF TANK OPPOSITE INSIDE CORNER OF WALL		GR-208 @QUEEN QUEEN CENTER NIGHTSTAND SCONE
	FRAMING SUBCONTRACTOR TO PROVIDE 3/4" F.R.T. PLYWOOD BLOCKING TO RECEIVE ITEM INDICATED - EXTEND FULL LENGTH OF OBJECT		GR-300 @QUEEN QUEEN SIDE QUEEN HEADBOARD
	SHOWER SURROUND		GR-301 KING HEADBOARD
	LED NIGHT LIGHT INTEGRATED WITH EITHER LIGHT SWITCH OR OUTLET		GR-302 VANITY
	SOAP DISPENSERS		GR-303 @GUEST BATH (LEFT&RIGHT) ACCESSIBLE VANITY
	DOOR STOP HARDWARE REQUIRED TO KEEP HARDWARE AT BACK OF DOOR FROM HITTING GLASS WHEN FULLY AJAR		GR-304 -316 @GUEST BATH WORKING WALL DINING TABLE
	BI-PASS SLIDING GLASS DOOR, BRUSHED ALUMINUM FINISH, CLEAR GLASS, WITH 24" BAR PULL HARDWARE		GR-317 @ONE BEDROOM SUITE SOFA TABLE @SOFA
	PROVIDE HINGE STOP AT DOOR		GR-318 NIGHTSTAND @RIGHT
	VANITY SHELF		GR-319 DECORATIVE SHELVES ABOVE DESK

BATHROOM ACCESSORIES NOTES :	
HD-01	TOILET PAPER ROLL HOLDER
HD-02	SINGLE TOILET PAPER HOLDER
HD-03	TOILET TISSUE DISPENSER
HD-04	TOWEL HOOK
HD-05 & HD-5.1	SHOWER ROD BOWED & STRAIGHT
HD-06	GRAB BAR ADA
HD-08	GRAB BAR ADA 24" VERTICAL MOUNT
HD-09	GRAB BAR ADA 24" HORIZONTAL MOUNT
HD-10	GRAB BAR ADA 22" HORIZONTAL MOUNT
HD-11	GRAB BAR ADA 36" HORIZONTAL MOUNT
HD-12	ROBE/COAT HOOK
HD-13	AUTOMATIC PAPER TOWEL DISPENSER SURFACE MOUNTED
HD-14	FOLDING RECTAGULAR SHOWER SEAT SURFACE MOUNTED
HD-15	SOAP DISPENSER SURFACE MOUNTED
HD-16	SHOWER SOAP DISPENSER SURFACE MOUNTED
HD-17	PAPER TOWEL/SOAP DISPENSER RECESSED
HD-18	SHOWER FOOTREST SURFACE MOUNTED
HD-19	RECESSED WASTE RECEPTACLE PUBLIC & POOL RESTROOM
HD-20	GRAB BAR ADA 12" HORIZONTAL MOUNT
HD-21	SOAP DISH SURFACE MOUNTED
HD-22	TOWEL BAR 24"

901	REFRIGERATOR
902	DISHWASHER
903	TELEVISION
904	CLOCK/RADIO
905	TELEPHONE
906	TUB SHOWER CURTAIN
907	SHOWER CURTAIN

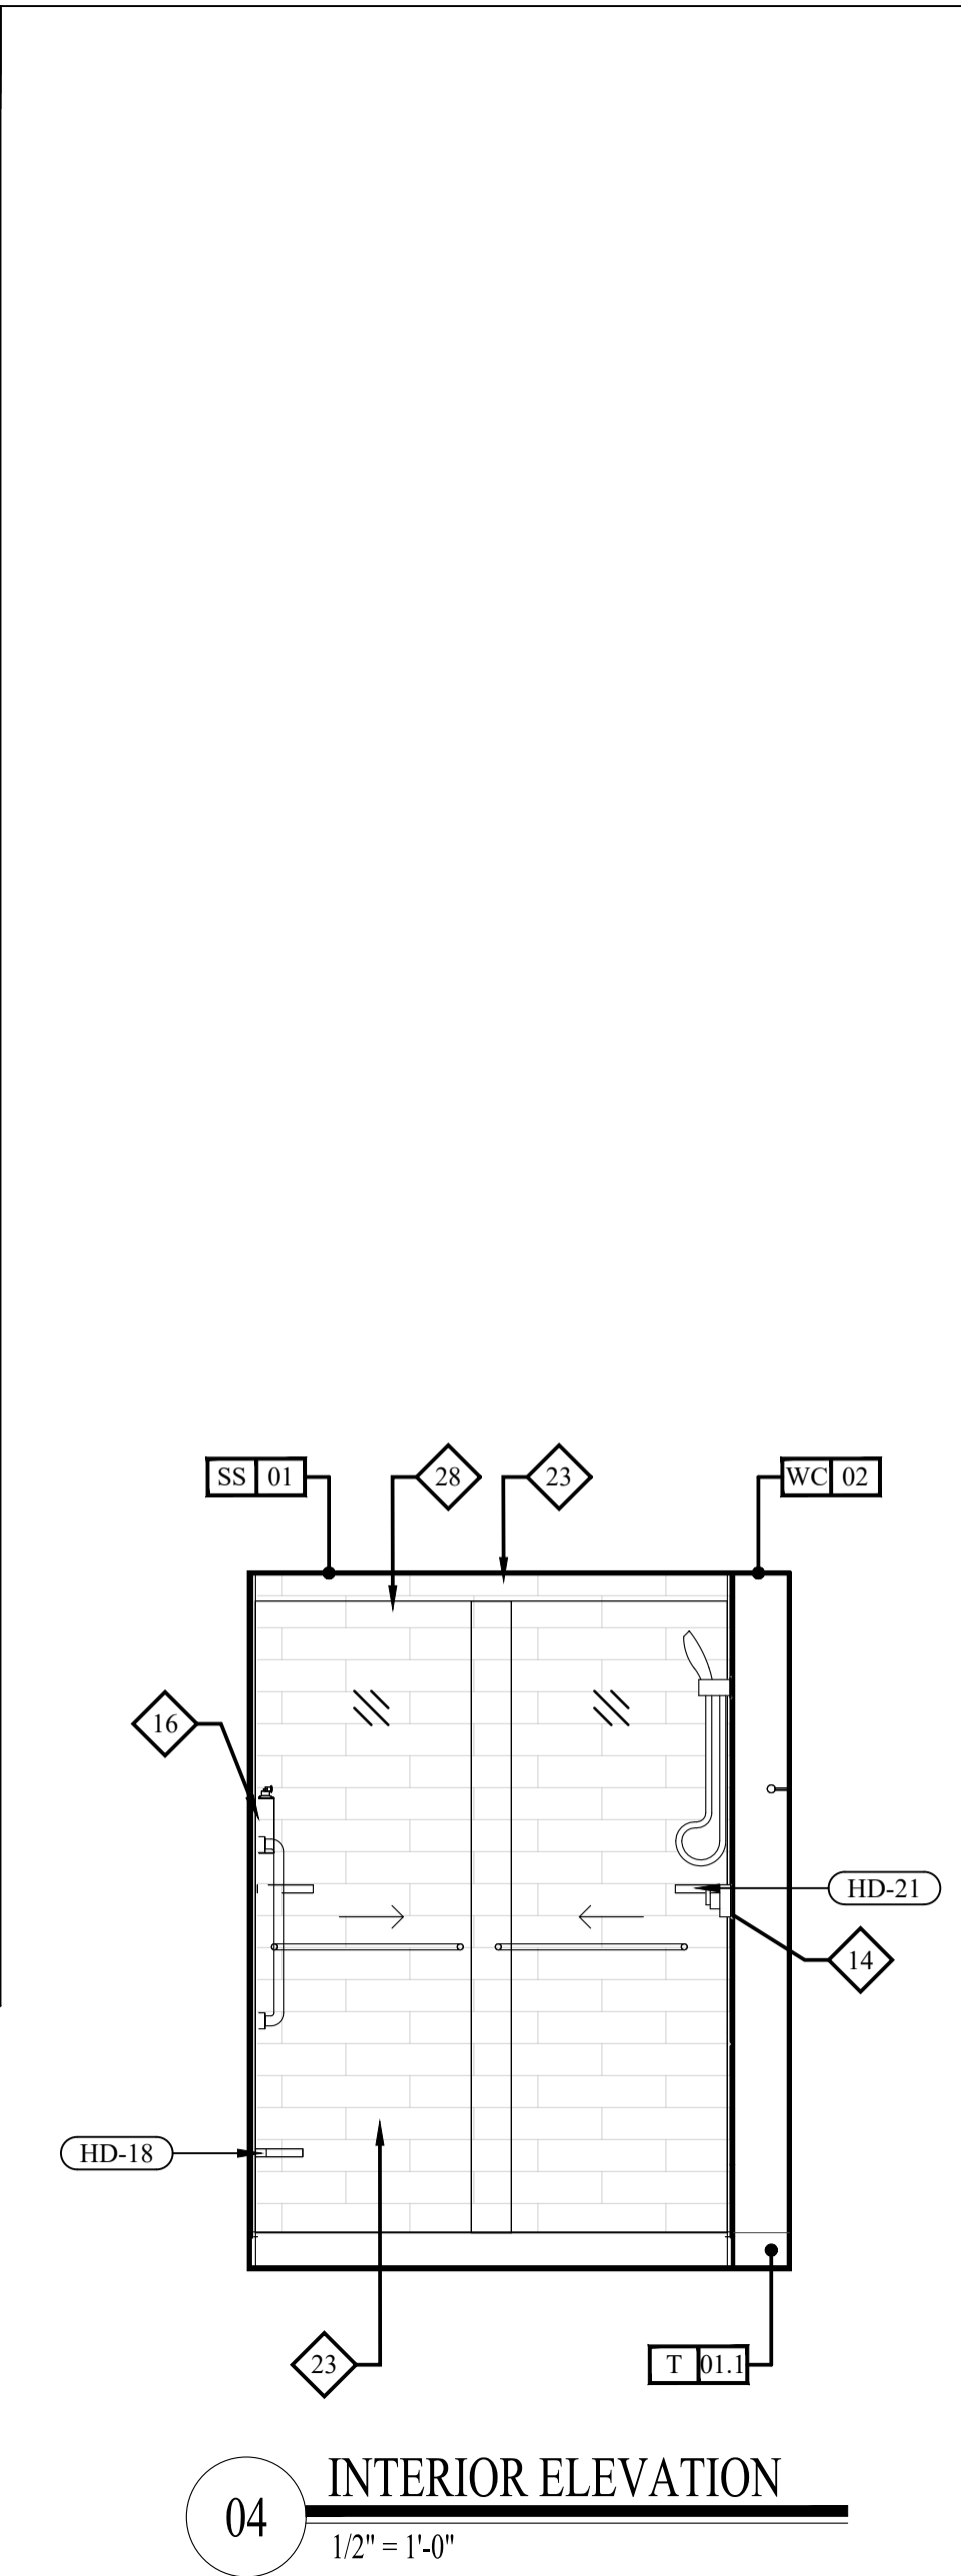

3827 BILLO ROAD
ALDEN, NY, 14004
716-631-0600
ARCHITECT OF RECORD

DONALD M. EDWARD
LICENSE #: 20212
10800 ALABASTER DR.
DAVIDSON, NC 28036
donedwardarchitect@gmail.com

08/09/2024

WARNING
IT IS A VIOLATION OF THE LAW FOR ANY PERSON, UNLESS ACTING UNDER THE DIRECTION OF THE ARCHITECT OR ENGINEER, TO ALTER OR REPRODUCE THESE DRAWINGS IN ANY WAY.

DRAWING QUESTIONS
CA@MWTUSA.COM
1-800-717-5816

ISSUED FOR :
CONSTRUCTION AND BID SET

HOME2
SUITES BY HILTON

EAGLE PASS, TX 78852
PROTOTYPE VERSION: 3.0

REVISIONS

NO.	DESCRIPTION	DATE	BY
1	FF&E FRANCHISE UPDATE	-	-
2	PER STRUCTURAL UPDATE	-	-
3	REVISED PER CITY COMMENT	-	-
4	REVISED	08/09/24	-

PROJECT NO.: 22-014

DATE: 08/09/24

DRAWN BY: BS

CHKD. BY: AS

ENL. BATHROOM
- KING STD., STD. CONN.,
QQ STD., STD. CONN.
QQ WIDE & QQ EXT.

SHEET
A530

22-014 A530 ENLARGE UNIT BATHROOM.dwg

IMPORTANT NOTICE TO ALL CONTRACTORS AND OR SUBCONTRACTORS: (COMPLETE BUILDING SYSTEMS AND OR INSTALLATIONS)

IF AWARDED A CONTRACT FOR ANY PORTION OF WORK NEEDED TO COMPLETE THIS PROJECT YOU ARE AGREEING TO THE FOLLOWING TERMS:

- YOU ARE A QUALIFIED CONTRACTOR AND OR SUBCONTRACTOR SPECIFICALLY IN PROVIDING A COMPLETE TURNKEY SERVICE IN YOUR TRADE OR PROFESSION FOR THE TYPE OF WORK AND SCOPE FOR THIS PROJECT.
- YOU AGREE TO PROVIDE A COMPLETE DESIGN BUILD SOLUTION BASED ON THE ARCHITECTS INTENDED DESIGN FOR THIS PROJECT.
- YOUR BID INCLUDED ALL THE STEPS, PROCESSES, MATERIALS, PRODUCTS, GOVERNING PERMITS AND APPROVALS NECESSARY TO PROVIDE A COMPLETED AND WARRANTED SYSTEM OR INSTALLATION THAT DOES NOT REQUIRE ANOTHER CONTRACTOR OR PRODUCT TO COMPLETE YOUR SCOPE OF WORK.
- YOUR BID MUST HAVE INCLUDED ANY DESIGN INFORMATION REFERENCED WITHIN ANY CIVIL, ARCHITECTURAL, STRUCTURAL, MECHANICAL, ELECTRICAL AND OR PLUMBING DRAWINGS. ALSO NOTE THESE DRAWINGS ARE SCHEMATIC AND ARE INTENDED TO SHOW ONLY BASIC CONCEPTS AND GENERAL INFORMATION. THE COMPLETION OF YOUR WORK MAY INCLUDE OTHER STEPS, PROCESSES, MATERIALS, PRODUCTS, LABOR, GOVERNING PERMITS AND OR APPROVALS NECESSARY TO PROVIDE A COMPLETE SYSTEM INSTALLATION WHETHER SUGGESTED ON THE DRAWINGS OR NOT.
- AS AN EXAMPLE, ITEMS AND OR TASKS LIKE: FIRE CAULK, DRAFT STOPS, FASTENERS, ANCHORS, EMBEDMENTS, DUMPSTERS, DEBRIS CLEAN UP, ETC. ARE YOUR RESPONSIBILITY. ANY WORK NOT COMPLETED IN A TIMELY MANNER, OR INCOMPLETE WORK WILL BE BILLED BACK TO THE CONTRACTOR AND OR SUBCONTRACTOR, AT THE OWNERS' DISCRETION.