




KEY NOTES: DESIGN DEVELOPMENT	FURNISHINGS LEGEND:	POWER & SIGNAL LEGEND	
PTAC UNIT IN BATHROOM LOCATIONS ONLY. LIGHT SWITCH EQUIPPED WITH NIGHTLIGHT. MOUNTED SO TOP OF SWITCH IS 48" MAX A.F.F. BLACK OUT ROLLER SHADE TO EXTEND 6" BEYOND WINDOW OPENING. SHEER ROLLER SHADE TO BE MOUNTED INSIDE WINDOW OPENING. GR-400 IS MANUAL. GR-401 IS MOTORIZED. SHOWER ENCLOSURE W/ TEMPERED GLASS DOOR FLOOR DRAIN BATHTUB CEILING MOUNTED DIVIDER--PROVIDE BLOCKING AS REQUIRED ALTERNATE LOCATION OF DOOR FOR CONNECTING ROOMS TO ACCESSIBLE ROOMS--REFER TO OVERALL PLANS FOR LOCATION OF ACCESSIBLE ROOMS DEDICATED CIRCUIT FOR DISHWASHER RANGE TOP STYLE MICROWAVE AFFIXED TO WALL MIRROR BEGIN CARPET TILE THIS SIDE W/ FULL TILE--FIRST TWO ROWS OF TILE TO BE INSTALLED AROUND BUILT-IN CASEGOODS SWITCH CONTROLLING GARBAGE DISPOSAL GANGED WITH DUPLEX. REFER TO HADG FOR ACCESSIBLE ROOM REQUIREMENTS DEDICATED CIRCUIT FOR GARBAGE DISPOSAL FIRE HORN IN STANDARD ROOMS FIRE HORN/STROBE IN COMMUNICATION FEATURES ROOMS RECESSED CEILING LIGHT FOR WET LOCATIONS W/ SHATTER PROOF LENS TOILET EXHAUST GRILLE MAKE-UP AIR DIFFUSER EXTENT OF SLEEPER SOFA APPROXIMATE LOCATIONS OF MILLWORK SUPPORTS ON FLOOR. PROVIDE SHIMS OR LEVELERS UNDER SUPPORTS TO PREVENT CARPET CRUSHING ROOM SIGNAGE HARDWIRED THERMOSTAT FOR PTAC. MOUNTED 48" MAX TO TOP OF DEVICE. COMMUNICATION BETWEEN THERMOSTAT AND PTAC MAY BE WIRELESS. EXTEND J-BOX, DEVICE & COVER PLATE FLUSH W/ MILLWORK BACK PANEL DROPPED GYPSUM BOARD BULKHEAD @ ROUGH OPENING -- WHERE PRE-MANUFACTURED SHOWER INSERT IS INDICATED. MEASURE ROUGH OPENING FROM FACE OF GYPSUM BOARD DOORBELL ON/OFF SWITCH (COMMUNICATION FEATURES ROOMS ONLY) SIGNAGE AS REQ'D. EDGE OF PTAC ABOVE CARPET TILES MIN. CEILING HEIGHT MUST BE MAINTAINED -- REFER TO HOME 2 SUITES BY HILTON STANDARDS MANUAL FRAMING SUBCONTRACTOR TO PROVIDE 3/4" F.R.T. PLYWOOD BLOCKING TO RECEIVE ITEM INDICATED - EXTEND FULL LENGTH OF OBJECT GENERAL CONTRACTOR TO COORDINATE W/ FIXTURE FABRICATOR WHERE NECESSARY TO PROVIDE PROPER BLOCKING IN WALL FOR ITEM KEYNOTED SWITCHES CONTROLLING MECHANICAL SHADES - REFER TO FFE MANUAL OUTLET ABOVE FOR MICROWAVE - REFER TO ROOM ELEVATION MOUNT DEVICE HORIZONTALLY--FACE PLATE TO BE WHITE REQUIRED ACCESSIBLE CLEAR FLOOR AREA DESIGNATION CENTER ARTWORK OVER SOFA COUNTERTOP MICROWAVE GRAPHIC ART. REFER TO ACCESSORIES LEGEND & CONSTRUCTION PLAN ADDITIONAL HORN STROBE. LOCATED IN COMMUNICATION FEATURES BATHROOMS ONLY WAP IN 3-GANG BOX MOUNTED VERTICALLY UNDER DESK. MAINTAIN 6" BETWEEN ALL BOXES. TYP. ALL GUESTROOMS. COORDINATE WAP LOCATION WITH CASEGOODS TO AVOID CONFLICTS. VISIT CONNECTEDROOM.HILTON.COM FOR CURRENT WIRELESS INTERNET REQ'S AND LIST OF APPROVED INTEGRATORS EACH CABLE MUST HOMERUN BETWEEN THE GUESTROOM AND THE IDF ON EACH FLOOR. VISIT CONNECTEDROOM.HILTON.COM FOR CURRENT REQUIREMENT AND OPTIONS OPTION WIRED DATA CONNECTION FOR GUEST USE: A) ADD CAT6 RJ-45 CABLE JACK AND PATCH CORD THROUGH DESKTOP GROMMET - OR - B) PATCH CORD FROM WAP PORT THROUGH DESKTOP GROMMET TV CONNECTIONS FOR FREE-TO-GUEST CONTENT: A) NO SMART TV: COAX CABLE BEHIND TV. CAT6 RJ-45 JACK BEHIND TV. RUN IN SMURF TUBE IN WALL TO WAP UNDER DESK. PATCH CORD TO EDGE CONTROLLER FOR CONNECTED ROOM. MIN. 6" CLEARANCE FROM WALL BOXES - OR - B) SMART TV-INTERNET PROTOCOL TELEVISION (IPTV) COAX NOT REQ'D. CAT6 RJ-45 JACK BEHIND TV. RUN IN SMURF TUBE IN WALL TO WAP UNDER DESK. PATCH CORD TO EDGE CONTROLLER FOR CONNECTED ROOM. CAT6 RJ-45 JACK BEHIND TV. IN ONE-BEDROOM TV. MIN. 6" CLEARANCE FROM WALL BOXES. VISIT HILTON.HDTV.COM FOR ADDITIONAL INFORMATION. PROVIDE HINGE STOP AT DOOR HARDWIRED BLACK OUT ROLLER SHADE WITH NO EXPOSES WIRES PROVIDE OUTLET FOR UNDERCABINET LIGHTING BY OTHERS ELECTRICAL PANEL	GR-100 OTTOMAN GR-101 SLEEPER SOFA GR-102 DINING CHAIR GR-103 TASK CHAIR GR-200 SIDE TABLE LAMP GR-201 DESK LAMP GR-202 NIGHTSTAND SCONE GR-203 VANITY SCONE GR-204 SCONE @WALL HOOK GR-205 FLOOR LAMP GR-206 TABLE LAMP GR-207 @ACCESSIBLE WORKING WALL GR-208 NIGHTSTAND SCONE GR-209 @QUEEN QUEEN CENTER GR-210 NIGHTSTAND SCONE GR-211 @QUEEN QUEEN SIDE GR-212 QUEEN HEADBOARD GR-213 KING HEADBOARD GR-214 VANITY GR-215 @GUEST BATH (LEFT&RIGHT) GR-216 ACCESSIBLE VANITY GR-217 @GUEST BATH GR-218 WORKING WALL GR-219 DINING TABLE GR-220 @ONE BEDROOM SUITE GR-221 SOFA TABLE @SOFA GR-222 NIGHTSTAND @RIGHT GR-223 DECORATIVE SHELVES ABOVE DESK GR-224 WALL SHELF @BATHROOM GR-225 NIGHTSTAND @QUEEN QUEEN GR-226 NIGHTSTAND @LEFT GR-227 WALL SHELF GR-228 @ACCESSIBLE BATHROOM GR-229 BLACKOUT & SHEER ROLLER SHADE GR-230 MOTORIZED ROLLER SHADE GR-231 DIVIDER DRAPERY GR-232 DIVIDER DRAPERY HARDWARE GR-233 CLOSET DRAPERY GR-234 ADA CLOSET DRAPERY GR-235 @GUEST SUITE GR-236 ART ABOVE SOFA GR-237 VANITY MIRROR GR-238 FULL LENGTH MIRROR GR-239 ART ABOVE DINING TABLE GR-240 @ONEBEDROOM SUITE GR-241 QUEEN MATTRESS SET GR-242 QUEEN BOX SPRING COVER GR-243 KING MATTRESS SET GR-244 KING BOX SPRING COVER GR-245 QUEEN BED BASE GR-246 QUEEN ACCESSIBLE BED BASE GR-247 KING BED BASE GR-248 KING ACCESSIBLE BED BASE GR-249 KING BED SKIRT GR-250 REFRIGERATOR GR-251 DISHWASHER GR-252 TELEVISION GR-253 CLOCK/RADIO GR-254 TELEPHONE GR-255 TUB SHOWER CURTAIN GR-256 SHOWER CURTAIN	<table><thead><tr><th>PLAN</th><th>ELEVATION</th><th>DESCRIPTION</th></tr></thead><tbody><tr><td></td><td></td><td>OUTLET - DUPLEX</td></tr><tr><td></td><td></td><td>OUTLET - DUPLEX - GFI</td></tr><tr><td></td><td></td><td>OUTLET - QUAD</td></tr><tr><td></td><td></td><td>OUTLET - QUAD - GFI</td></tr><tr><td></td><td></td><td>PHONE</td></tr><tr><td></td><td></td><td>DATA</td></tr><tr><td></td><td></td><td>OPTIONAL DATA</td></tr><tr><td></td><td></td><td>OUTLET - TV</td></tr><tr><td></td><td></td><td>SWITCH, 3 WAY, 4 WAY</td></tr><tr><td></td><td></td><td>J BOX</td></tr><tr><td></td><td></td><td>ALARM STROBE</td></tr><tr><td></td><td></td><td>DOORBELL</td></tr><tr><td></td><td></td><td>SMOKE DETECTOR</td></tr><tr><td></td><td></td><td>THERMOSTAT</td></tr><tr><td></td><td></td><td>ALARM HORN AND STROBE</td></tr><tr><td></td><td></td><td>SIDE WALL SPRINKLER HEAD</td></tr><tr><td></td><td></td><td>SPRINKLER HEAD</td></tr><tr><td></td><td></td><td>SIDE WALL SPRINKLER HEAD</td></tr><tr><td></td><td></td><td>WAP</td></tr><tr><td></td><td></td><td>ELECTRICAL PANEL</td></tr></tbody></table>	PLAN	ELEVATION	DESCRIPTION			OUTLET - DUPLEX			OUTLET - DUPLEX - GFI			OUTLET - QUAD			OUTLET - QUAD - GFI			PHONE			DATA			OPTIONAL DATA			OUTLET - TV			SWITCH, 3 WAY, 4 WAY			J BOX			ALARM STROBE			DOORBELL			SMOKE DETECTOR			THERMOSTAT			ALARM HORN AND STROBE			SIDE WALL SPRINKLER HEAD			SPRINKLER HEAD			SIDE WALL SPRINKLER HEAD			WAP			ELECTRICAL PANEL
PLAN	ELEVATION	DESCRIPTION	
		OUTLET - DUPLEX	
		OUTLET - DUPLEX - GFI	
		OUTLET - QUAD	
		OUTLET - QUAD - GFI	
		PHONE	
		DATA	
		OPTIONAL DATA	
		OUTLET - TV	
		SWITCH, 3 WAY, 4 WAY	
		J BOX	
		ALARM STROBE	
		DOORBELL	
		SMOKE DETECTOR	
		THERMOSTAT	
		ALARM HORN AND STROBE	
		SIDE WALL SPRINKLER HEAD	
		SPRINKLER HEAD	
		SIDE WALL SPRINKLER HEAD	
		WAP	
		ELECTRICAL PANEL	

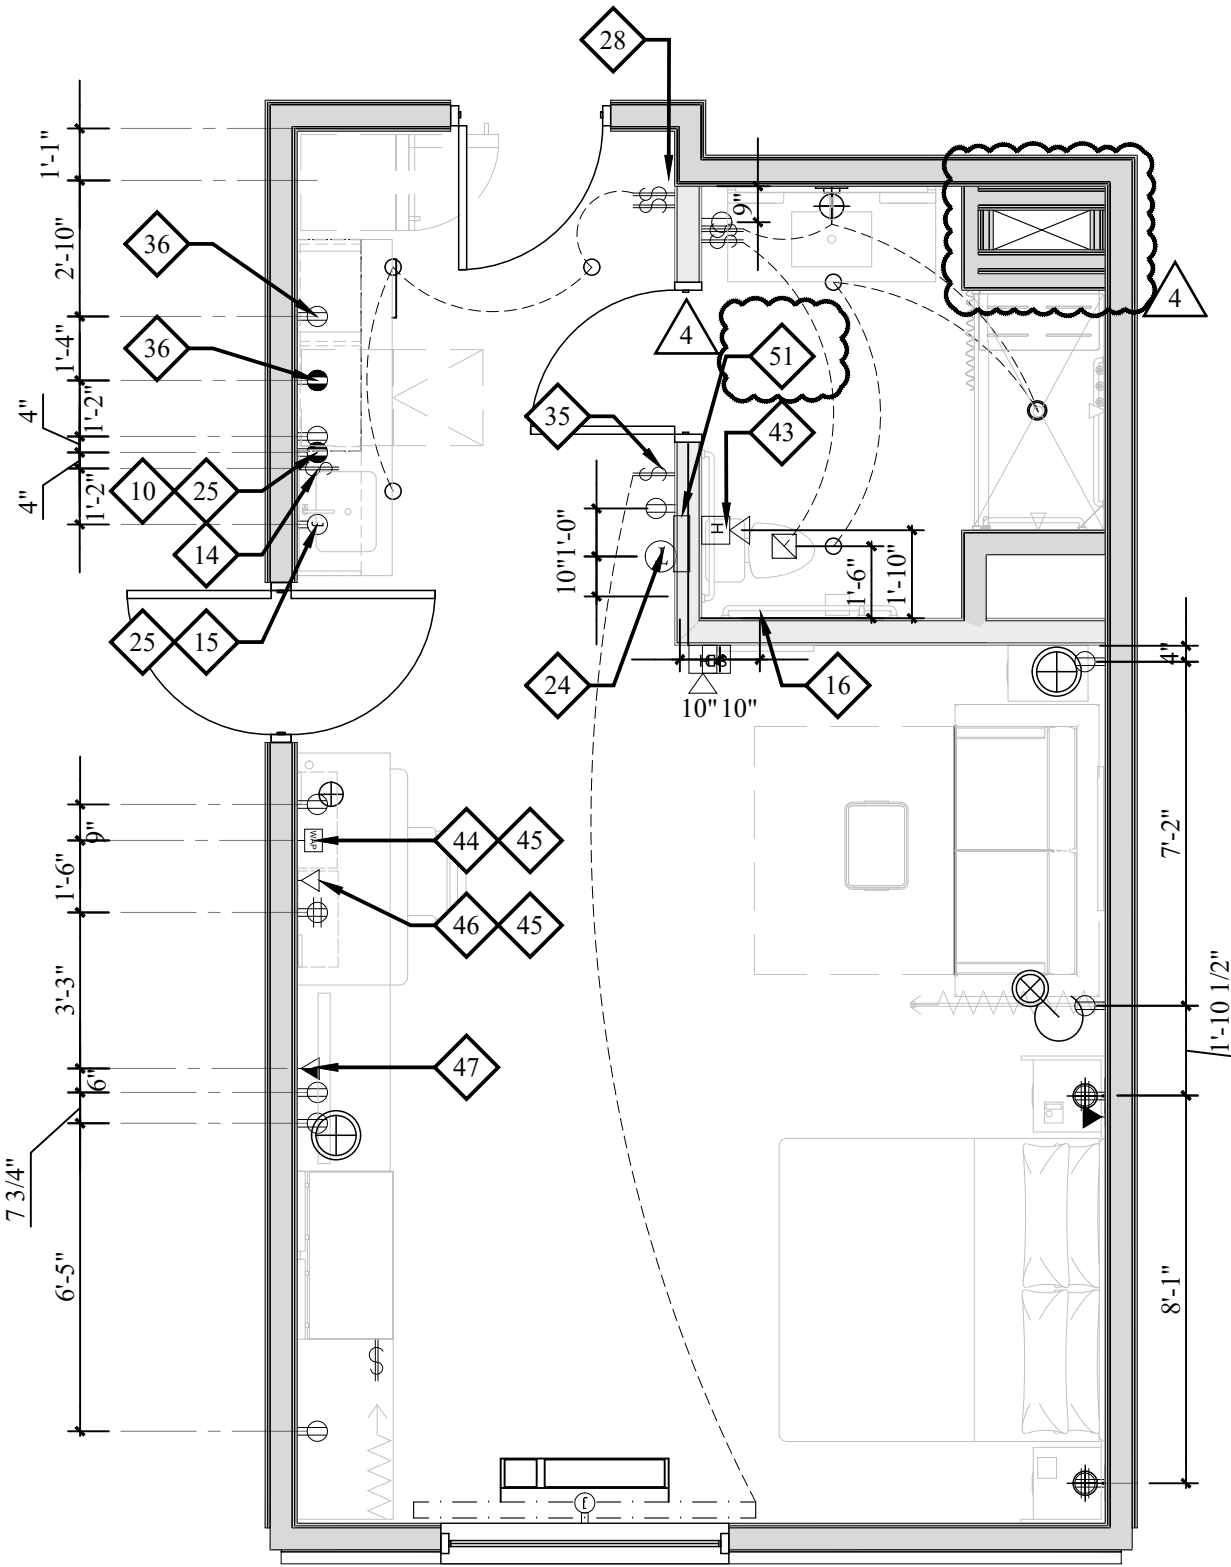


04 KING STUDIO ACC MOD-ELECTRICAL PLAN
1/4" = 1'-0"

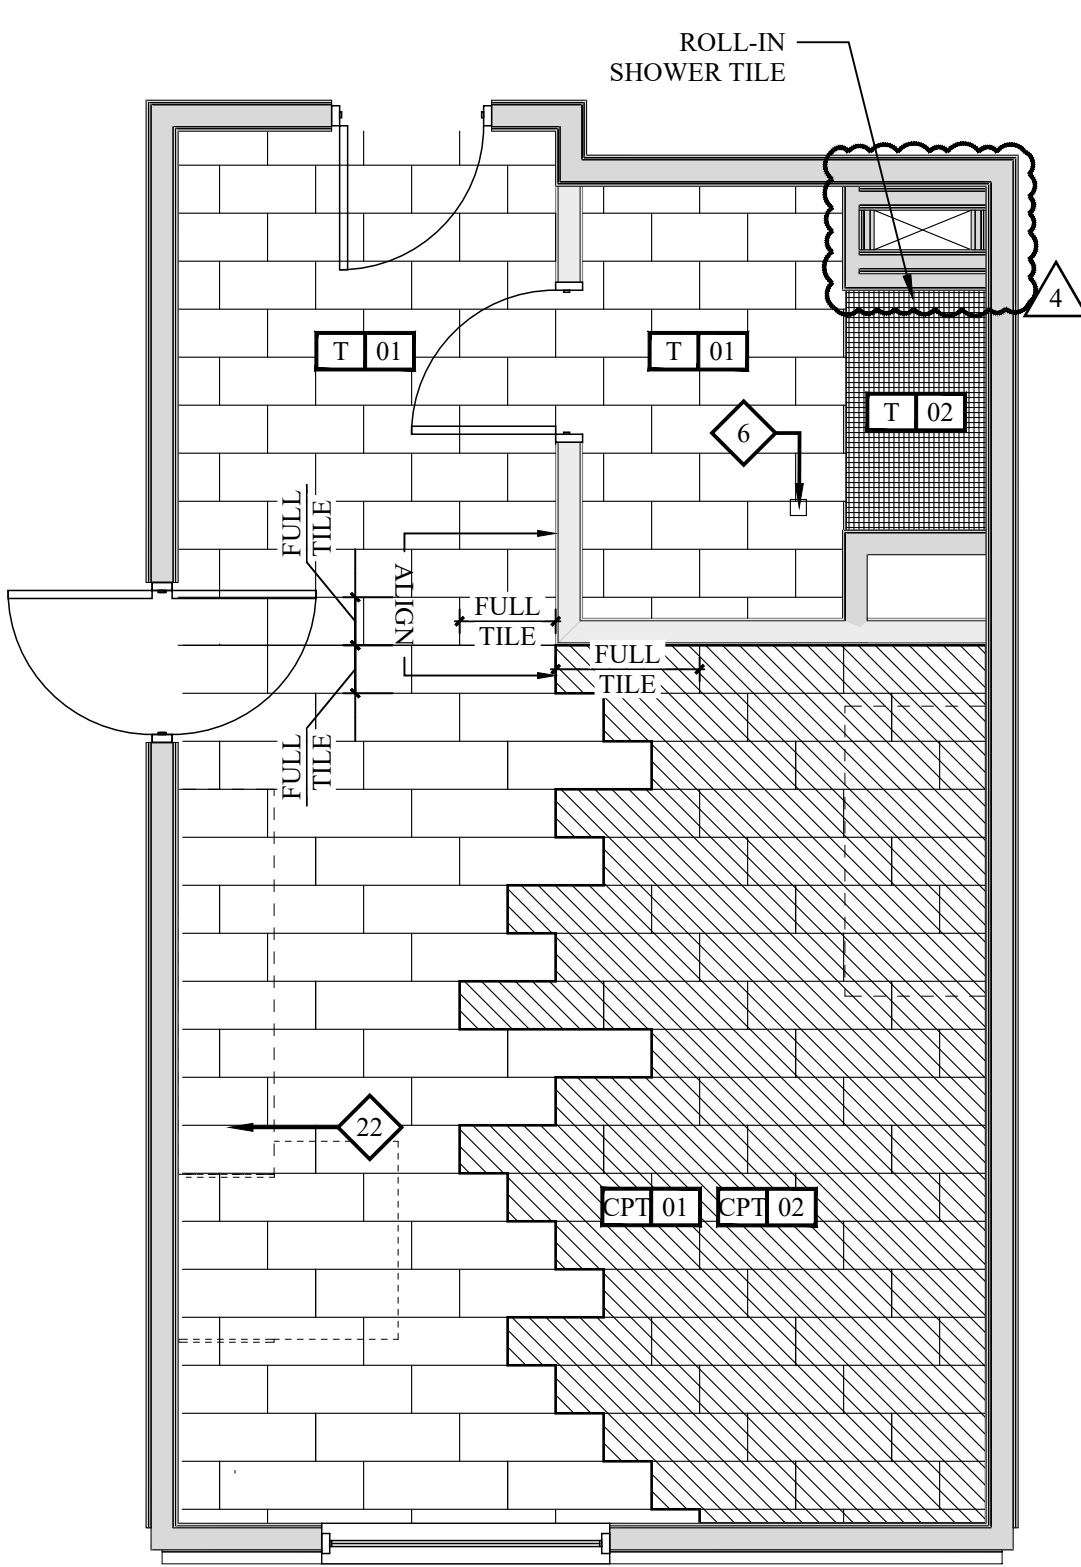


03 KING STUDIO ACC MOD-FINISH PLAN
1/4" = 1'-0"

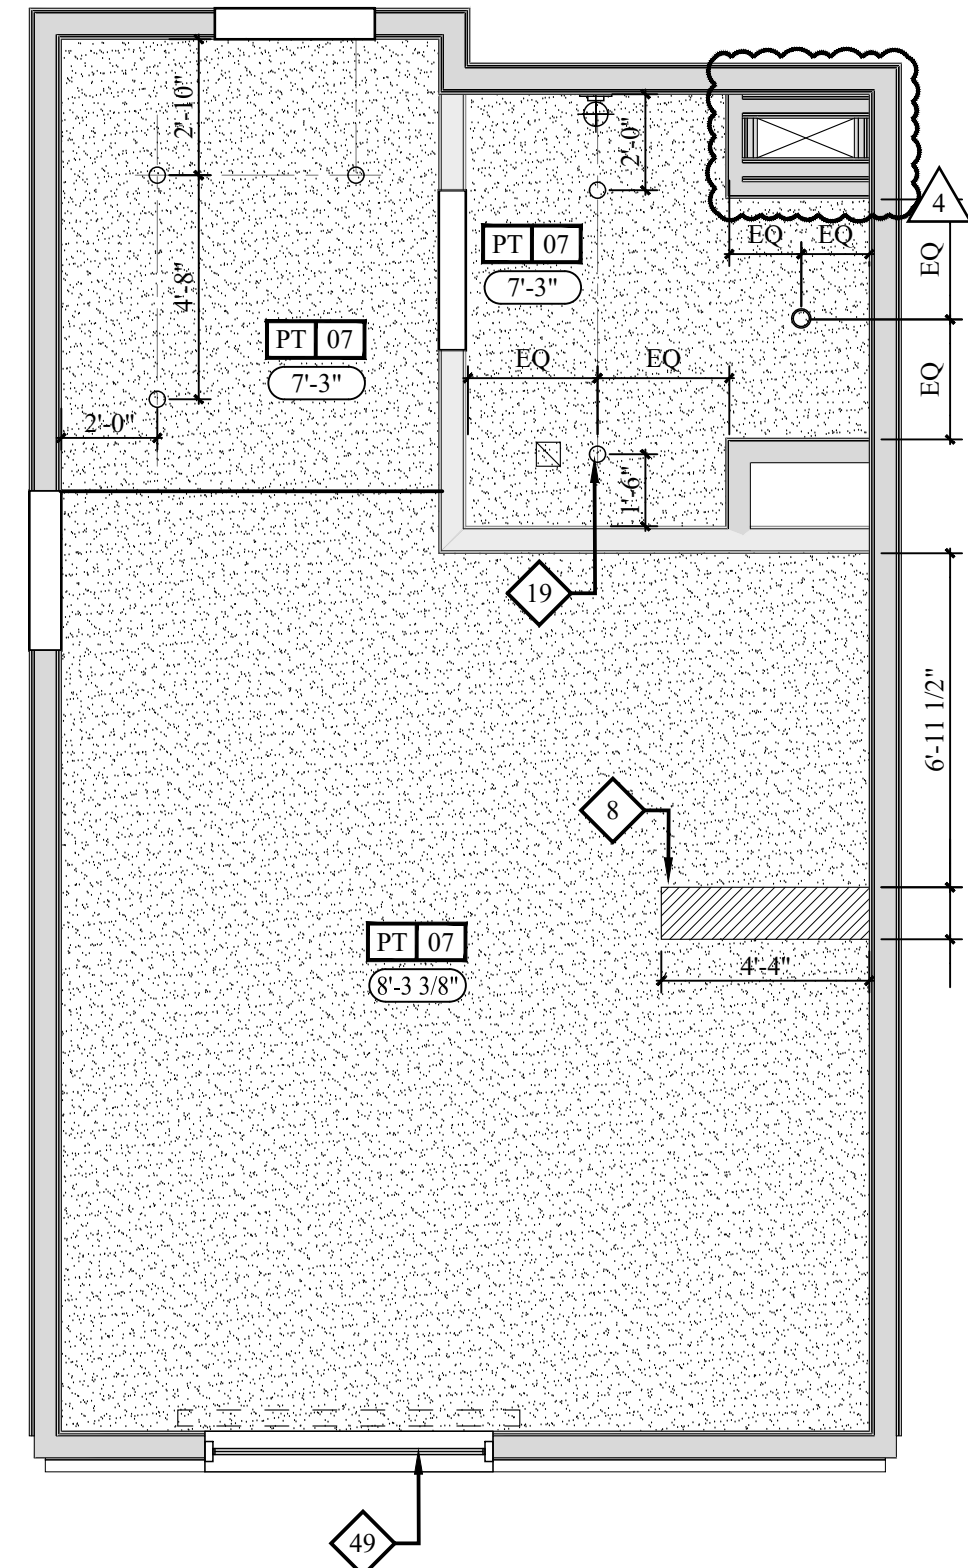


02 KING STUDIO ACC MOD-REFLECTED CEILING PLAN
1/4" = 1'-0"

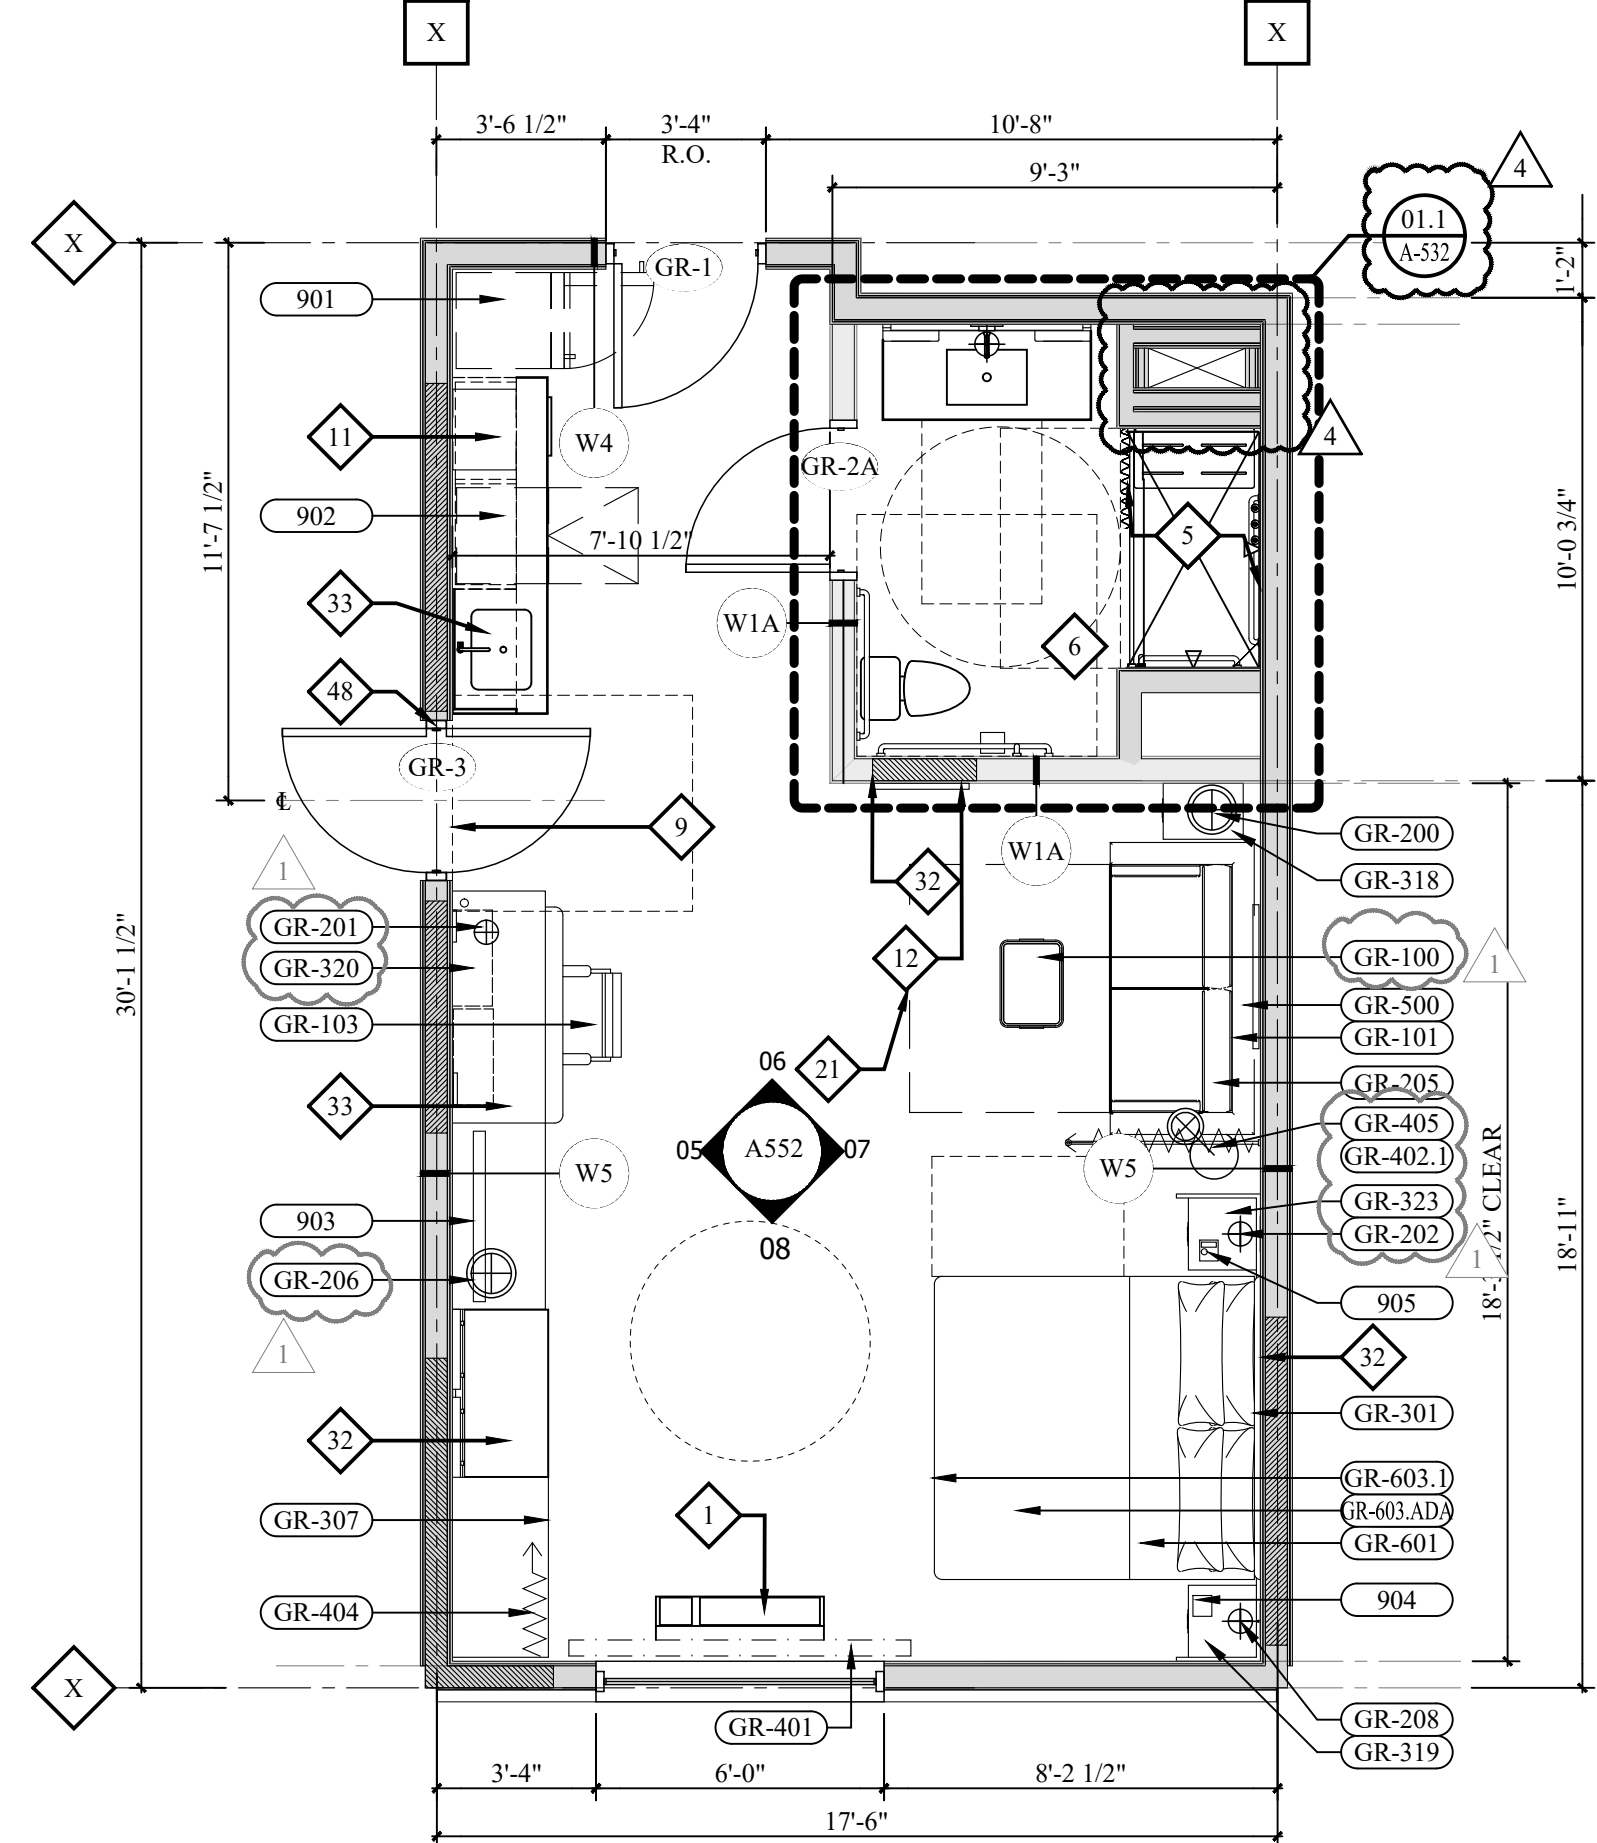


01 KING STUDIO ACC MOD-ARCHITECTURAL PLAN
1/4" = 1'-0"

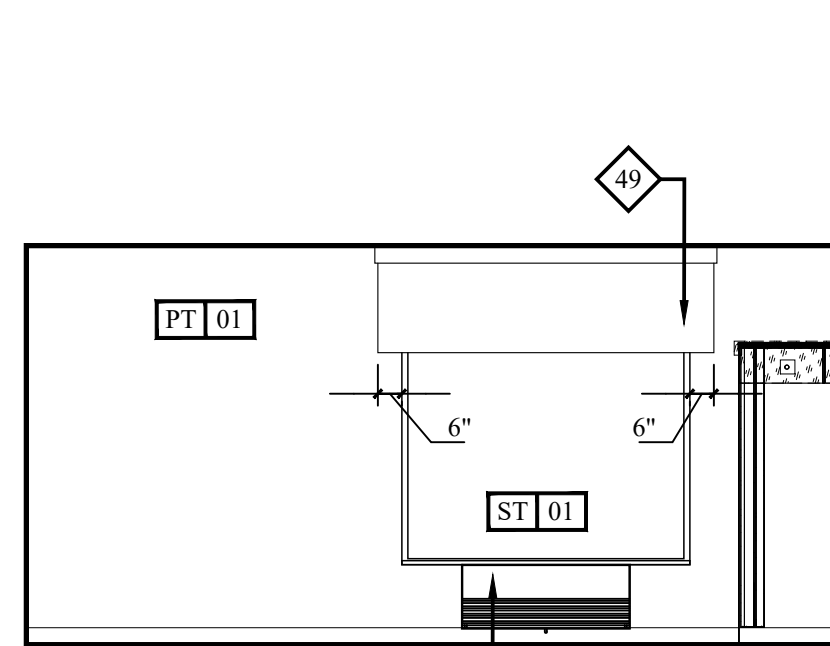


08 INTERIOR ELEVATION
1/4" = 1'-0"

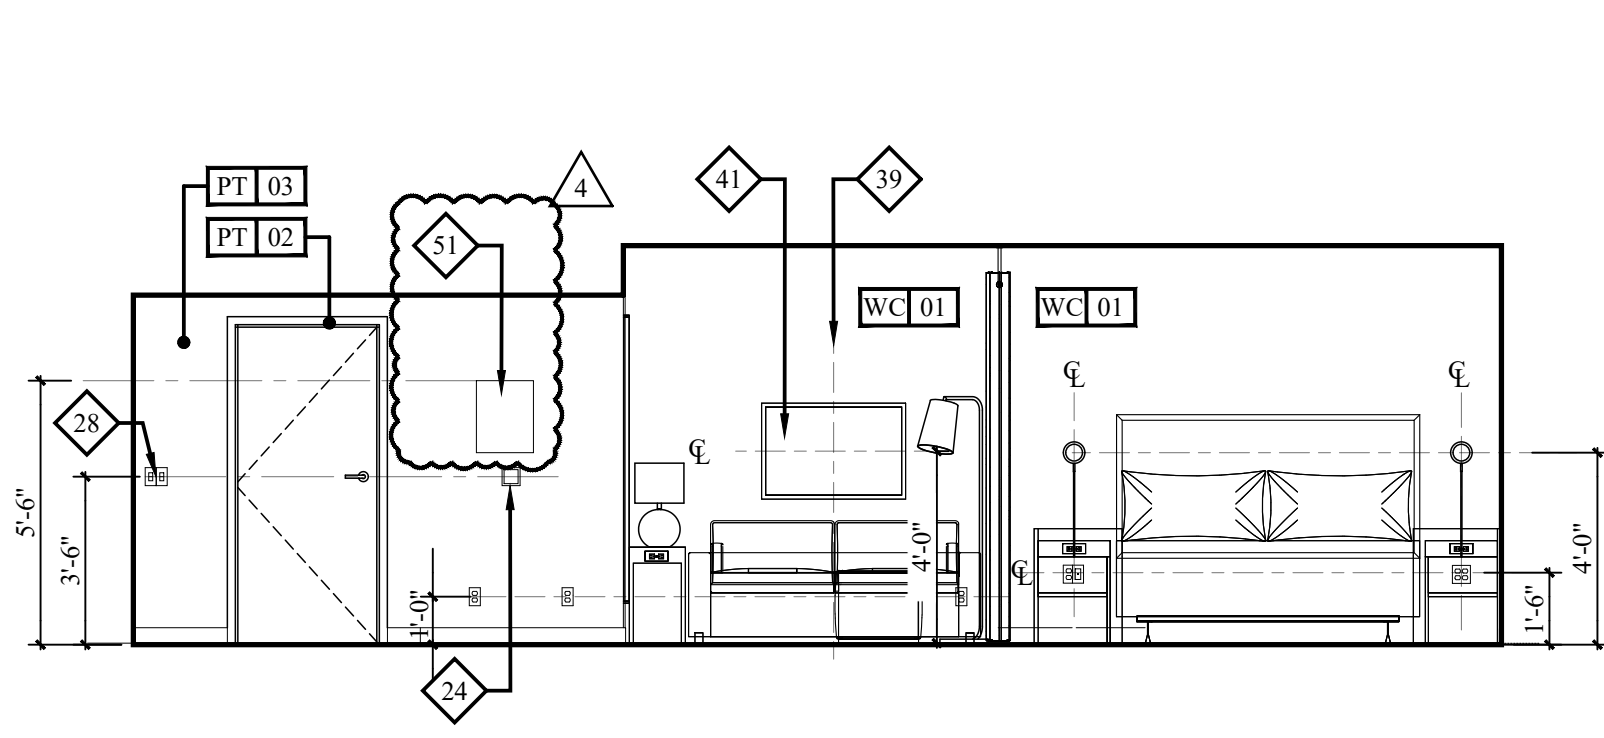


07 INTERIOR ELEVATION
1/4" = 1'-0"

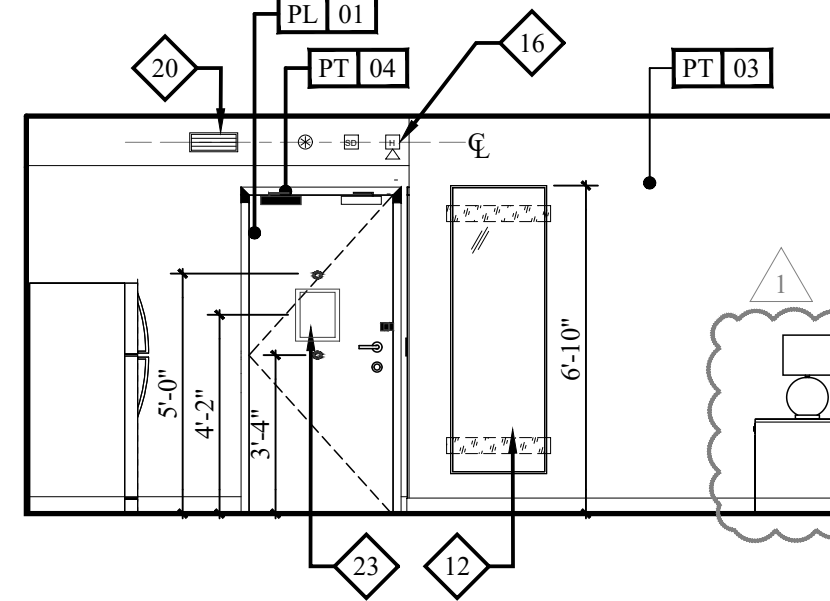

06 INTERIOR ELEVATION
1/4" = 1'-0"

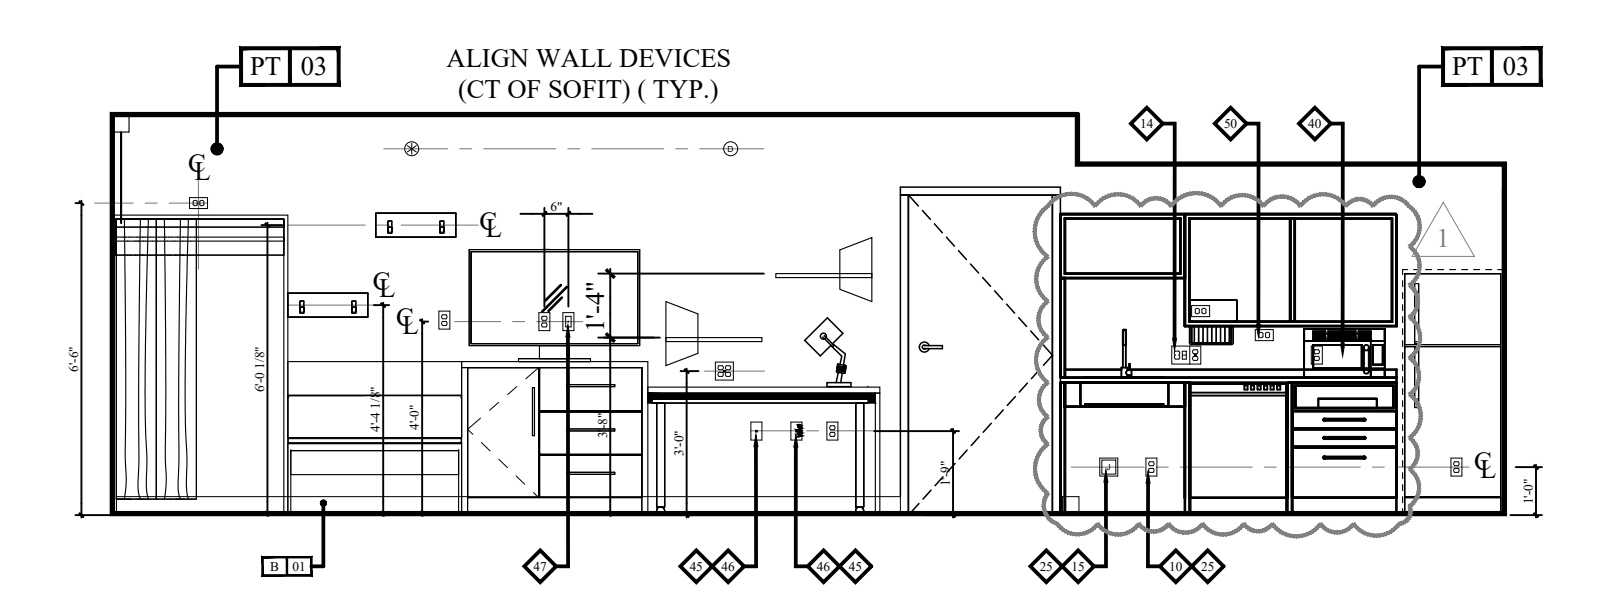


05 INTERIOR ELEVATION
1/4" = 1'-0"

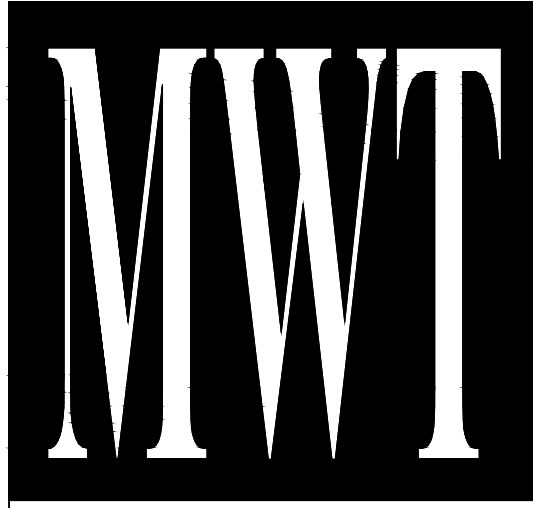

3827 BILLO ROAD
ALDEN, NY, 14004
716-631-0600
ARCHITECT OF RECORD

DONALD M. EDWARD
LICENSE #: 20212
10800 ALABASTER DR.
DAVIDSON, NC 28036
donedwardarchitect@gmail.com

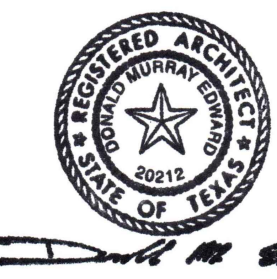

08/09/2024

WARNING
IT IS A VIOLATION OF THE LAW FOR ANY PERSON, UNLESS ACTING UNDER THE DIRECTION OF THE ARCHITECT OR ENGINEER, TO ALTER OR REPRODUCE THESE DRAWINGS IN ANY WAY.

DRAWING QUESTIONS
CA@MWTUSA.COM
1-800-717-5816

ISSUED FOR :

CONSTRUCTION AND BID SET



EAGLE PASS, TX 78852
PROTOTYPE VERSION: 3.0

REVISIONS

NO.	DESCRIPTION	DATE	BY
1	FF&E FRANCHISE UPDATE	08/04/23	-
2	PER STRUCTURAL UPDATE	-	-
3	REVISED PER CITY COMMENT	-	-
4	REVISED	08/09/24	-

PROJECT NO.: 22-014

DATE: 08/09/24

DRAWN BY: RH/EY/BS

CHKD. BY: AS

ENL. GUEST ROOM
PLANS & ELEVS
- KING STUDIO
ACC. MOD.

SHEET

A552

22-014 A552 ENLARGE GUEST ROOM KING ACC MOD.dwg

IMPORTANT NOTICE TO ALL CONTRACTORS AND OR SUBCONTRACTORS: (COMPLETE BUILDING SYSTEMS AND OR INSTALLATIONS)

IF AWARDED A CONTRACT FOR ANY PORTION OF WORK NEEDED TO COMPLETE THIS PROJECT YOU ARE AGREEING TO THE FOLLOWING TERMS:

- YOU ARE A QUALIFIED CONTRACTOR AND OR SUBCONTRACTOR SPECIFICALLY IN PROVIDING A COMPLETE TURNKEY SERVICE IN YOUR TRADE OR PROFESSION FOR THE TYPE OF WORK AND SCOPE FOR THIS PROJECT.
- YOU AGREE TO PROVIDE A COMPLETE DESIGN BUILD SOLUTION BASED ON THE ARCHITECTS INTENDED DESIGN FOR THIS PROJECT.
- YOUR BID INCLUDES ALL THE STEPS, PROCESSES, MATERIALS, PRODUCTS, GOVERNING PERMITS AND APPROVALS NECESSARY TO PROVIDE A COMPLETED AND WARRANTED SYSTEM OR INSTALLATION THAT DOES NOT REQUIRE ANOTHER CONTRACTOR OR PRODUCT TO COMPLETE YOUR SCOPE OF WORK.
- YOUR BID MUST HAVE INCLUDED ANY DESIGN INFORMATION REFERENCED WITHIN ANY CIVIL, ARCHITECTURAL, STRUCTURAL, MECHANICAL, ELECTRICAL AND OR PLUMBING DRAWINGS. ALSO NOTE THESE DRAWINGS ARE SCHEMATIC AND ARE INTENDED TO SHOW ONLY BASIC CONCEPTS AND GENERAL INFORMATION. THE COMPLETION OF YOUR WORK MAY INCLUDE OTHER STEPS, PROCESSES, MATERIALS, PRODUCTS, LABOR, GOVERNING PERMITS AND OR APPROVALS NECESSARY TO PROVIDE A COMPLETE SYSTEM INSTALLATION WHETHER SUGGESTED ON THE DRAWINGS OR NOT.
- AS AN EXAMPLE, ITEMS AND OR TASKS LIKE: FIRE CAULK, DRAFT STOPS, FASTENERS, ANCHORS, EMBEDMENTS, DUMPSTERS, DEBRIS CLEAN UP, ETC. ARE YOUR RESPONSIBILITY. ANY WORK NOT COMPLETED IN A TIMELY MANNER, OR INCOMPLETE WORK WILL BE BILLED BACK TO THE CONTRACTOR AND OR SUBCONTRACTOR, AT THE OWNERS' DISCRETION.