

**ELEC. PLAN
@ QQ CONN.**

**GENERAL CONTRACTOR TO COORDINATE W/
FIXTURE FABRICATOR WHERE NECESSARY TO
PROVIDE PROPER BLOCKING IN WALL FOR ITEM
KEYNOTED**

**SWITCHES CONTROLLING MECHANICAL SHADES -
REFER TO FFE MANUAL**

**OUTLET ABOVE FOR MICROWAVE - REFER TO ROOM
ELEVATION MOUNT DEVICE HORIZONTALLY-FACE
PLATE TO BE WHITE**

**REQUIRED ACCESSIBLE CLEAR FLOOR AREA
DESIGNATION**

CENTER ARTWORK OVER SOFA

COUNTERTOP MICROWAVE

**GRAPHIC ART, REFER TO ACCESSORIES LEGEND &
CONSTRUCTION PLAN**

**ADDITIONAL HORN STROBE: LOCATED IN
COMMUNICATION FEATURES BATHROOMS ONLY**

**WAP IN 3-GANG BOX MOUNTED VERTICALLY UNDER
DESK. MAINTAIN 6" BETWEEN ALL BOXES. TYP. ALL
GUESTROOMS. COORDINATE WAP LOCATION WITH
CASEGOODS TO AVOID CONFLICTS. VISIT
CONNECTEDROOM.HILTON.COM FOR CURRENT
WIRELESS INTERNET REQS AND LIST OF APPROVED
INTEGRATORS**

**EACH CABLE MUST HOMERUN BETWEEN THE
GUESTROOM AND THE IDF ON EACH FLOOR.
VISIT CONNECTEDROOM.HILTON.COM FOR CURRENT
REQUIREMENT AND OPTIONS**

**OPTION WIRED DATA CONNECTION FOR GUEST USE:
A) ADD CAT6 RJ-45 CABLE JACK AND PATCH CORD
THROUGH DESKTOP GROMMET - OR - B) PATCH CORD
FROM WAP PORT THROUGH DESKTOP GROMMET**

**TV CONNECTIONS FOR FREE-TO-GUEST CONTENT: A)
NO SMART TV: COAX CABLE BEHIND TV. CAT6 RJ-45
JACK BEHIND TV. RUN IN SMURF TUBE IN WALL TO
WAP UNDER DESK. PATCH CORD TO EDGE
CONTROLLER FOR CONNECTED ROOM. MIN. 6"
CLEARANCE FROM WALL BOXES - OR - B) SMART
TV-INTERNET PROTOCOL TELEVISION (IPTV) COAX
NOT REQ'D. CAT6 RJ-45 JACK BEHIND TV RUN IN
SMURF TUBE IN WALL TO WAP UNDER DESK. PATCH
CORD TO EDGE CONTROLLER FOR CONNECTED
ROOM. CAT6 RJ-45 JACK BEHIND TV
IN ONE-BEDROOM TV. MIN. 6" CLEARANCE FROM WALL
BOXES. VISIT HILTON HDTV.COM FOR ADDITIONAL
INFORMATION.**

PROVIDE HINGE STOP AT DOOR





**HARDWIRED BLACK OUT ROLLER SHADE WITH NO
EXPOSURE WIRES**

**PROVIDE OUTLET FOR UNDERCABINET LIGHTING BY
OTHERS**

ELECTRICAL PANEL

04.1 1/4" = 1'-0"

04 ELECTRICAL PLAN
1/4" = 1'-0"

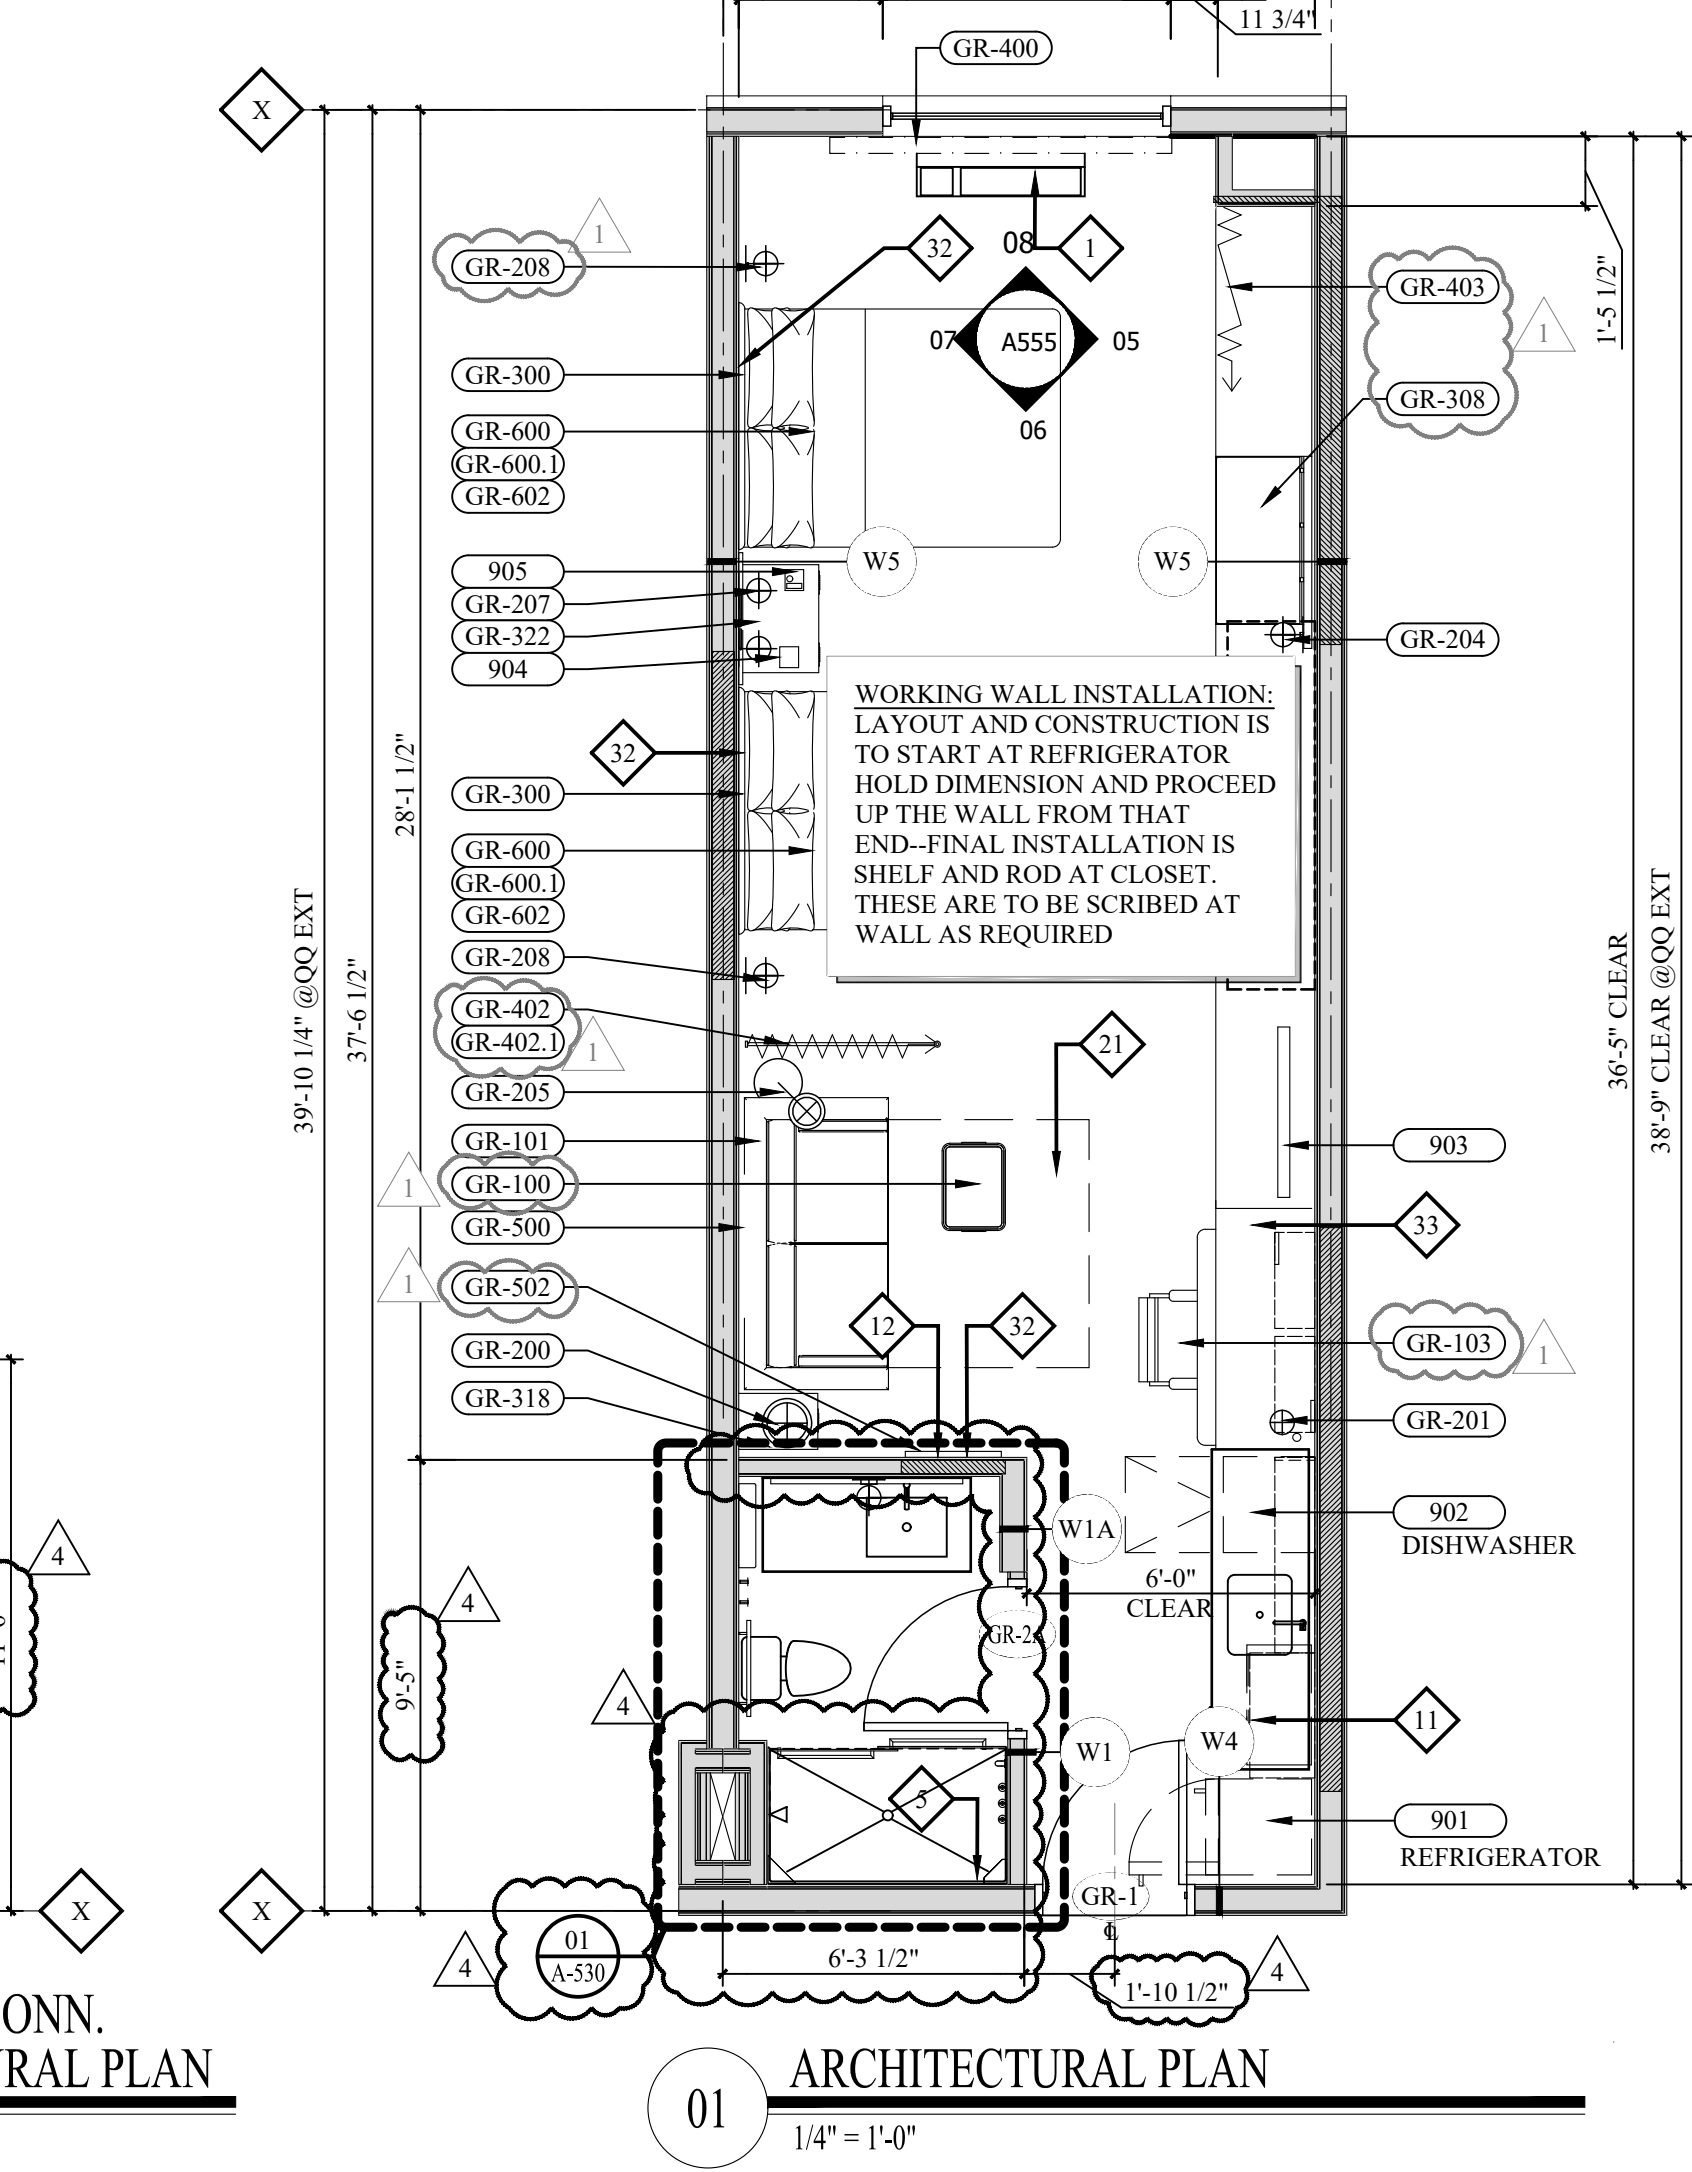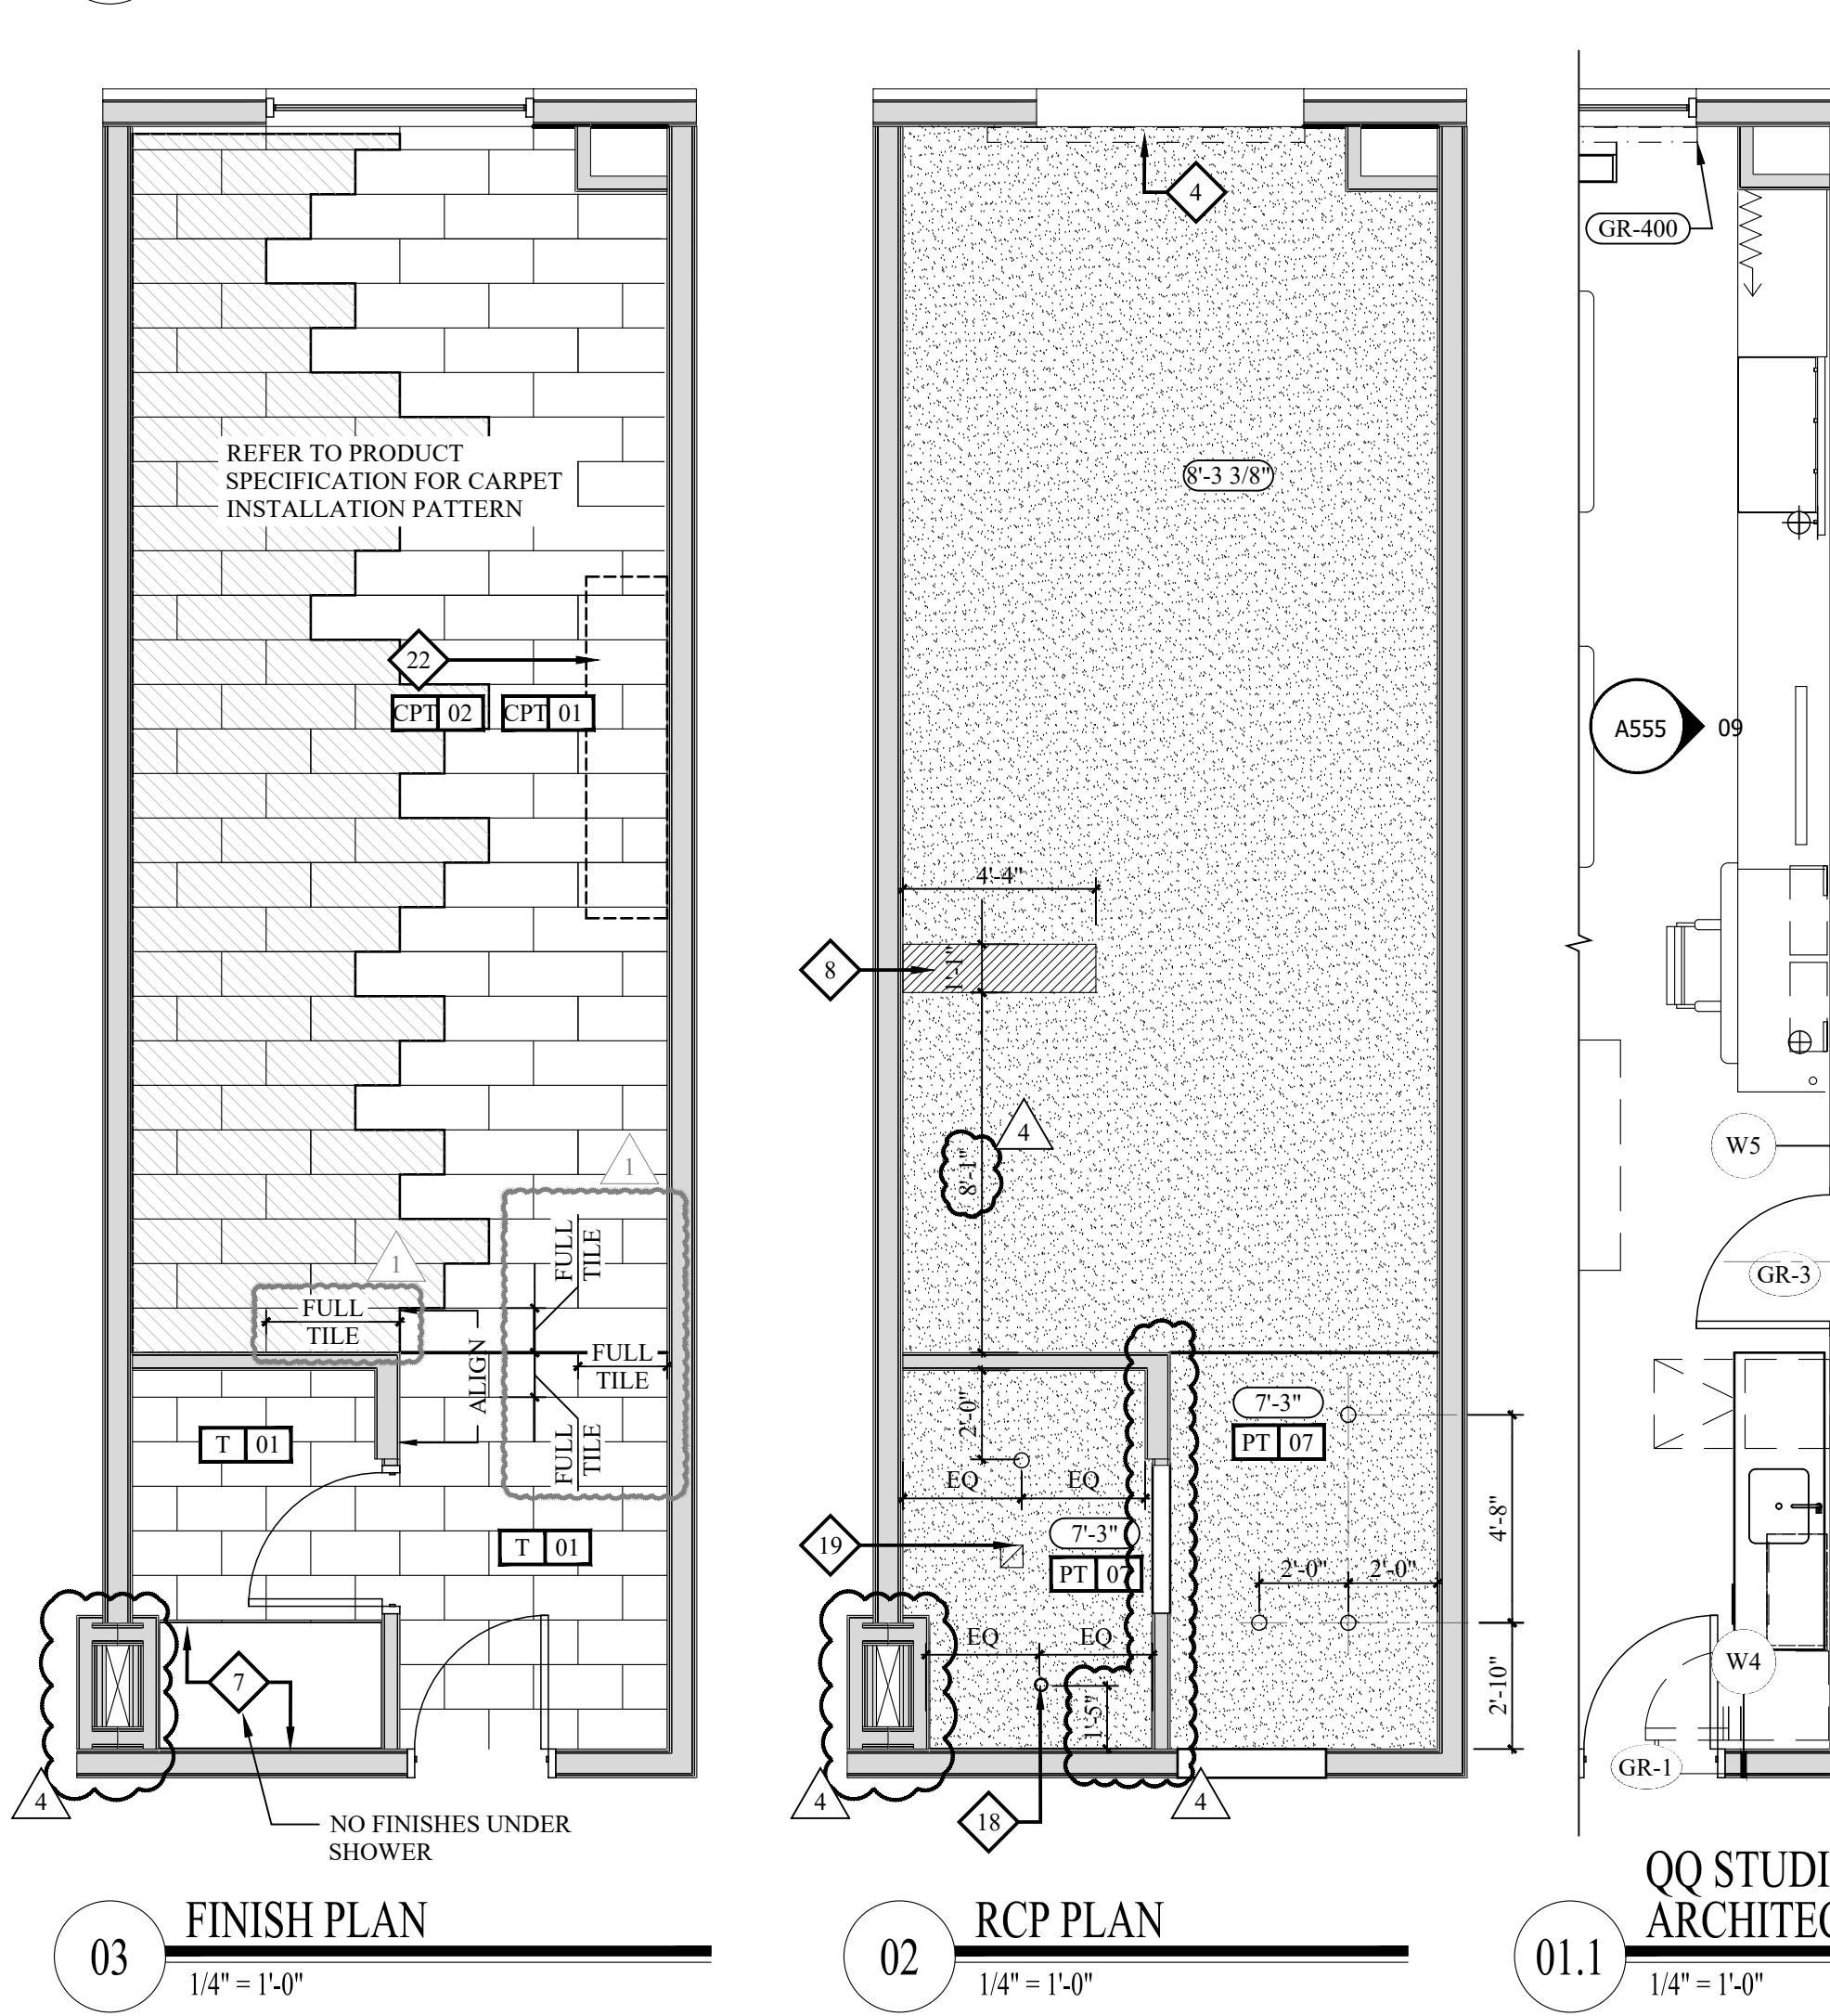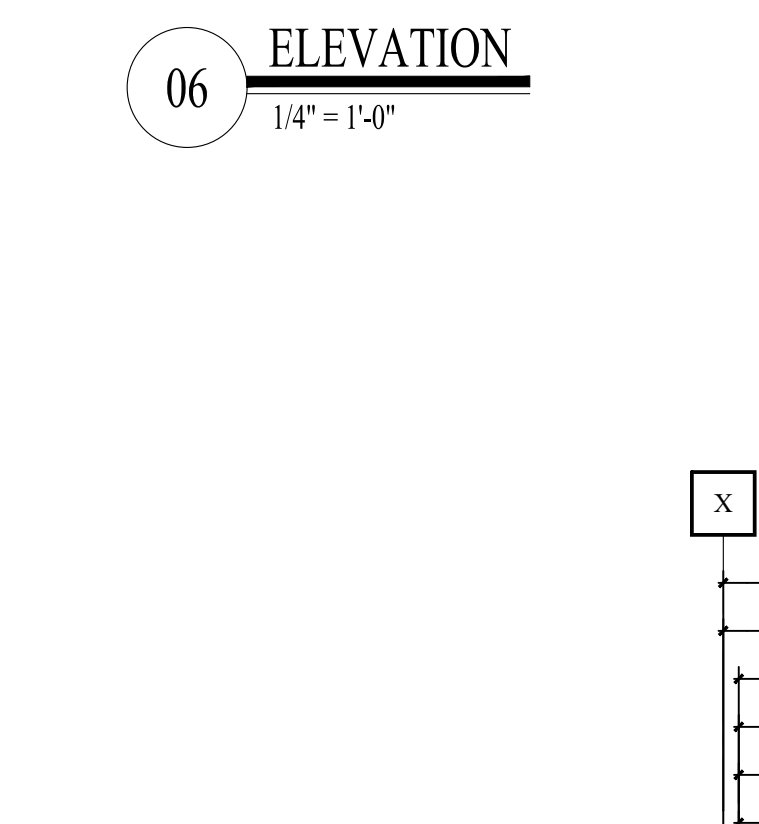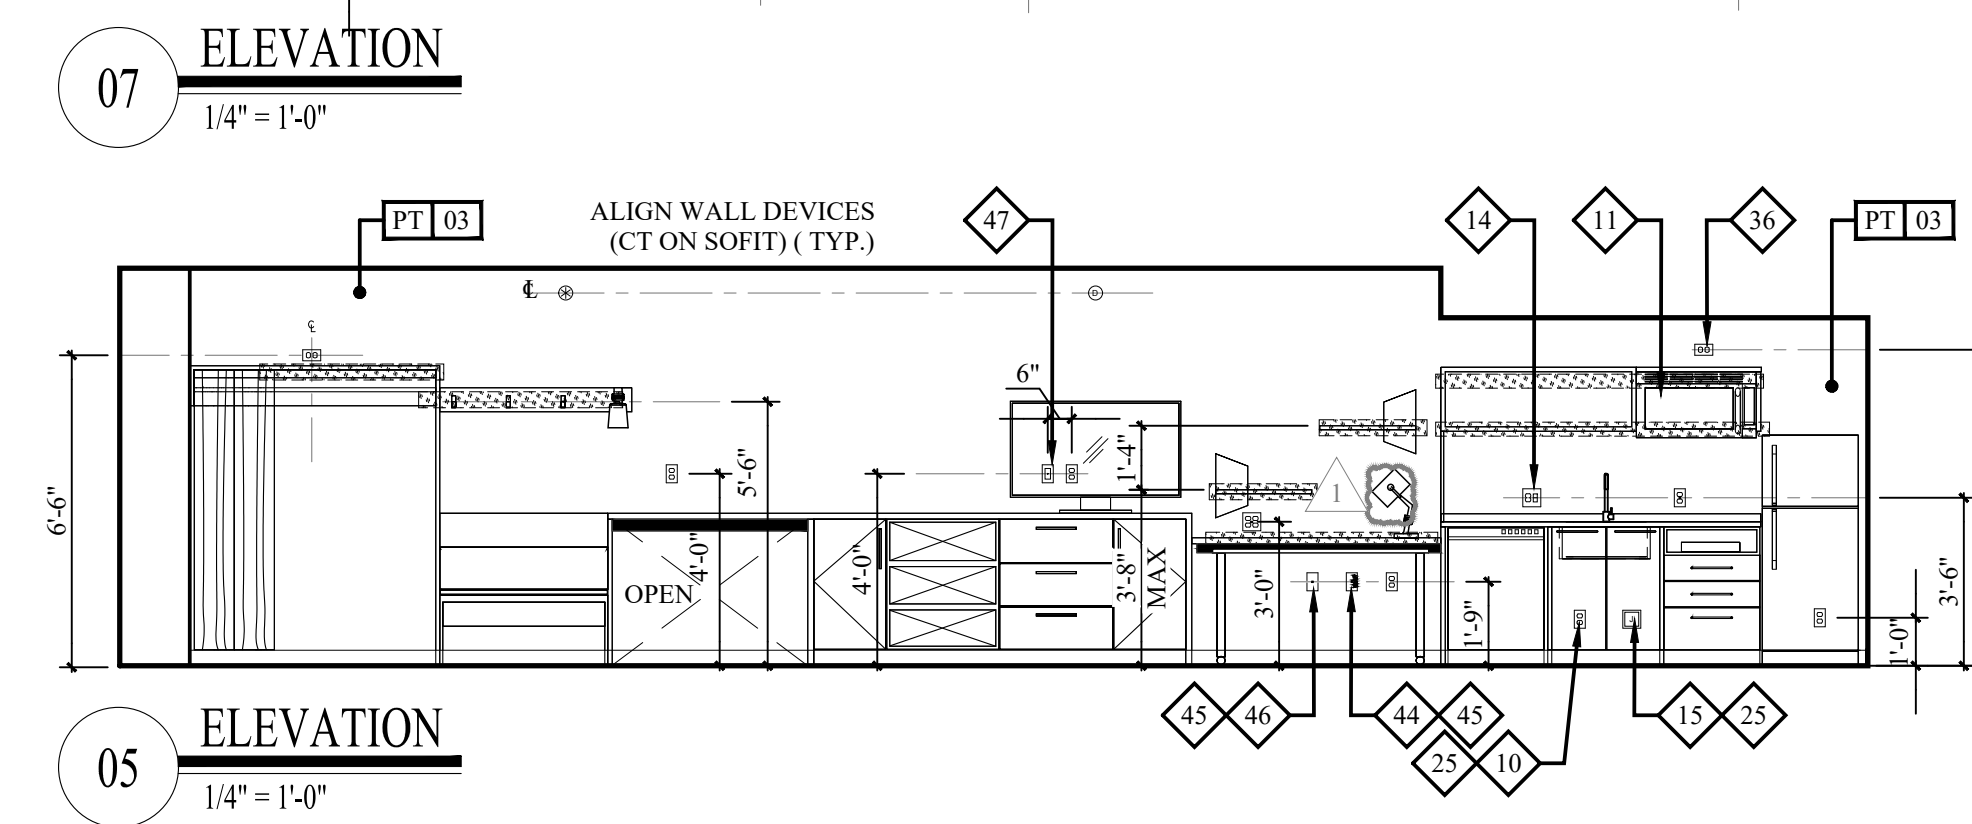

IF AWARD OF A CONTRACT FOR ANY PORTION OF WORK NOTED TO COMPLETE THIS PROJECT YOU ARE AGREEING TO THE FOLLOWING TERMS:

YOU AGREE TO QUALIFY CONTRACTOR AND SUB-CONTRACTOR FOR YOURSELF IN ADVANCE OF PROVIDING A CONTRACT TO YOUR CLIENT OR PROFESSION, FOR THE TYPE OF WORK AND SCOPE FOR THIS PROJECT.

YOU AGREE TO PROVIDE A COMPLETE DESIGN AND BUILD SOLUTION BASED ON THE ARCHITECT'S INTENDED DESIGN FOR THE PROJECT.

YOU AGREE TO THE DESIGN, PROCESS, MATERIALS, PRODUCT, MANUFACTURING, INSTALLATION, MAINTENANCE AND WARRANTY SYSTEMS TO PROVIDE A COMPLETE AND WARRANTED SYSTEM OR INSTALLATION THAT DOES NOT REQUIRE ANOTHER CONTRACTOR OR CONTRACTOR TO COMPLETE YOUR SCOPE OF WORK.

YOUR WORK MUST HAVE INCLUDED ANY NECESSARY INFORMATION REFERENCED WITHIN ANY CIVIL, ARCHITECTURAL, STRUCTURAL, MECHANICAL, ELECTRICAL AND/OR PLUMBING DRAWINGS; ALSO NOTE THESE DRAWINGS ARE SCHEMATIC AND ARE INTENDED TO SHOW ONLY BASIC CONCEPTS AND GENERAL INFORMATION. THE COMPLETION OF THE PROJECT IS YOUR RESPONSIBILITY.

YOUR WORK MUST BE COMPLETED WITHIN THE SPECIFIED TIME FRAME. 

ON ANY EXISTING ITEMS OR TASKS LIKE: FIRE, CABLE, DRAFT STOPS, FASTENERS, ANCHORS, EMBELLISHMENTS, DUMPS, DEBRIS CLEAN UP, ETC. ARE YOUR RESPONSIBILITY. ANY WORK NOTED IN A TIME FRAME, OR ON COMPLETE WORK WILL BE LEFT BACK TO THE CONTRACTOR AND/OR SUBCONTRACTOR. AT THE OWNER'S RISK.

SHEET
A555