



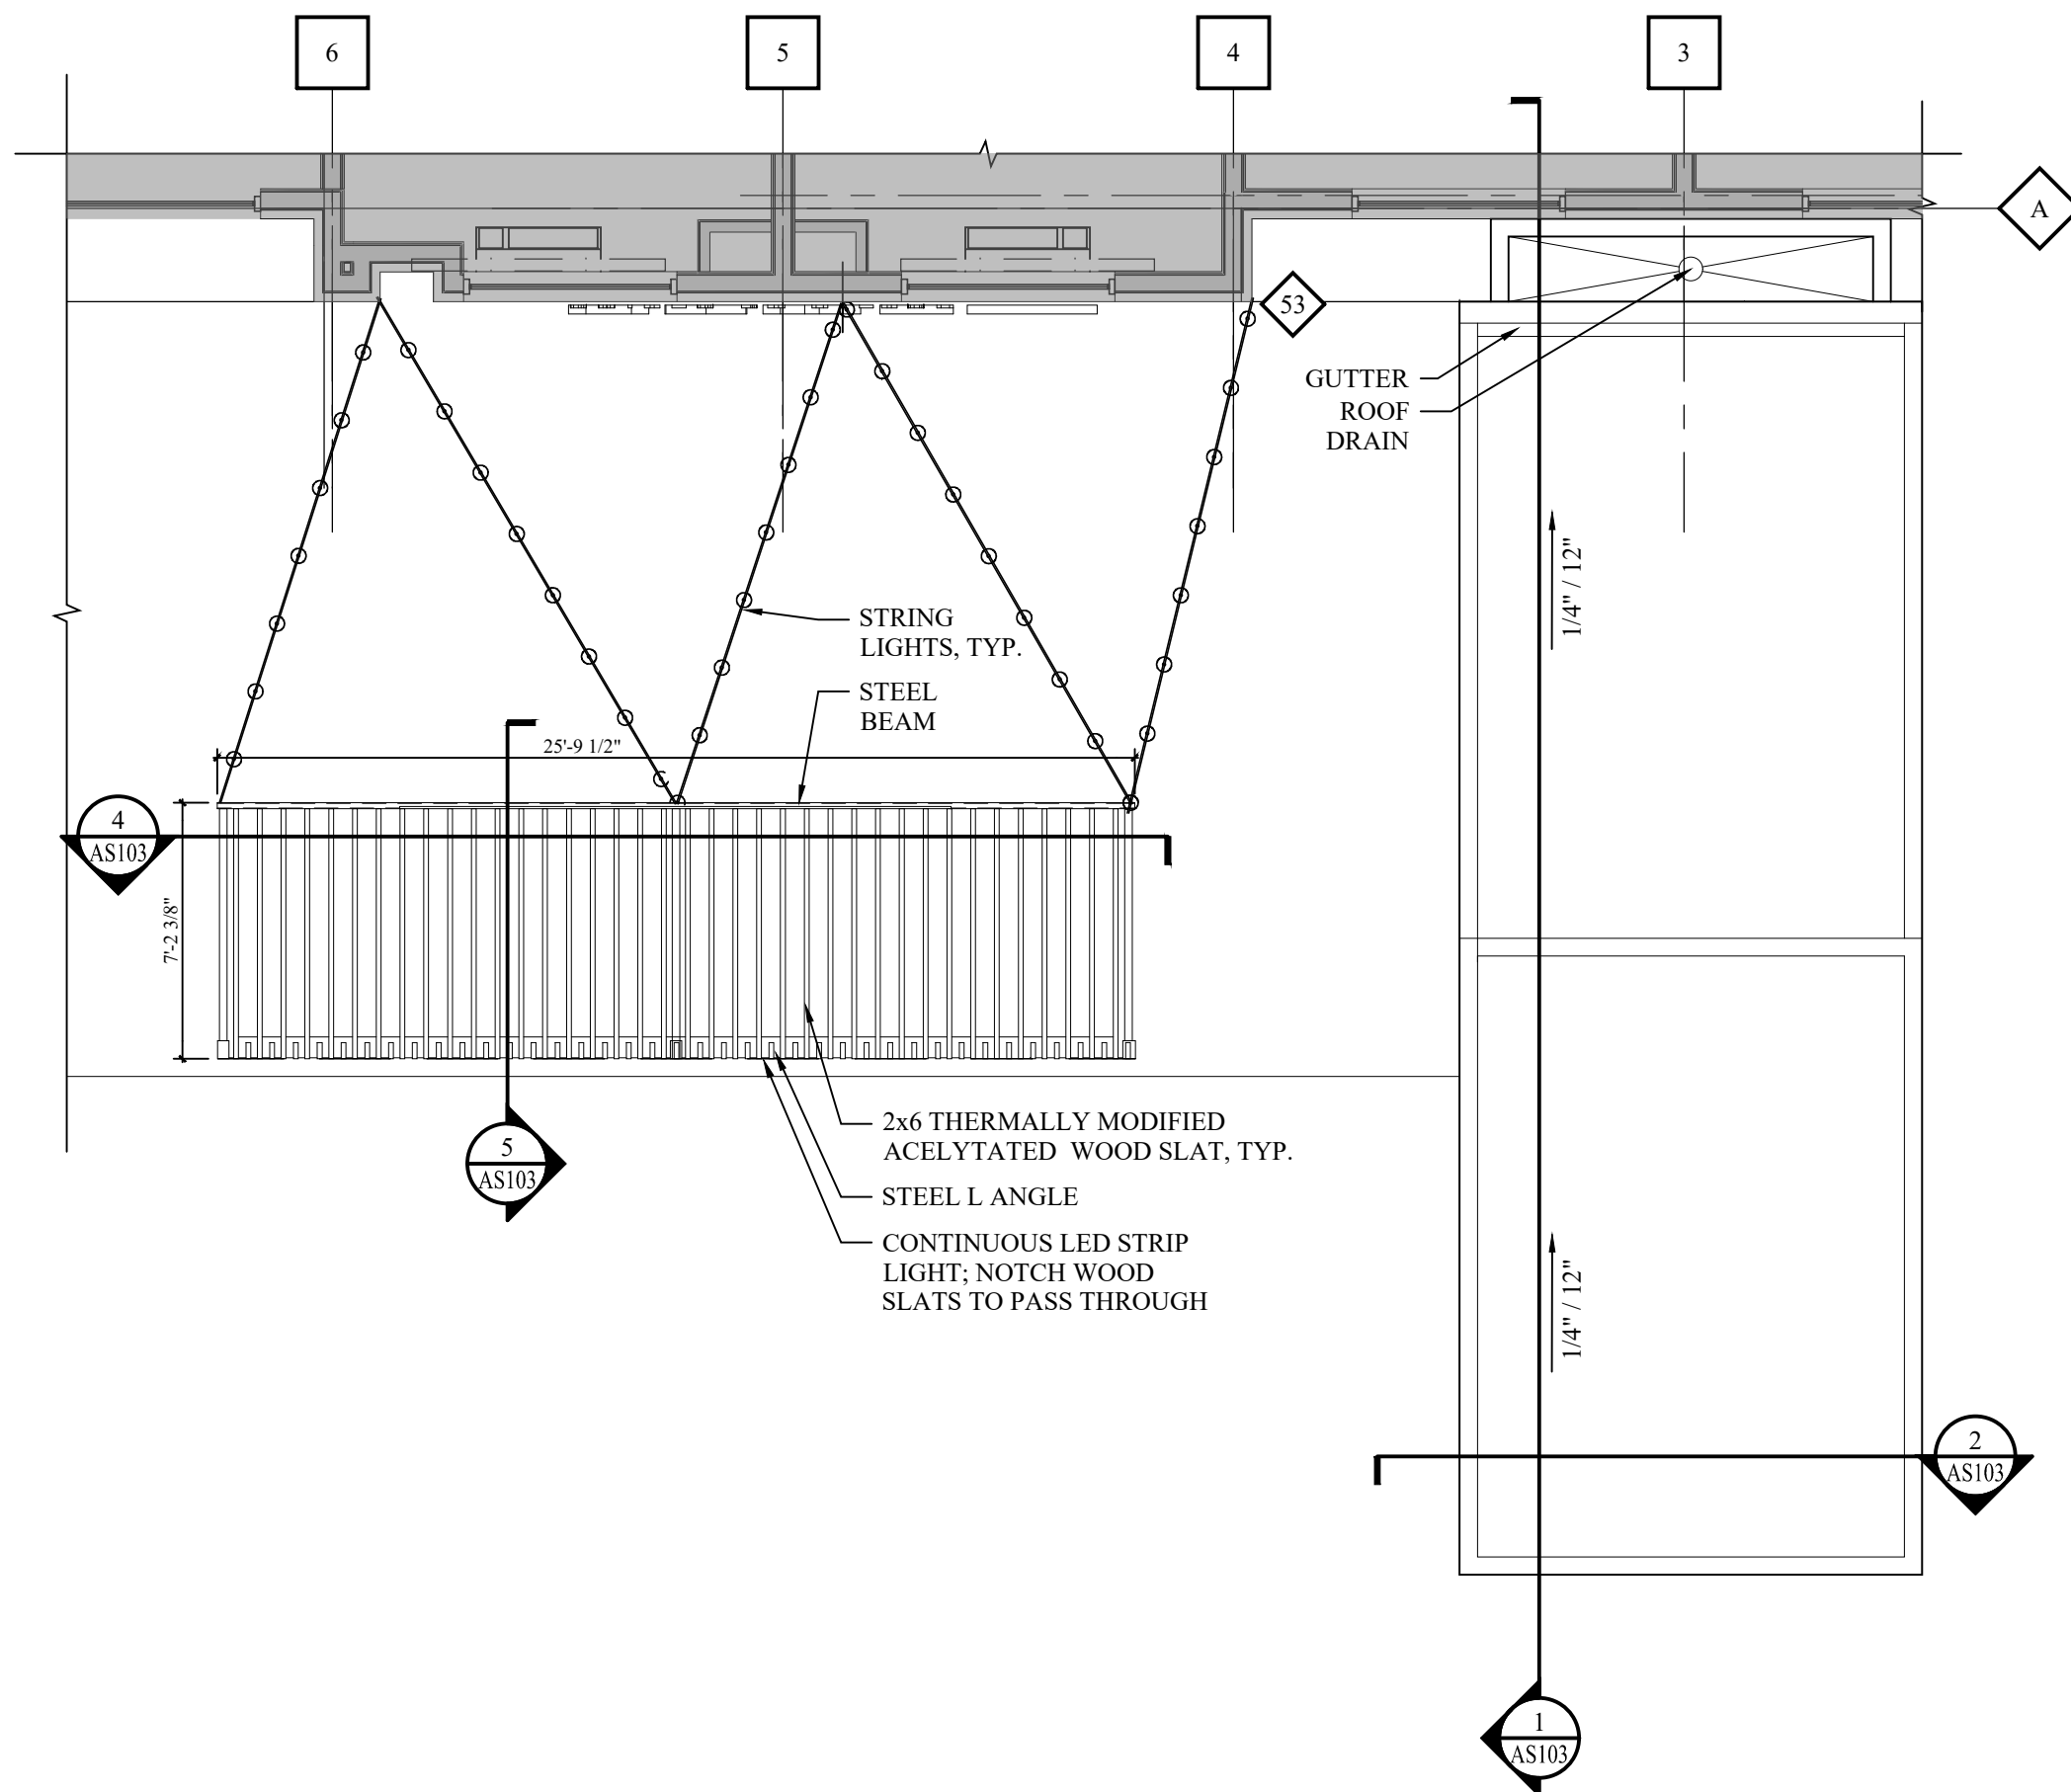


4 **ENLARGED PLAN - CANOPY AND TRELLIS**
3/16" = 1'-0"

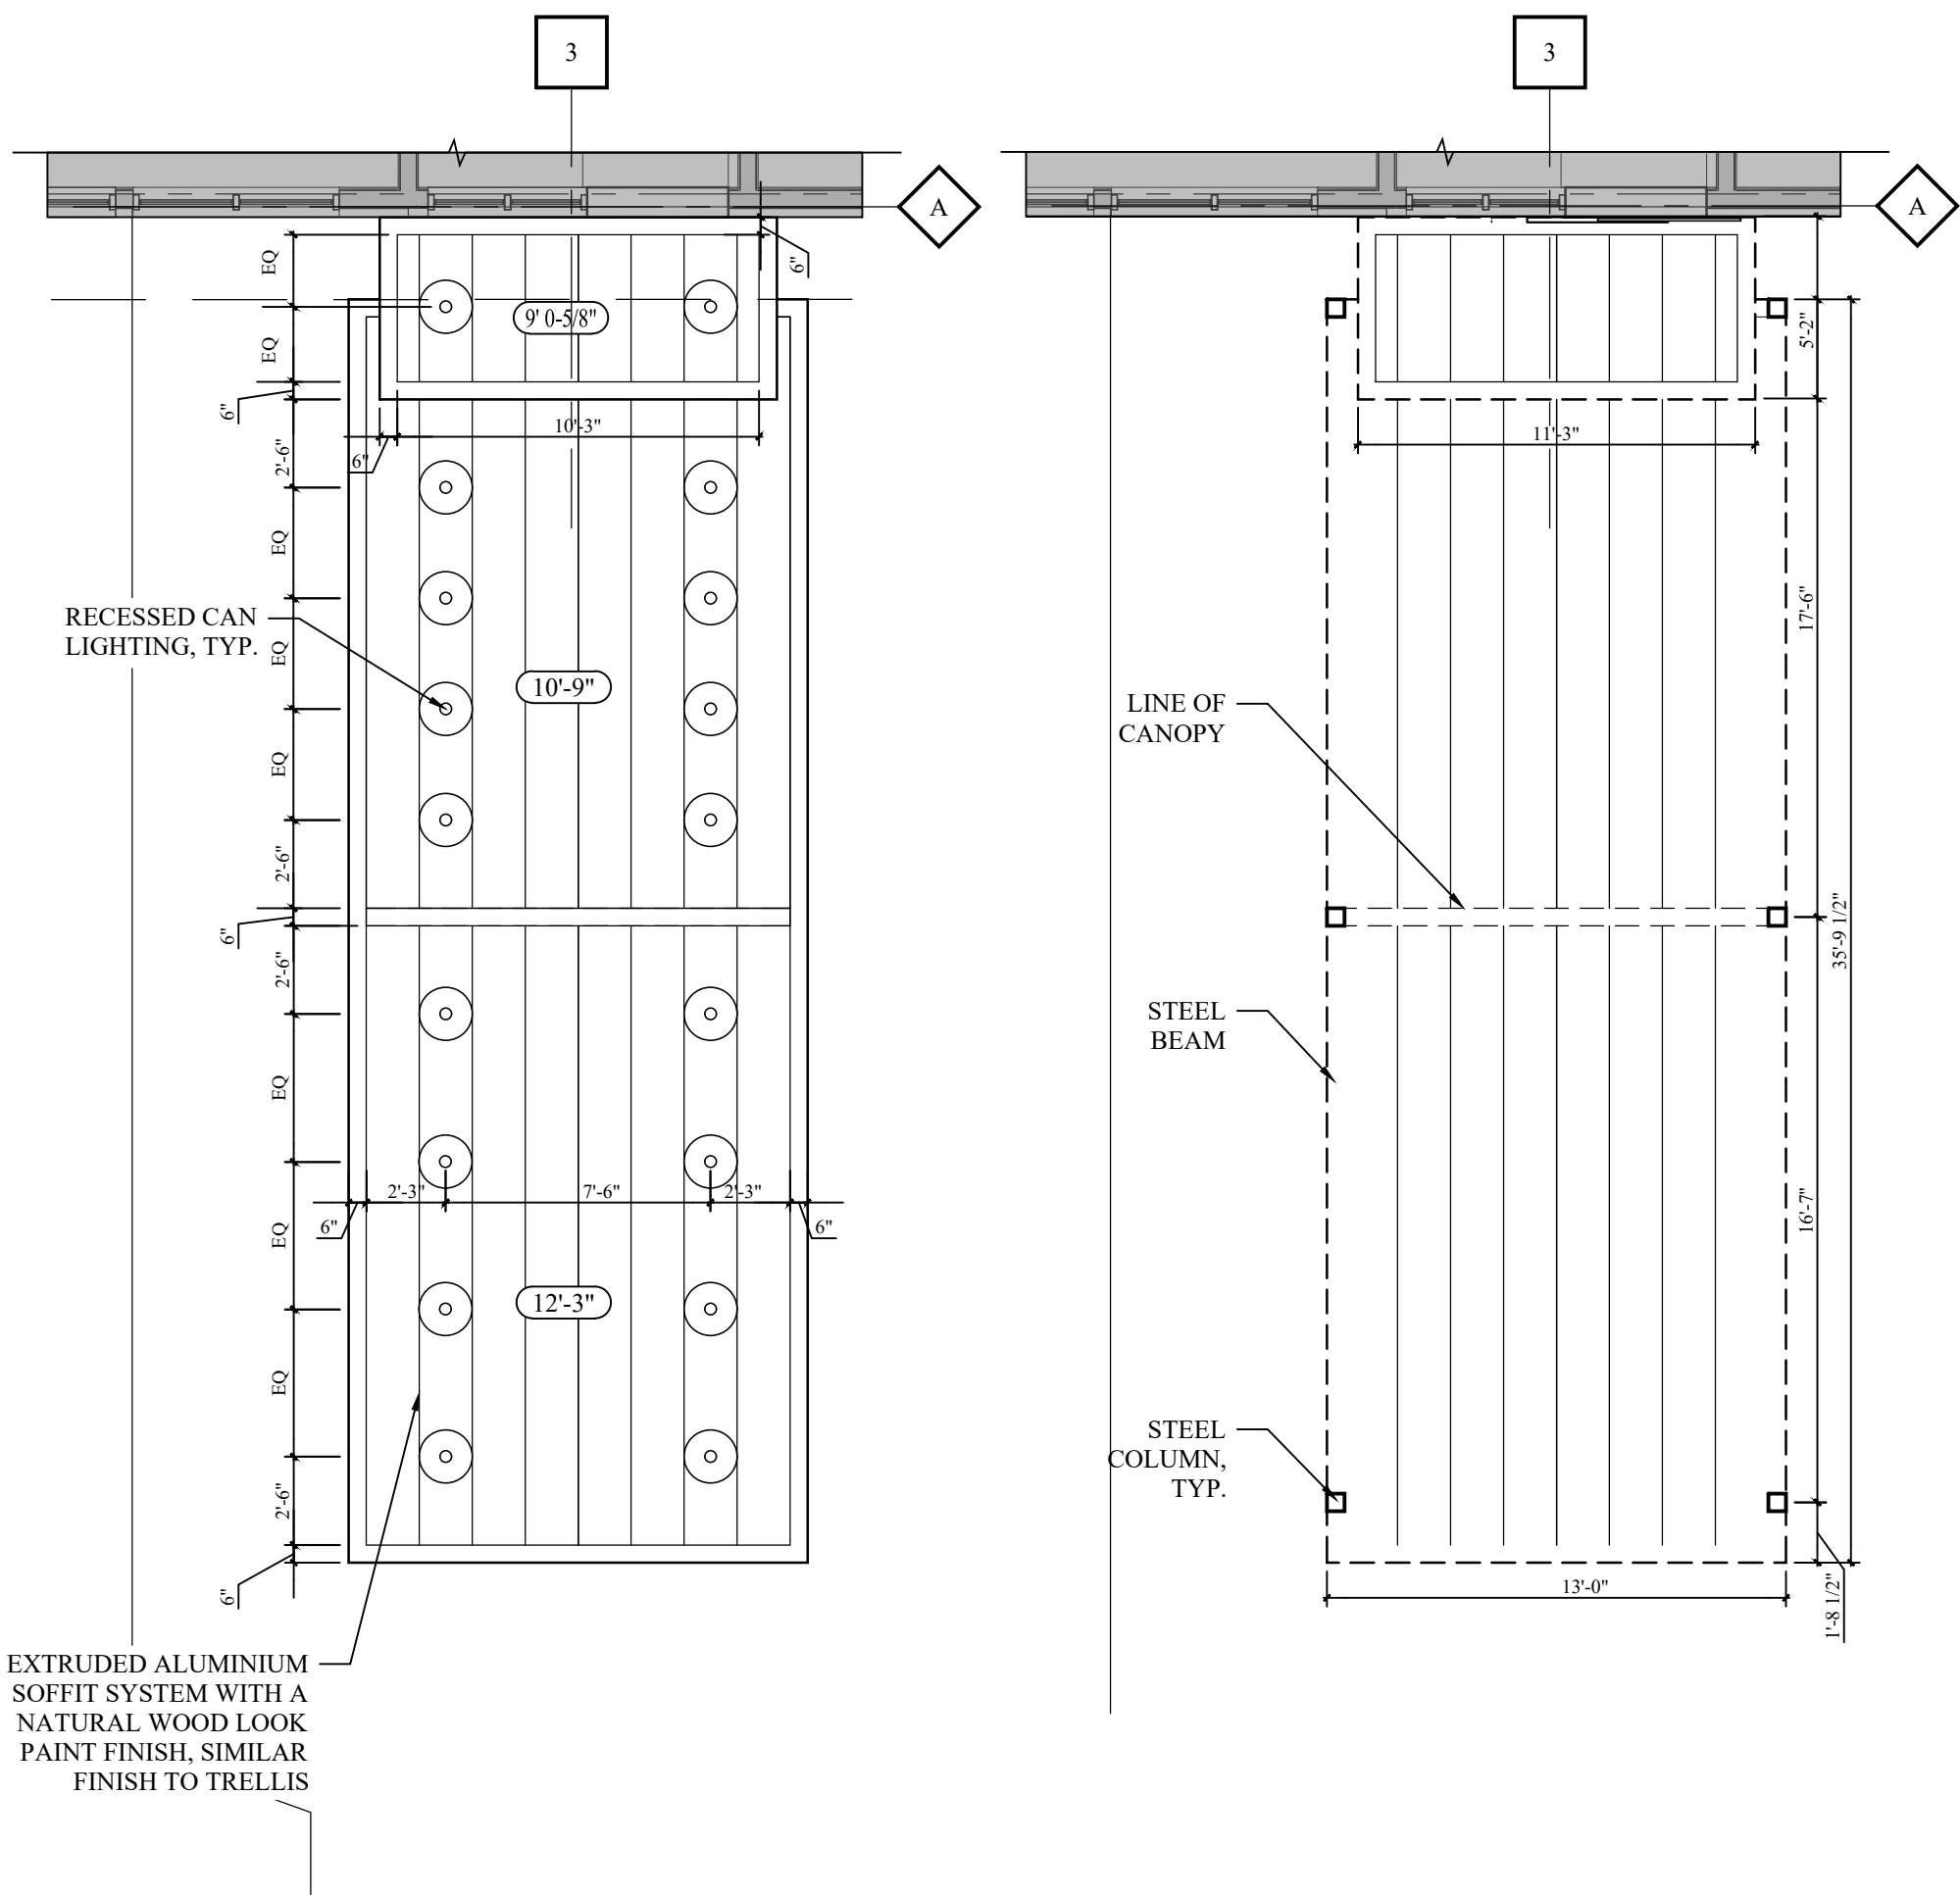

3 **CANOPY - RCP PLAN**
3/16" = 1'-0"

2 **CANOPY - ARCH. PLAN**
3/16" = 1'-0"

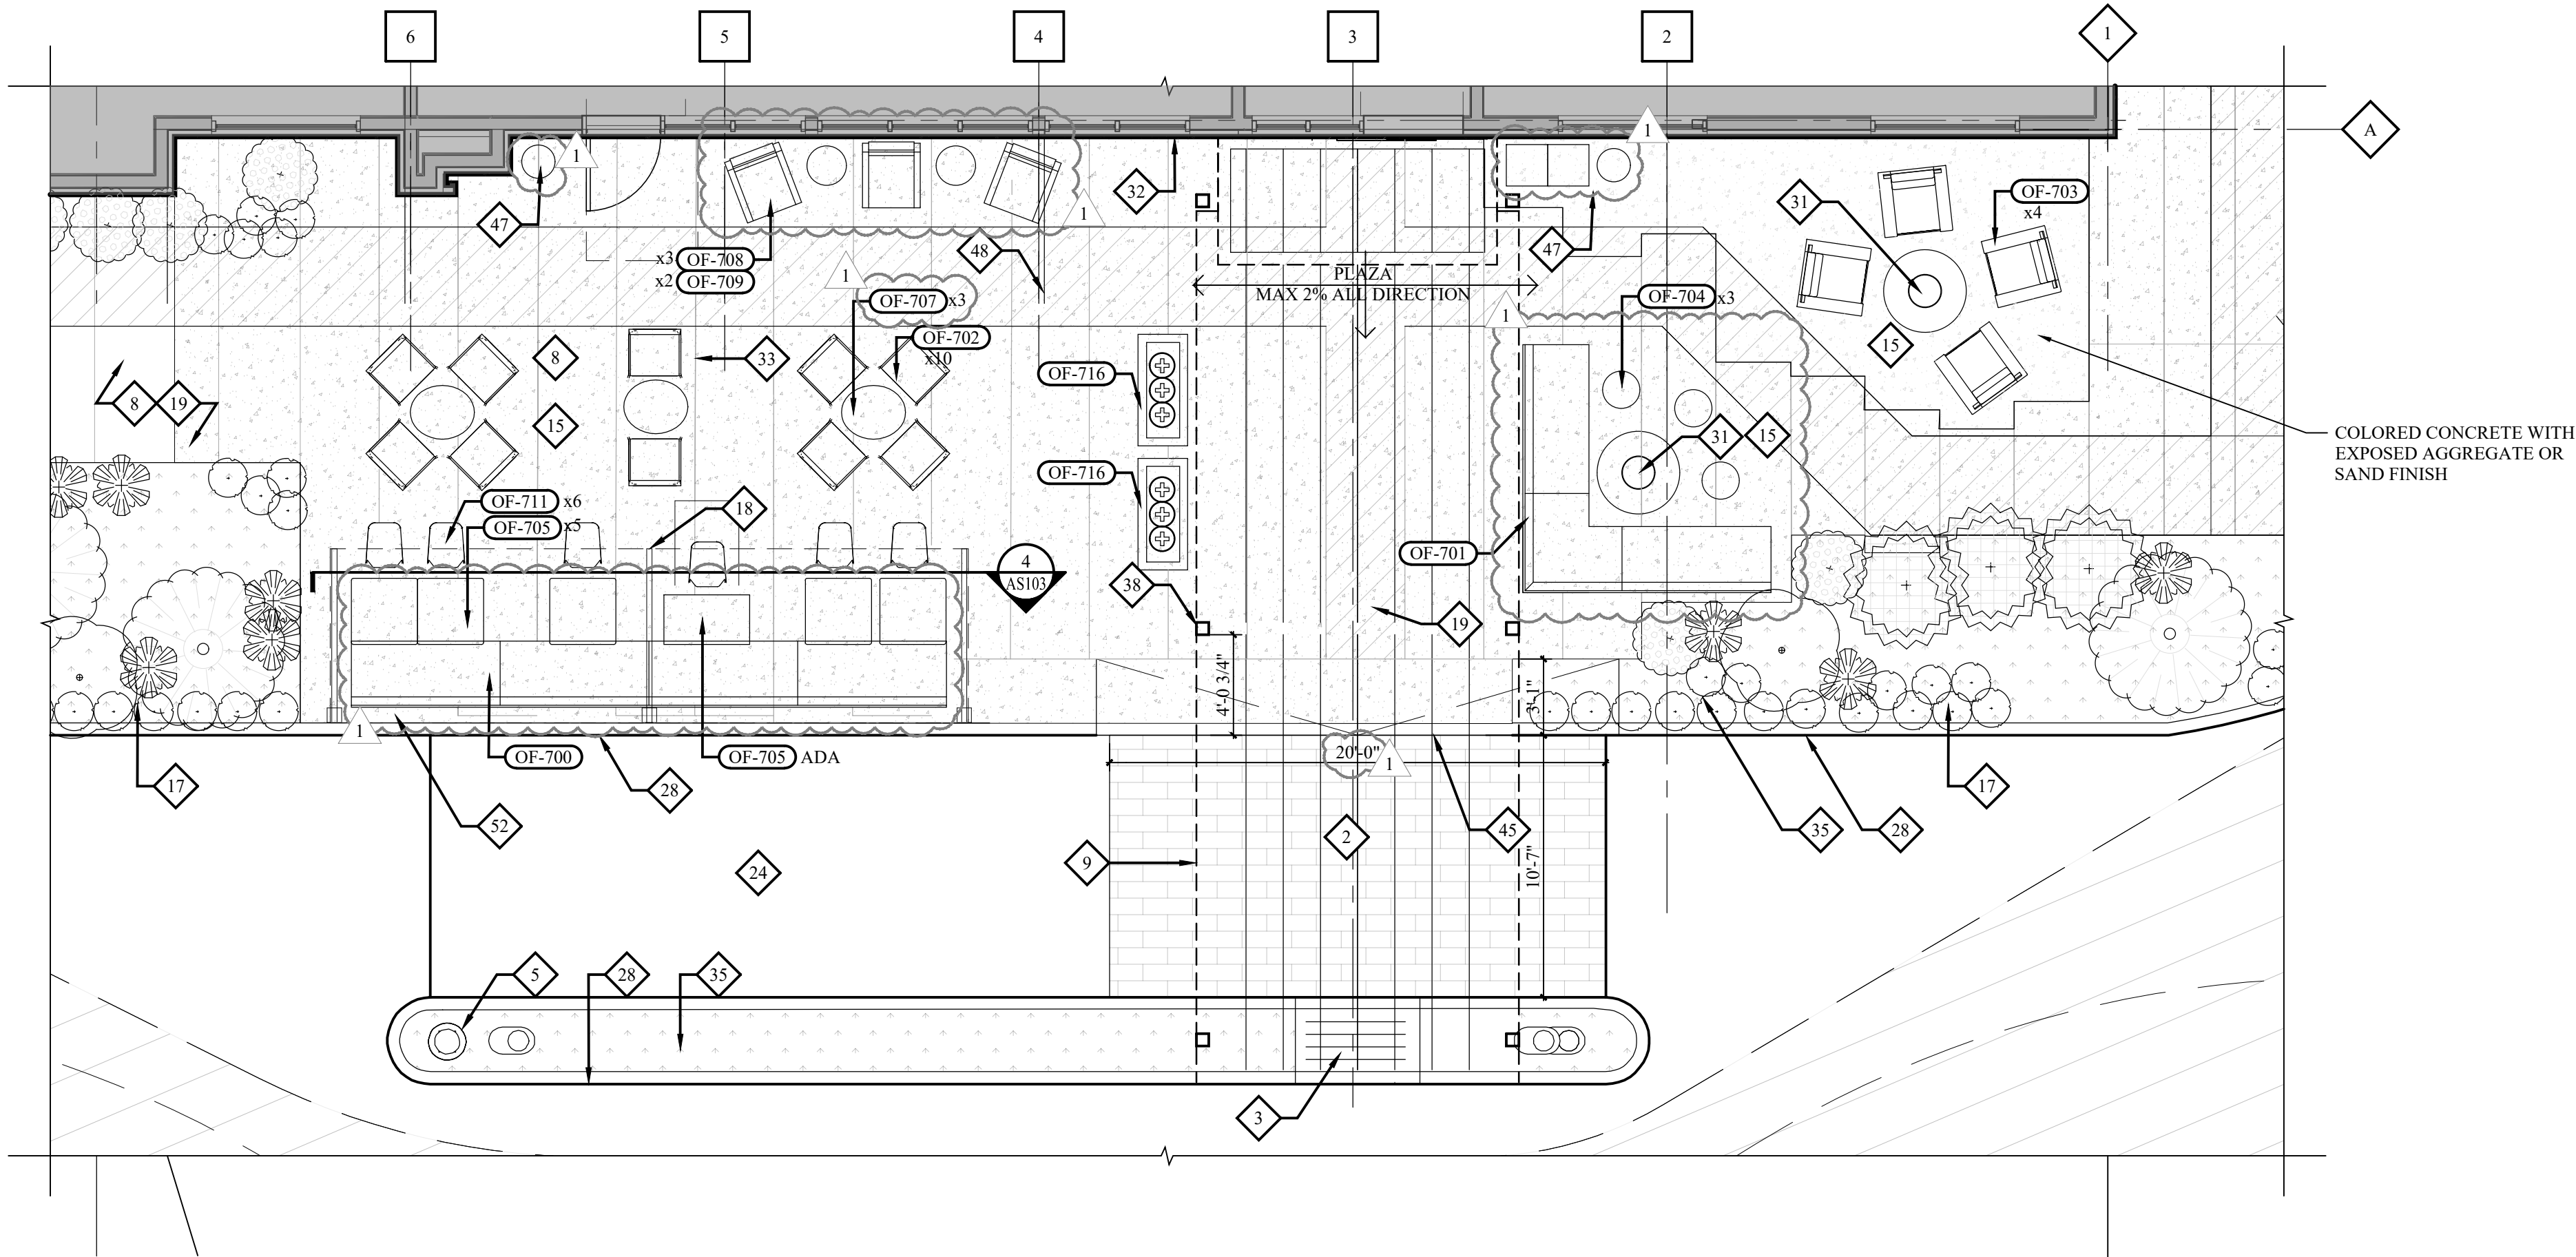

1 **ENTRANCE/DROP OFF CANOPY & OUTDOOR LOUNGE PLAN**
3/16" = 1'-0"

IMPORTANT NOTICE TO ALL CONTRACTORS AND OR SUBCONTRACTORS: (COMPLETE BUILDING SYSTEMS AND OR INSTALLATIONS)

IF AWARDED A CONTRACT FOR ANY PORTION OF WORK NEEDED TO COMPLETE THIS PROJECT YOU ARE AGREEING TO THE FOLLOWING TERMS:

- YOU ARE A QUALIFIED CONTRACTOR AND/OR SUBCONTRACTOR SPECIFICALLY IN PROVIDING A COMPLETE TURNKEY SERVICE IN YOUR TRADE OR PROFESSION FOR THE TYPE OF WORK AND SCOPE FOR THIS PROJECT.
- YOU AGREE TO PROVIDE A COMPLETE DESIGN BUILD SOLUTION BASED ON THE ARCHITECT'S INTENDED DESIGN FOR THIS PROJECT.
- YOUR BID INCLUDES ALL THE STEPS, PROCESSES, MATERIALS, PRODUCTS, GOVERNING PERMITS AND APPROVALS NECESSARY TO PROVIDE A COMPLETED AND WARRANTED SYSTEM OR INSTALLATION THAT DOES NOT REQUIRE ANOTHER CONTRACTOR OR PRODUCT TO COMPLETE YOUR SCOPE OF WORK.
- YOUR BID MUST HAVE INCLUDED ANY DESIGN INFORMATION REFERENCED WITHIN ANY CIVIL, ARCHITECTURAL, STRUCTURAL, MECHANICAL, ELECTRICAL AND OR PLUMBING DRAWINGS; ALSO NOTE THESE DRAWINGS ARE SCHEMATIC AND ARE INTENDED TO SHOW ONLY BASIC CONCEPTS AND GENERAL INFORMATION. THE COMPLETION OF YOUR WORK MAY INCLUDE OTHER STEPS, PROCESSES, MATERIALS, PRODUCTS, LABOR, GOVERNING PERMITS AND OR APPROVALS NECESSARY TO PROVIDE A COMPLETE SYSTEM INSTALLATION WHETHER SUGGESTED ON THE DRAWINGS OR NOT AS AN EXAMPLE; ITEMS AND OR TASKS LIKE: FIRE CAULK, DRAFT STOPS, FASTENERS, ANCHORS, EMBEDMENTS, DUMPS/STOPS, DEBRIS CLEAN UP, ETC. ARE YOUR RESPONSIBILITY. ANY WORK NOT COMPLETED IN A TIMELY MANNER, OR INCOMPLETE WORK WILL BE BILLED BACK TO THE CONTRACTOR AND OR SUBCONTRACTOR, AT THE OWNERS' DISCRETION.
-

KEYED NOTES		
1	MONUMENT SIGN LOCATION	
2	ACCESSIBLE PASSENGER DROP OFF AREA W/ ADJACENT CLEAR ACCESS AISLE - DROP OFF AND ACCESS AISLE SHALL BE AT THE SAME LEVEL & SHALL HAVE A SLOPE NOT TO EXCEED 1:48 (1:64 RECOMMENDED) - DRIVE AISLES SHALL RAMP UP TO LEVEL OF WALK AT DROP-OFF AREA - REFER TO MATERIAL LEGEND FOR SPECIFIC PAVING OF THIS AREA. REFER TO THE HADG FOR MORE INFORMATION REGARDING ACCESSIBLE PASSENGER LOADING ZONES.	
3	ACCESSIBLE CURB RAMP TO MEET ALL ACCESSIBILITY REQUIREMENTS, MAXIMUM SLOPE OF RUN 1:12 (1:14 RECOMMENDED), MAXIMUM CROSS SLOPE OF 1:48 (1:64 RECOMMENDED), REFER TO THE HADG FOR FURTHER INFORMATION.	
4	ACCESSIBLE PARKING SPACES, SIGNAGE, LOGOS, WHEEL STOPS AND ACCESS AISLES - MUST MEET ALL ACCESSIBILITY REQUIREMENTS - PROVIDE SPACES IN SIZE, QUANTITY AND LOCATIONS REQ'D BY ACCESSIBILITY AND BY APPLICABLE CODES AS DETERMINED BY LOCAL JURISDICTION. PROVIDE A MAXIMUM SLOPE IN EITHER DIRECTION OF 1:48 (1:64 RECOMMENDED), REFER TO HADG FOR FURTHER INFORMATION.	
5	OPTIONAL FLAG POLE WITH IN-GROUND UPLIGHT	
6	SPECIMEN TREE	
7	PAVED WALKWAY - SLOPE AWAY FROM BLDG. (MAX 2% CROSS SLOPE) - SILICA-BASED AGGREGATE	
8	DECORATIVE NON-SLIP PAVING	
9	LINE OF CANOPY ROOF ABOVE	
10	REINFORCED CONCRETE PAD	
11	EXTERIOR GARDEN STORAGE AREA	
12	PET RELIEF STAND	
13	PROPERTY LINE	
14	CURB CUT & DRIVEWAY ACCESS - SIZE & LOCATE CURB CUTS & DRIVE AISLES PER LOCAL REQUIREMENTS - MAINTAIN APPROPRIATE SIGHT LINES	
15	OUTDOOR LOUNGE - REFER TO FF&E SPEC'S FOR LOOSE FURNISHINGS	
16	POOL PATIO - REFER TO FF&E SPEC'S FOR LOOSE FURNISHINGS	
17	ACCENT PLANTINGS - SPECIES DETERMINED BY LOCAL CLIMATE CONDITIONS - REFER TO LANDSCAPE DESIGN INTENT PLAN FOR LANDSCAPING GUIDELINES	
18	TRELLIS ABOVE - SEE DETAILS SHEET A-305	
19	ACCESSIBLE ROUTE FROM ACCESSIBLE PARKING TO BUILDING ENTRANCE. PROVIDE A RUNNING SLOPE OF MAXIMUM 1:20 AND A CROSS SLOPE OF MAXIMUM 1:48 (1:64 RECOMMENDED), REFER TO HADG FOR FURTHER INFORMATION.	
20	BOLLARDS - 48" HIGH 6" DIA. CONC. FILLED STL.	
21	PROPOSED TRANSFORMER & CONCRETE PAD LOCATION - ADJUST LOCATION AS REQUIRED TO MEET LOCAL CODES & UTILITY ACCESS	
22	PARKING LOT STRIPING MUST BE WHITE, EXCEPT WHERE OTHER COLORS ARE REQUIRED BY LOCAL CODES FOR FIRE LANES, ACCESSIBLE PARKING, NO PARKING ZONES, ETC.	
23	TREES - SPECIES DETERMINED BY LOCAL CLIMATE CONDITION - TREES SHALL NOT INTERFERE WITH PARKING OR PEDESTRIAN ACTIVITY - REFER TO LANDSCAPE DESIGN INTENT PLAN FOR LANDSCAPING GUIDELINES.	
24	ASPHALT OR CONC. PAVING SHALL COMPLY WITH LOCAL REQUIREMENTS - PROVIDE POSITIVE DRAINAGE AWAY FROM BUILDING. COORDINATE SITE DRAINAGE & DETENTION WITH CIVIL ENGINEER.	
25	PARTIAL HEIGHT WALL	
26	ACCESSIBLE WALKWAY: RUNNING SLOPE OF MAXIMUM 1:20 AND CROSS SLOPE OF MAXIMUM 1:48 (1:64 RECOMMENDED), REFER TO HADG FOR FURTHER INFORMATION. SCORE DECORATIVE CONC.	
27	CONTINUOUS CONCRETE CURB - TYP.	
28	CONDENSING UNIT LOCATION - SCREENED FROM VIEW	
29	ACCESSIBLE PATH AWAY FROM BUILDING	
30	EXTERIOR FIRE PIT WITH MANUAL EMERGENCY REMOTE SHUT-OFF VALVE. SECURE IN PLACE TO RESIST MOVEMENT. FEED WITH UNDERGROUND LINE FROM BUILDING GAS SERVICE. PROVIDE APPROPRIATELY SIZED SAFETY SCREEN.	
31	EXPANSION JOINT	
32	CONTROL JOINT	
33	LANDSCAPE AREA - REFER TO LANDSCAPE SHEETS FOR PLANTING PLAN	
34	REFER TO FLOOR PLANS FOR HATCHED AREA	
35	PRIMED AND PAINTED TUBE STEEL CANOPY COLUMNS	
36	ACCESSIBLE ROUTE TO PUBLIC RIGHT OF WAY (1 REQUIRED), MAX. RUNNING SLOPE OF 1:20 AND MAX. CROSS SLOPE OF 1:48 (1:64 RECOMMENDED). ALL PAVED SURFACES, CURB RAMPS & TRANSITIONS ALONG PATH TO MEET ACCESSIBILITY REQ'S	
37	EXTERIOR GAS GRILL. GRILLS REQUIRE REMOTE EMERGENCY SHUT OFF.	
38	PARKING LOT & DRIVEWAY LIGHTING (P-1) - SHOWN FOR DESIGN INTENT	
39	FLUSH CURB ALONG ENTIRE LENGTH OF ACCESSIBLE DROP OFF	
40	TRASH, RECYCLING, AND ASH BIN	
41	24" X 54" FRC PLANTERS	
42	OPTIONAL POOL	
43	EV CHARGING STATION. PROVIDE CONCRETE FOOTING AND ELECTRICAL.	
44	EMERGENCY GAS SHUT OFF	
45	PROVIDE POWER FOR PLUG IN STRIP LIGHT AT TRELLIS	
46	PROVIDE POWER FOR PLUG IN STRING LIGHTS	

MWT

3827 BILLO ROAD
ALDEN, NY, 14004
716-631-0600
ARCHITECT OF RECORD

DONALD M. EDWARD
LICENSE # 20212
10800 ALABASTER DR.
DAVIDSON, NC 28036
donedwardarchitect@gmail.com

04/20/2023

WARNING
IT IS A VIOLATION OF THE LAW FOR ANY PERSON, UNLESS ACTING UNDER THE DIRECTION OF THE ARCHITECT OR ENGINEER, TO ALTER OR REPRODUCE THESE DRAWINGS IN ANY WAY.

DRAWING QUESTIONS
CA@MWTUSA.COM
1-800-717-5816

ISSUED FOR :
CONSTRUCTION AND BID SET

HOME2
SUITES BY HILTON

EAGLE PASS, TX 78852
PROTOTYPE VERSION: 3.0

REVISIONS		
NO.	DESCRIPTION	DATE BY
1	FF&E FRANCHISE UPDATE	08/04/23 -

PROJECT NO.: 22-014

DATE: 06/09/23

DRAWN BY: YA/AA/RH/BS

CHKD. BY: AS

ENLARGED
PORTE COCHERE
& OUTDOOR LOUNGE

SHEET
AS102

22-014-AS102-ASH ENLARGED PORTE COCHERE & OUTDOOR LOUNGE.dwg