



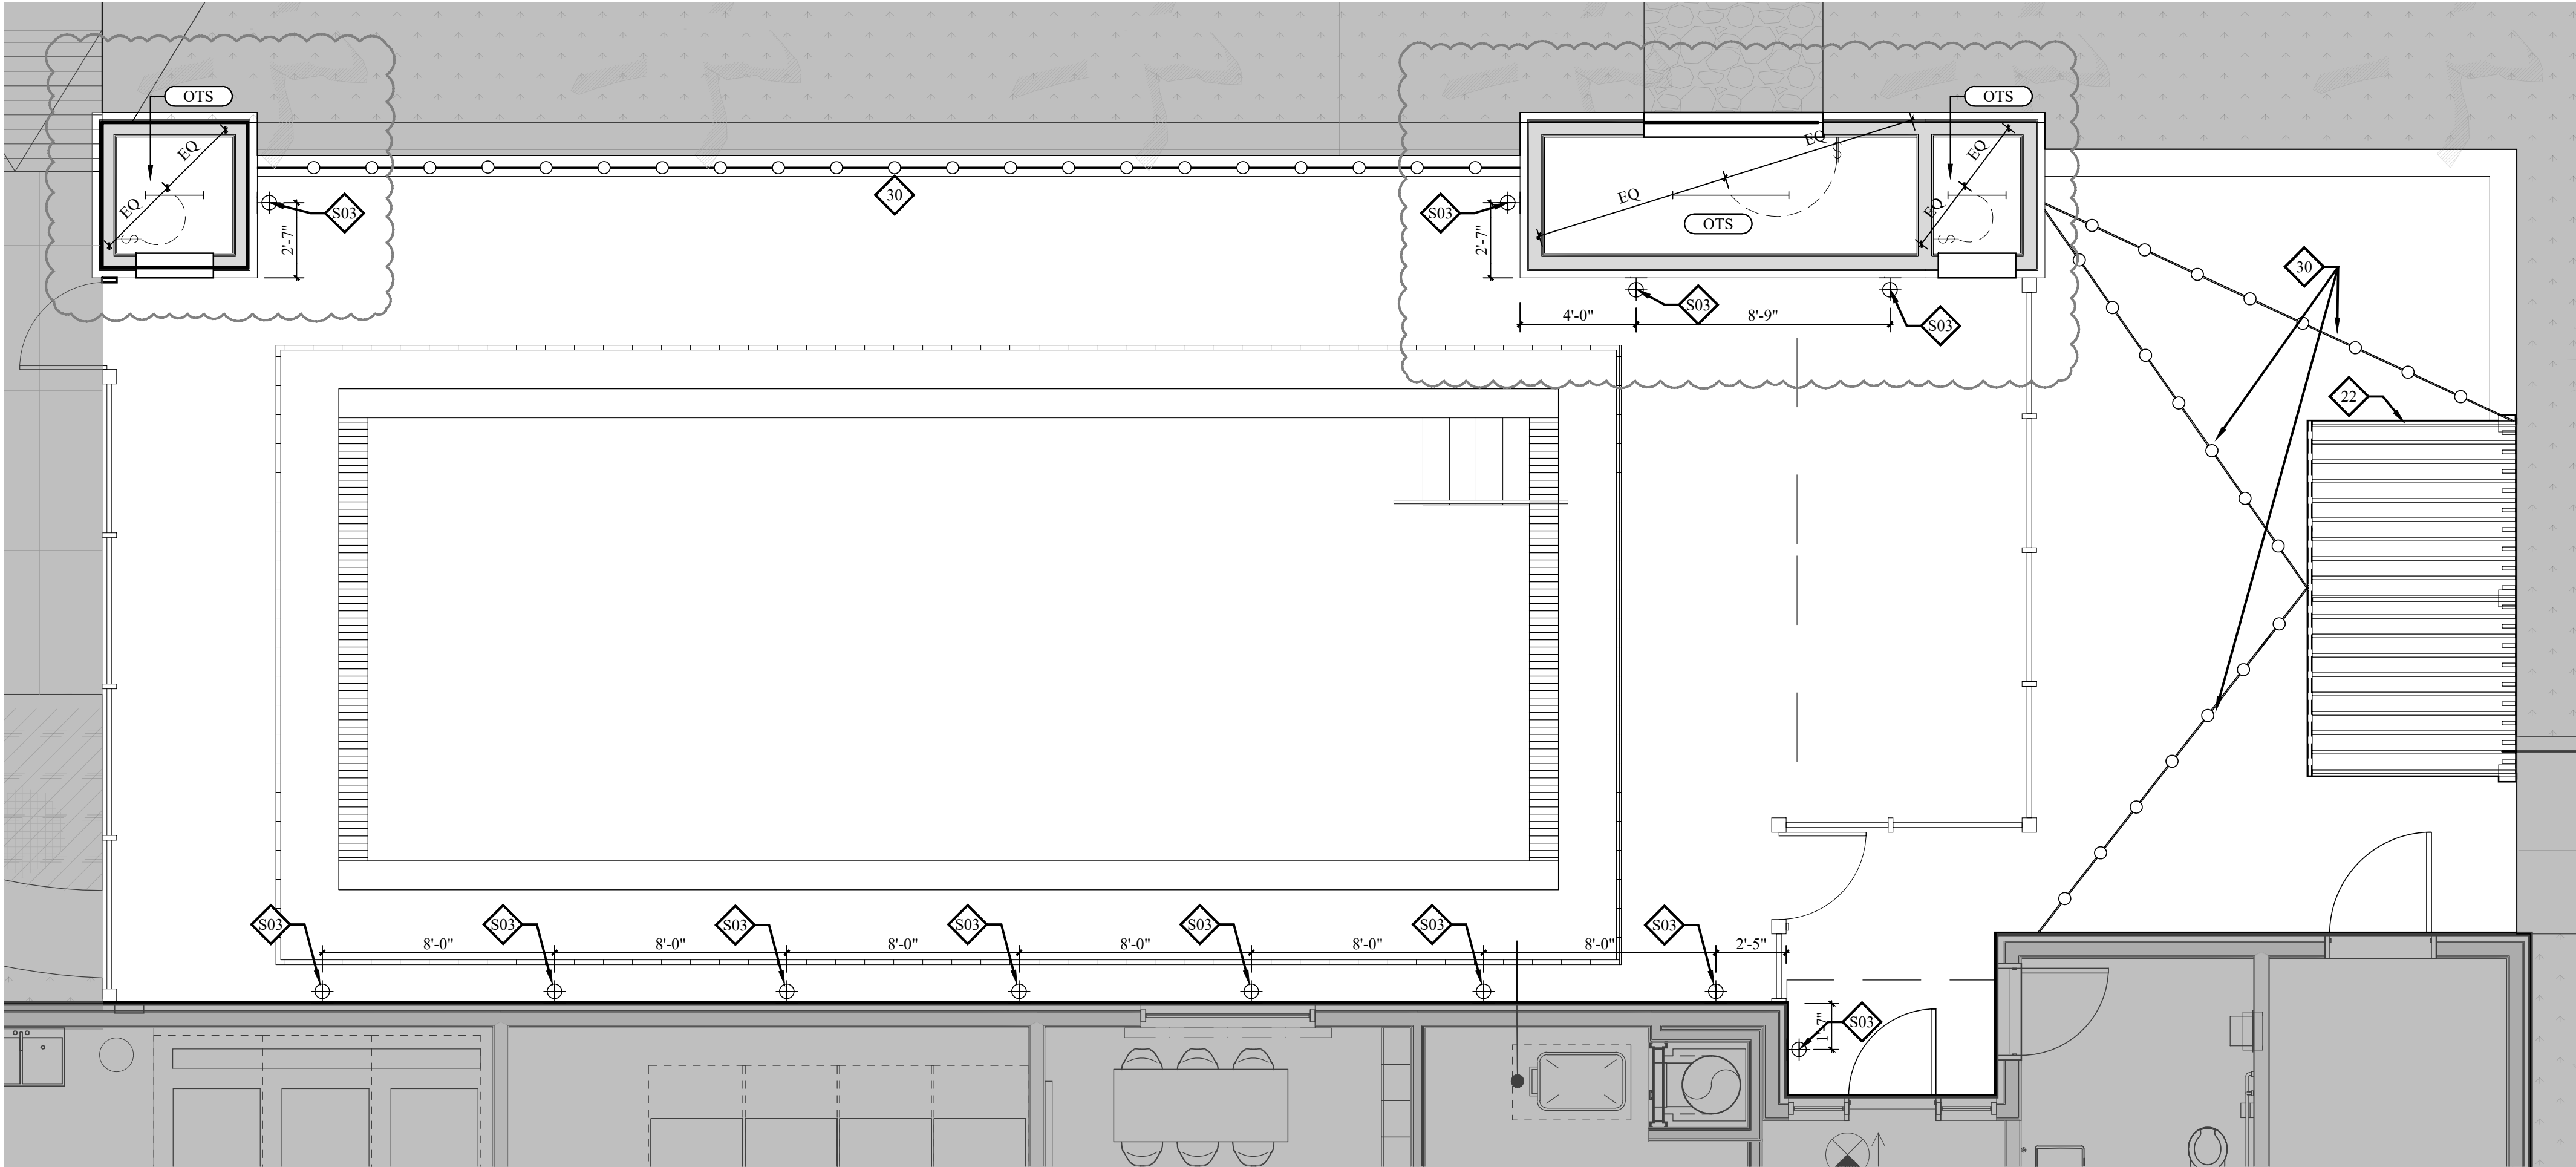

2 ENL. OUTDOOR POOL - REFLECTIVE CEILING PLAN
1/4" = 1'-0"

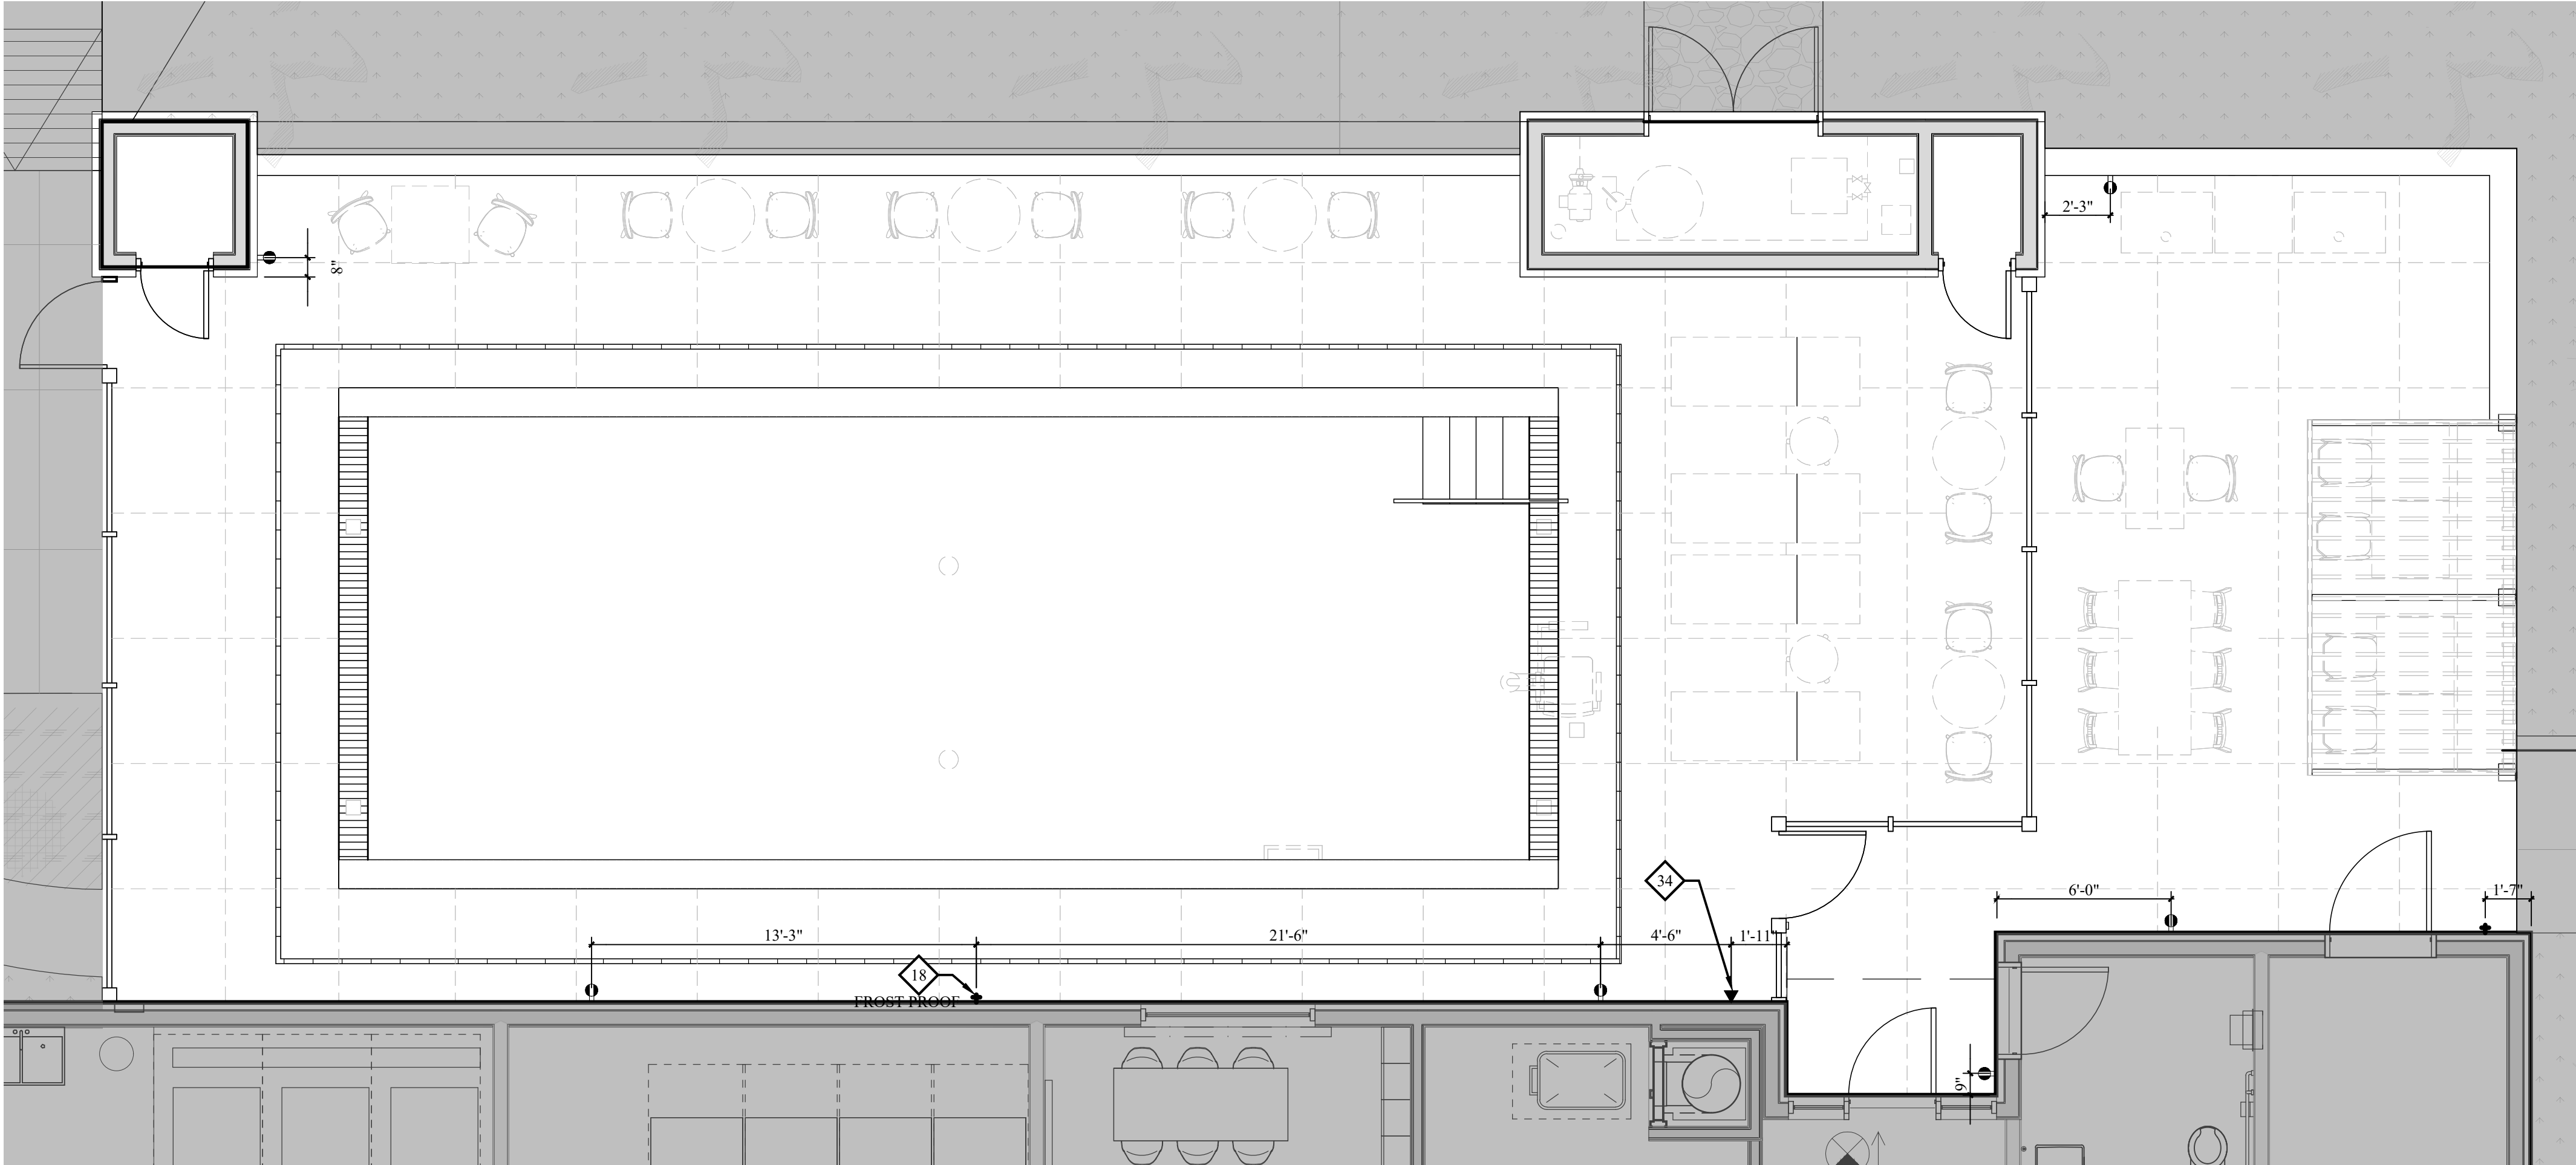

1 ENL. OUTDOOR POOL - POWER PLAN
1/4" = 1'-0"

LEGEND - CEILING FIXTURES


SYMBOL	DESIGNATION	DESCRIPTION
	W	WALL SCONCE
	L	SURFACE LINEAR STRIP

LEGEND - ELECTRICAL FIXTURE

PLAN	DESCRIPTION
	OUTLET - DUPLEX
	OUTLET - DUPLEX - GFI
	PHONE
	LIGHT SWITCH


KEYED NOTES - POOL

1	FLUSH MOUNT SPEAKER RATED FOR DAMP ENVIRONMENTS
2	STAINLESS STEEL HANDRAIL TO COMPLY WITH ACCESSIBILITY REQUIREMENTS
3	PROVIDE A FIXED POOL LIFT TO PROVIDE AN ACCESSIBLE MEANS OF ENTRY TO THE POOL. PROVIDE LIFT LOCATION TO COMPLY W/ ACCESSIBILITY STANDARDS. REFER TO HADG FOR FURTHER REQ'S
4	STAIR ENTRY TO POOL TO COMPLY WITH ACCESSIBILITY REQUIREMENTS
5	SWIMMING POOL
6	JOINTS WHERE THE DECK MEET THE POOL MUST BE WATERTIGHT
7	STAINLESS STEEL HVAC DUCT
8	FLUSH BOX HYDRANT
11	NOT USED
12	POOL DEPTH MARKERS AS REQUIRED BY CODE, INSET FLUSH WITH POOL COPING. DECK LOCATION ALSO INDICATES CORRESPONDING POOL WALL TILE LOCATION, DECK AND WALL TILES TO BE ALIGNED. POOL CONTRACTOR TO VERIFY POOL DEPTHS PRIOR TO INSTALLING TILES
13	POOL BOTTOM DRAIN
14	POOL EQUIPMENT
15	POOL CHEMICAL CLOSET - EVERYTHING IN THIS ROOM TO BE RATED FOR CORROSIVE ENVIRONMENTS (DOOR, DOOR FRAME AND HARDWARE, PIPES, PIPE SUPPORTS, SHELVES, LIGHTS, ETC.)
16	LADDER
17	BRICK COPING AT PERIMETER OF POOL
18	TAMPER RESISTANT, RECESSED HOSE BIBB - MOUNT TOP AT +12" A.F.F
19	SLOPE POOL DECK TOWARD AREA DRAIN EXTEND WATERPROOFING OVER STRUCTURAL SLAB AND INTO LOWER BODY OF DRAIN. SLOPE OF POOL DECK NOT TO EXCEED 1:48 (1:64 RECOMMENDED) IN EITHER DIRECTION PER ACCESSIBILITY REQUIREMENTS
20	DRINKING FOUNTAINS: LEADING EDGES OF BOTH ACCESSIBLE AND NON-ACCESSIBLE FOUNTAIN SHOULD BE NO HIGHER THAN 27" PER ACCESSIBILITY. REQUIREMENTS.
21	SURFACE MOUNTED DOWNLIGHT -- RUN EXPOSED SUPPLY CONDUIT UP TIGHT AGAINST CORNER OF DECKING AND BEAM TO MINIMIZE SIGHT LINES
22	PRIMED AND PAINTED TUBE STEEL - WITH MODIFIED WOOD TRELLIS INFILL - SYSTEM TO BE LIGHTED BY LINEAR TUBE LIGHT
23	UNDERWATER LIGHTING - WATTAGE PER LOCAL CODE
24	DECKS MUST BE INSTALLED W/ RELIEF JOINTS FOR THERMAL MOVEMENT & POTENTIAL SETTLING
25	PROVIDE CONT. VAPOR BARRIER BEHIND POOL CEILING FINISH
27	EDGE OF POOL BELOW DASHED IN FOR REFERENCE
28	SLOPE CONCRETE DECK AWAY FROM BUILDING. SLOPE OF POOL DECK NOT TO EXCEED 1:48 (1:64 RECOMMENDED) IN EITHER DIRECTION PER ACCESSIBILITY REQUIREMENTS
29	WALL RETURN GRILLE -- REFER TO ELEVATIONS
30	EXTERIOR LIGHT STRING -- ENSURE THAT ADEQUATE BLOCKING IS PROVIDED FOR STRING LIGHTS
31	PROVIDE POWER FOR PLUG IN STRING LIGHTS
32	ROOF MOUNTED EXHAUST FAN GRILLE
33	EXPANSION JOINT IN COPING 10" MAX SEPARATION
34	HOUSE PHONE LOCATION
35	JOINTS WHERE THE POOL OR WHIRLPOOL COPING MEETS THE DECK MUST BE PROTECTED FROM THE RELATIVE PRESSURE OF ADJOINING DECK MOVEMENT
37	FIRE EXTINGUISHER (CABINET IN PUBLIC AREAS); INSTALLED SO THAT NO OPERABLE PART IS HIGHER THAN 48" A.F.F.
38	EMERGENCY TELEPHONE OR BUTTON LOCATION. REFER TO STANDARDS
39	INDOOR POOL RECEIVE TILE
40	FLOOR DRAIN WITH TRAP PRIMER IN DISHED RECESS
41	DRAIN OPENINGS TO BE PERPENDICULAR TO THE DIRECTION OF TRAVEL AND BE LESS THAN 1/2" WIDE. DRAIN WITH TRAP PRIMER
43	POOL PERIMETER FENCE AS REQUIRED BY CODE 3'-0" GATE
44	DIRECT ATTACHED TECTUM CEILING PANELS
45	PROVIDE KEY CARD ENTRY FOR DOOR
52	PROVIDE POWER FOR PLUG IN STRIP LIGHT AT TRELLIS

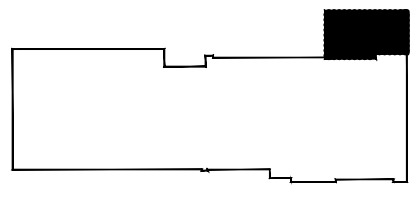

IMPORTANT NOTICE TO ALL CONTRACTORS AND OR SUBCONTRACTORS: (COMPLETE BUILDING SYSTEMS AND OR INSTALLATIONS)

- IF AWARDED A CONTRACT FOR ANY PORTION OF WORK NEEDED TO COMPLETE THIS PROJECT YOU ARE AGREEING TO THE FOLLOWING TERMS:
- YOU ARE A QUALIFIED CONTRACTOR AND OR SUBCONTRACTOR SPECIFICALLY IN PROVIDING A COMPLETE TURNKEY SERVICE IN YOUR TRADE OR PROFESSION FOR THE TYPE OF WORK AND SCOPE FOR THIS PROJECT.
 - YOU AGREE TO PROVIDE A COMPLETE DESIGN BUILD SOLUTION BASED ON THE ARCHITECTS INTENDED DESIGN FOR THIS PROJECT.
 - YOUR BID INCLUDED ALL THE STEPS, PROCESSES, MATERIALS, PRODUCTS, GOVERNING PERMITS AND APPROVALS NECESSARY TO PROVIDE A COMPLETED AND WARRANTED SYSTEM OR INSTALLATION THAT DOES NOT REQUIRED ANOTHER CONTRACTOR OR PRODUCT TO COMPLETE YOUR SCOPE OF WORK.
 - YOUR BID MUST HAVE INCLUDED ANY DESIGN INFORMATION REFERENCED WITHIN ANY CIVIL, ARCHITECTURAL, STRUCTURAL, MECHANICAL, ELECTRICAL AND OR PLUMBING DRAWINGS; ALSO NOTE THESE DRAWINGS ARE SCHEMATIC AND ARE INTENDED TO SHOW ONLY BASIC CONCEPTS AND GENERAL INFORMATION. THE COMPLETION OF YOUR WORK MUST INCLUDE OTHER STEPS, PROCESSES, MATERIALS, PRODUCTS, LABOR, GOVERNING PERMITS AND OR APPROVALS NECESSARY TO PROVIDE A COMPLETE SYSTEM INSTALLATION WHETHER SUGGESTED ON THE DRAWINGS OR NOT.
 - AS AN EXAMPLE: ITEMS AND OR TASKS LIKE: FIRE CAULK, DRAFT STOPS, FASTENERS, ANCHORS, EMBEDMENTS, DUMPSTERS, DEBRIS CLEAN UP, ETC. ARE YOUR RESPONSIBILITY. ANY WORK NOT COMPLETED IN A TIMELY MANNER, OR INCOMPLETE WORK WILL BE BILLED BACK TO THE CONTRACTOR AND OR SUBCONTRACTOR, AT THE OWNERS' DISCRETION.

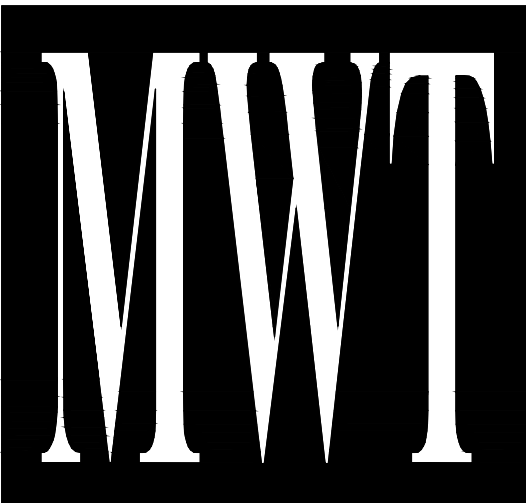

3827 BILLO ROAD
ALDEN, NY, 14004
716-631-0600
ARCHITECT OF RECORD

DONALD M. EDWARD
LICENSE #: 20212
10800 ALABASTER DR.
DAVIDSON, NC 28036
donedwardarchitect@gmail.com



04/20/2023

WARNING
IT IS A VIOLATION OF THE LAW FOR ANY PERSON, UNLESS ACTING UNDER THE DIRECTION OF THE ARCHITECT OR ENGINEER, TO ALTER OR REPRODUCE THESE DRAWINGS IN ANY WAY.

DRAWING QUESTIONS
CA@MWTUSA.COM
1-800-717-5816

ISSUED FOR :

CONSTRUCTION AND BID SET



EAGLE PASS, TX 78852
PROTOTYPE VERSION: 3.0

REVISIONS

NO.	DESCRIPTION	DATE	BY
1	FF&E FRANCHISE UPDATE	08/04/23	-

PROJECT NO.: 22-014

DATE: 06/09/23

DRAWN BY: BS

CHKD. BY: AS

ENLARGED
OUTDOOR POOL &
PATIO - POWER &
R.C PLAN

SHEET

AS104.1

22-014-104-1 ENLARGED OUTDOOR POOL & PATIO PLAN, POOL SECTION.dwg