

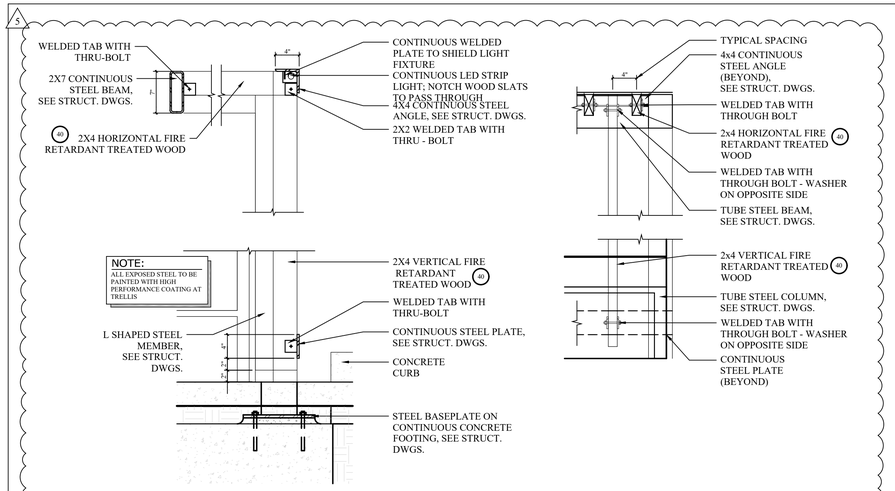


11 TRELLIS DETAIL
1" = 1'-0"


10 TRELLIS DETAIL
1" = 1'-0"

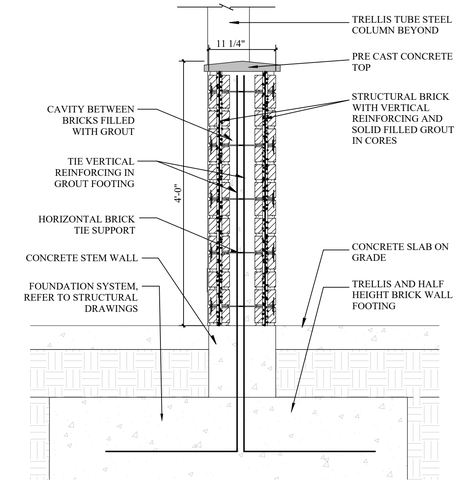


9 BRICK WALL SECTION
1" = 1'-0"

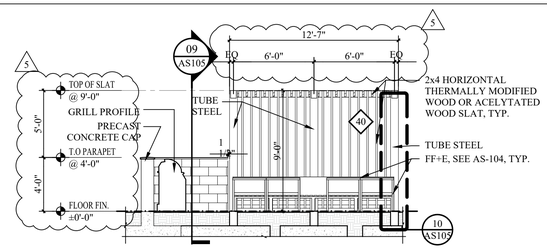

8 SECTION - PATIO GRILL
3/16" = 1'-0"

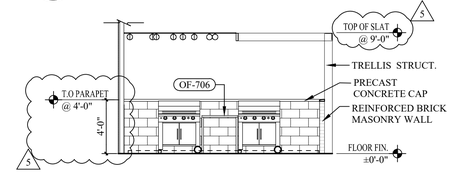


7 ELEVATION - PATIO GRILL
3/16" = 1'-0"

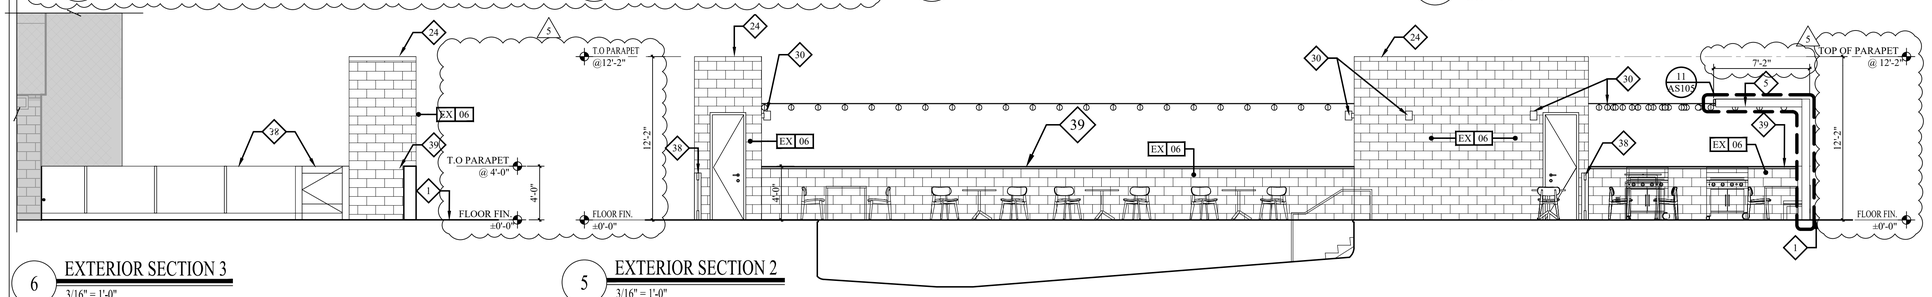


6 EXTERIOR SECTION 3
3/16" = 1'-0"


5 EXTERIOR SECTION 2
3/16" = 1'-0"

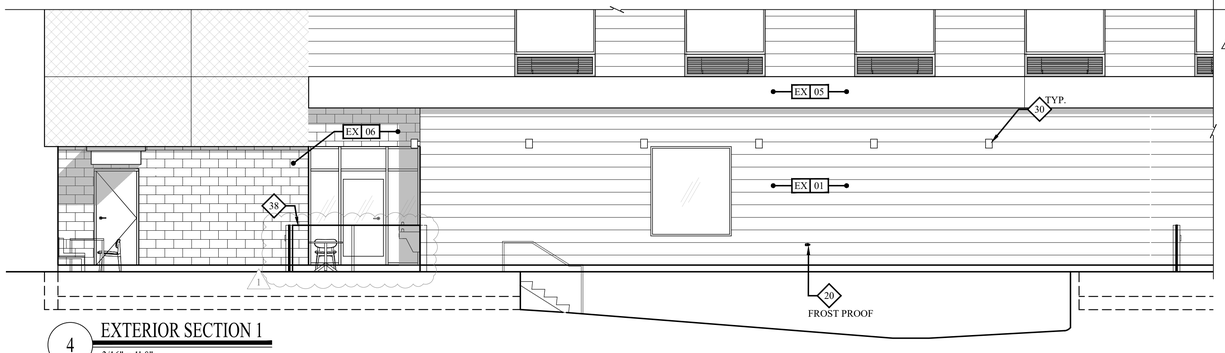

4 EXTERIOR SECTION 1
3/16" = 1'-0"

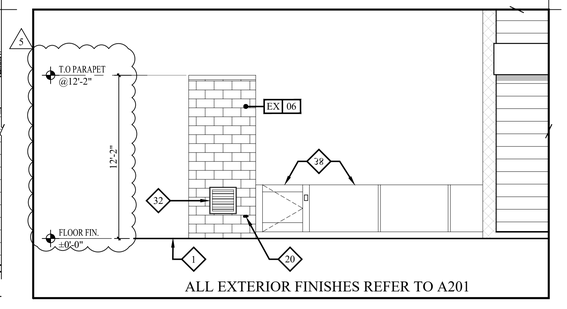


3 EXTERIOR SIDE ELEVATION
3/16" = 1'-0"

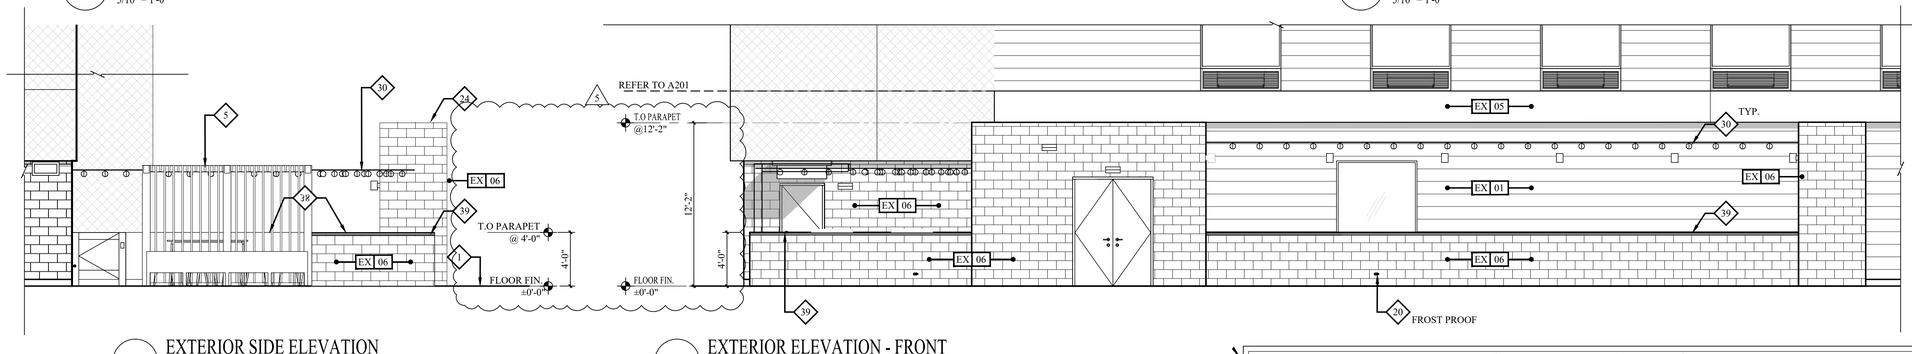

2 EXTERIOR SIDE ELEVATION
3/16" = 1'-0"

1 EXTERIOR ELEVATION - FRONT
3/16" = 1'-0"

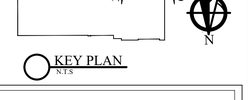

KEY PLAN
N.T.S

IMPORTANT NOTICE TO ALL CONTRACTORS AND OR SUBCONTRACTORS: (COMPLETE BUILDING SYSTEMS AND OR INSTALLATIONS)

IF AWARDED A CONTRACT FOR ANY PORTION OF WORK NEEDED TO COMPLETE THIS PROJECT YOU ARE AGREEING TO THE FOLLOWING TERMS:

1. YOU ARE A QUALIFIED CONTRACTOR AND OR SUBCONTRACTOR SPECIFICALLY IN PROVIDING A COMPLETE TURNKEY SERVICE IN YOUR TRADE OR PROFESSION FOR THE TYPE OF WORK AND SCOPE FOR THIS PROJECT.
2. YOU AGREE TO PROVIDE A COMPLETE DESIGN BUILD SOLUTION BASED ON THE ARCHITECTS INTENDED DESIGN FOR THIS PROJECT.
3. YOUR BID INCLUDED ALL THE STEPS, PROCESSES, MATERIALS, PRODUCTS, GOVERNING PERMITS AND APPROVALS NECESSARY TO PROVIDE A COMPLETED AND WARRANTED SYSTEM OR INSTALLATION THAT DOES NOT REQUIRED ANOTHER CONTRACTOR OR PRODUCT TO COMPLETE YOUR SCOPE OF WORK.
4. YOUR BID MUST HAVE INCLUDED ANY DESIGN INFORMATION REFERENCED WITHIN ANY CIVIL, ARCHITECTURAL, STRUCTURAL, MECHANICAL, ELECTRICAL AND OR PLUMBING DRAWINGS; ALSO NOTE THESE DRAWINGS ARE SCHEMATIC AND ARE INTENDED TO SHOW ONLY BASIC CONCEPTS AND GENERAL INFORMATION. THE COMPLETION OF YOUR WORK MAY INCLUDE OTHER STEPS, PROCESSES, MATERIALS, PRODUCTS, LABOR, GOVERNING PERMITS AND OR APPROVALS NECESSARY TO PROVIDE A COMPLETE SYSTEM INSTALLATION WHETHER SUGGESTED ON THE DRAWINGS OR NOT.
5. AS AN EXAMPLE: ITEMS AND OR TASKS LIKE: FIRE CAULK, DRAFT STOPS, FASTENERS, ANCHORS, EMBEDMENTS, DUMPSTERS, DEBRIS CLEAN UP, ETC. ARE YOUR RESPONSIBILITY. ANY WORK NOT COMPLETED IN A TIMELY MANNER, OR INCOMPLETE WORK WILL BE BILLED BACK TO THE CONTRACTOR AND OR SUBCONTRACTOR, AT THE OWNERS' DISCRETION.

KEYED NOTES

1	APPROXIMATE LINE OF GRADE
2	ABOVE GRADE EXPOSED FOUNDATION WALL
4	PAINTED TUBE STEEL CANOPY WITH WOOD FINISHED SOFFIT
5	MODIFIED WOOD CANOPY WITH STEEL SUPPORT
6	MECHANICAL EQUIPMENT SCREEN - REVIEW ALL VIEWS AROUND PROPERTY BEFORE LOCATING ALL ROOF TOP MECHANICAL UNITS. VERIFY ALL EQUIPMENT IS ADEQUATELY SCREENED
8	ALUMINUM FIXED WINDOW WITH THERMAL BROKEN FRAME, INSULATED GLAZING WITH INTEGRAL ALUMINUM LOUVER AT PTAC UNITS - SEE SHEET A-601 FOR SIZES.
9	ALUMINUM STOREFRONT SYSTEM WITH THERMAL BROKEN FRAME AND INSULATED GLAZING
10	ALUMINUM FIXED WINDOW WITH THERMAL BROKEN FRAME AND INSULATED GLAZING
11	ELEVATOR OVERRUN
13	LAUNDRY CHUTE OVERRUN
18	FINISH CONTROL JOINT
19	OVERFLOW SCUPPER - BASIS OF DESIGN NESCO MFG INC. - MODEL # SCT914R - REFER ALSO TO DETAIL 7/A-303
20	TAMPER RESISTANT, RECESSED HOSE BIBB - MOUNT TOP AT +12"A.F.F
23	SIGNAGE - REFER TO EXTERIOR SIGNAGE SPECIFICATIONS
24	KYNAR FINISH ALUMINUM COPING SYSTEM --COLOR TO MATCH ADJACENT MATERIAL
25	KYNAR FINISH ALUMINUM GRAVEL STOP -COLOR TO MATCH ADJACENT MATERIAL
30	LIGHT FIXTURE - REFER TO CEILING PLAN
31	EXPANSION JOINT AT FLOOR LINE WITH BACKER ROD AND SEALANT
32	ALUMINUM LOUVER - COLOR TO MATCH ADJACENT MATERIAL MATCHING ADJACENT WALL
33	BUILDING HEIGHT DIMENSIONS ARE BASED ON WOOD FRAME CONSTRUCTION. THESE DIMENSIONS WILL VARY BASED ON FINAL BUILDING CONSTRUCTION. INTERIOR CEILING HEIGHT DIMENSIONS ARE CRITICAL TO MAINTAIN AS MINIMUMS.
36	ALUMINUM GUTTER AND DS. COLOR TO MATCH ADJ. MATERIAL
37	ACCESSIBLE KEY CARD READER WIRED TO ELECTRIC STRIKE IN DOOR - TOP OF READER AT 48" MAX. HEIGHT
38	POOL PERIMETER FENCE AS REQUIRED BY CODE WITH 3'-0" GATE
39	PRECAST COPING
40	TRELLIS THERMALLY MODIFIED WOOD OR ACELYTATED WOOD, POSSIBLE PRODUCTS: - THERMALLY MODIFIED WOOD - THERMORY, USA - ACELYTATED WOOD - ACOYA

ARCHITECTURAL ELEMENTS

EX-1	FIBER CEMENT SIDING COLOR: SAN FRANCISCO BAY TEXTURE: MEDIUM FINISH CORE: BODY BACKGROUND FOR LAYERING OF ALL OTHER MATERIALS	
EX-5	EIFS. COLOR: WHITE TEXTURE: SMOOTH FINISH ACCENT BAND: ARTICULATION HORIZONTAL 3D BAND PROUD OF CORE. SUFFICIENT DEPTH (2" MIN) TO CREATE DISTINCT SHADOW LINE. NO VISIBLE JOINTS.	
EX-6	FACE BRICK. COLOR: STONE TEXTURE: SANDSTONE LIKE SUPPORT: BASE	

MWT
3827 BILLO ROAD
ALDEN, NY, 14004
716-631-0600
ARCHITECT OF RECORD

DONALD M. EDWARD
LICENSE #: 20212
10800 ALABASTER DR.
DAVIDSON, NC 28036
donedwardarchitect@gmail.com

REGISTERED ARCHITECT DONALD M. EDWARD 20212 STATE OF TEXAS

04/20/2023

WARNING
IT IS A VIOLATION OF THE LAW FOR ANY PERSON, UNLESS ACTING UNDER THE DIRECTION OF THE ARCHITECT OR ENGINEER, TO ALTER OR REPRODUCE THESE DRAWINGS IN ANY WAY.

DRAWING QUESTIONS
CA@MWTUSA.COM
1-800-717-5816

ISSUED FOR :

CONSTRUCTION AND BID SET

HOME2 SUITES BY HILTON

EAGLE PASS, TX 78852
PROTOTYPE VERSION: 3.0

REVISIONS

NO.	DESCRIPTION	DATE	BY
1	FF&E FRANCHISE UPDATE	08/04/23	-
5	REVISED PER RFI	04/09/26	-

PROJECT NO.:	22-014
DATE:	4/9/26
DRAWN BY:	RH/BS
CHKD. BY:	AS/FS

ENLARGED OUTDOOR POOL & PATIO - ELEV. & SECTIONS

SHEET
AS105

22-014 AS105 ENLARGED OUTDOOR POOL & PATIO ELEVATIONS & SECTIONS.dwg