




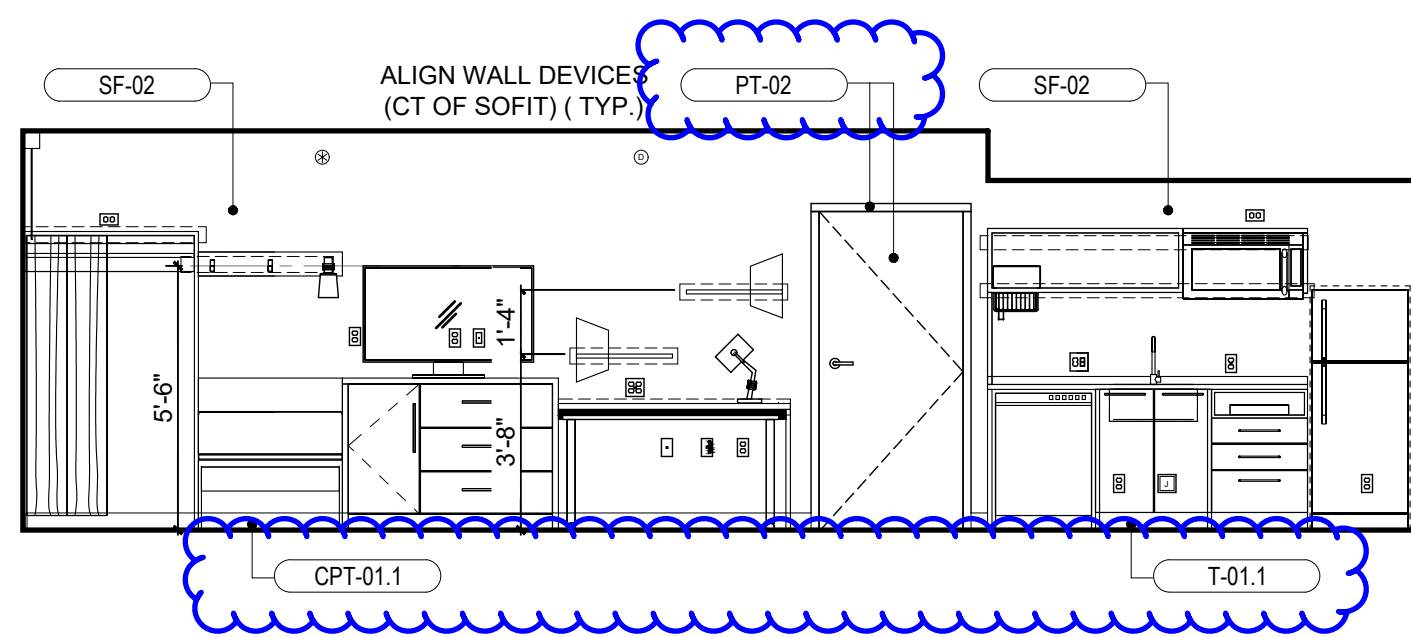


9 INTERIOR ELEVATION
1/4" = 1'-0"

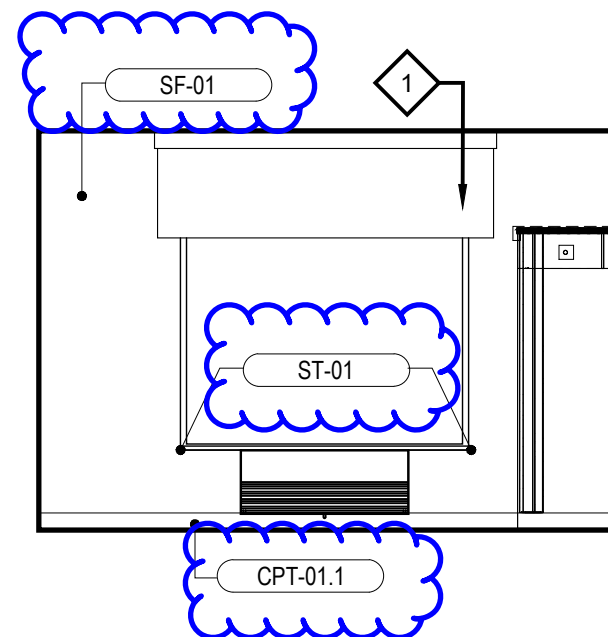


8 INTERIOR ELEVATION
1/4" = 1'-0"

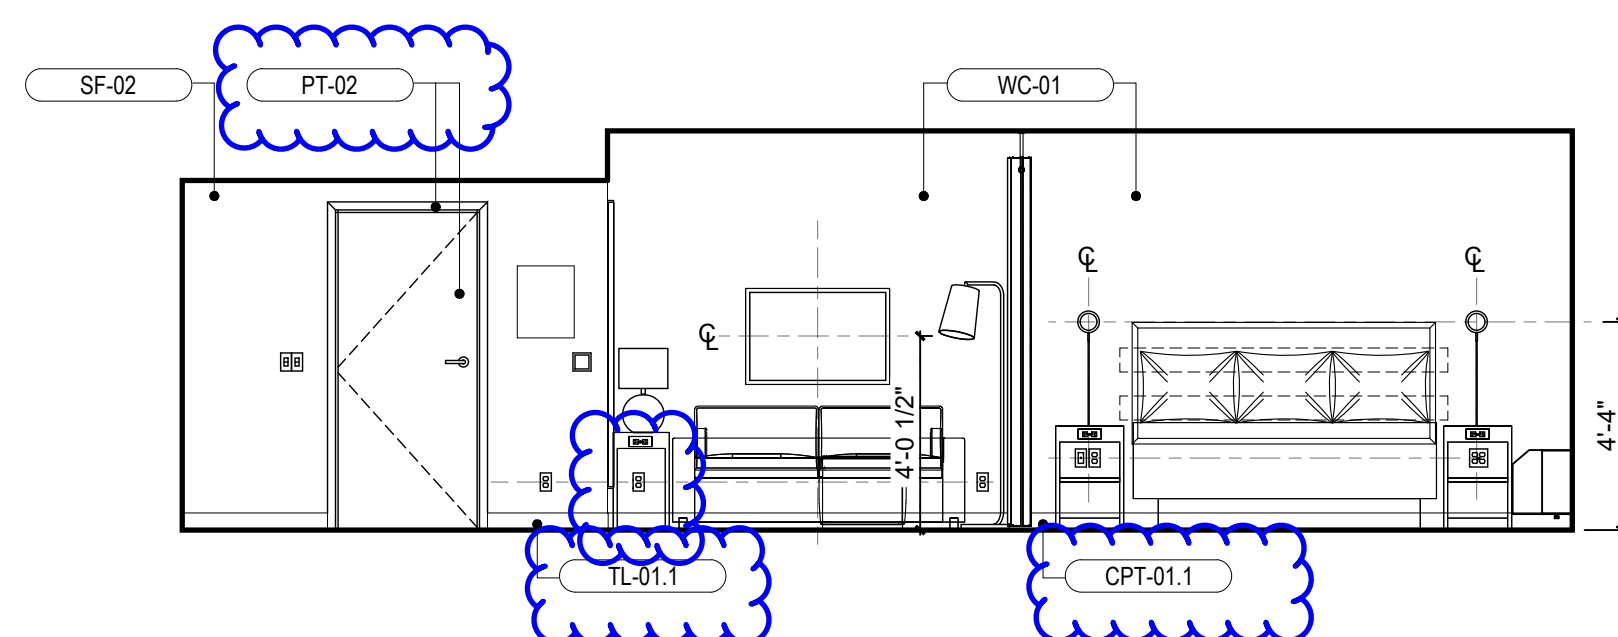


7 INTERIOR ELEVATION
1/4" = 1'-0"

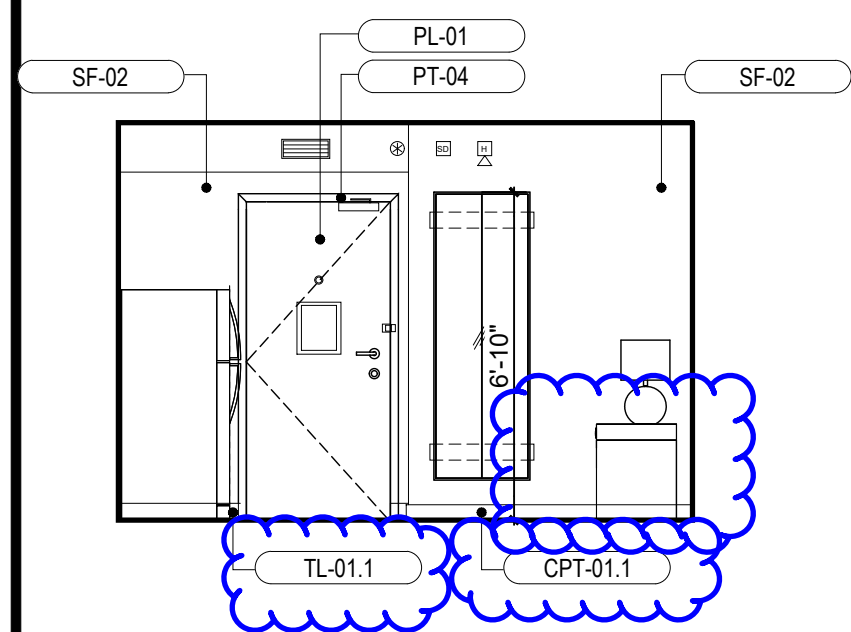


6 INTERIOR ELEVATION
1/4" = 1'-0"

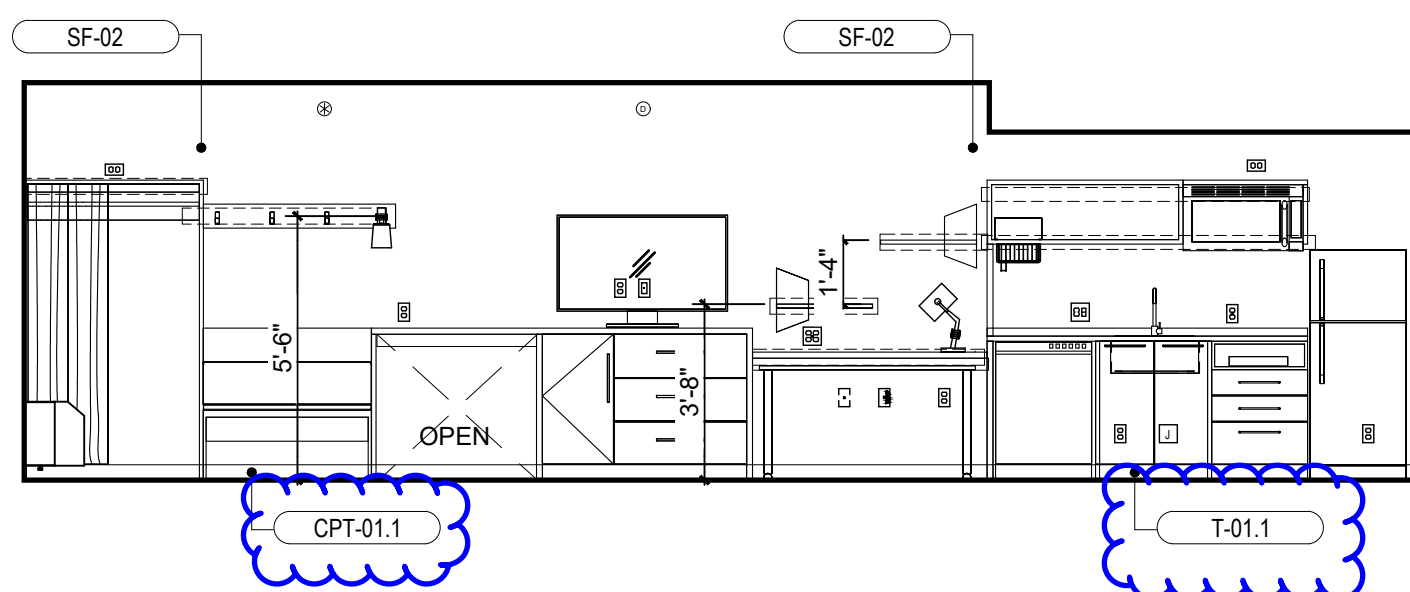


5 INTERIOR ELEVATION
1/4" = 1'-0"

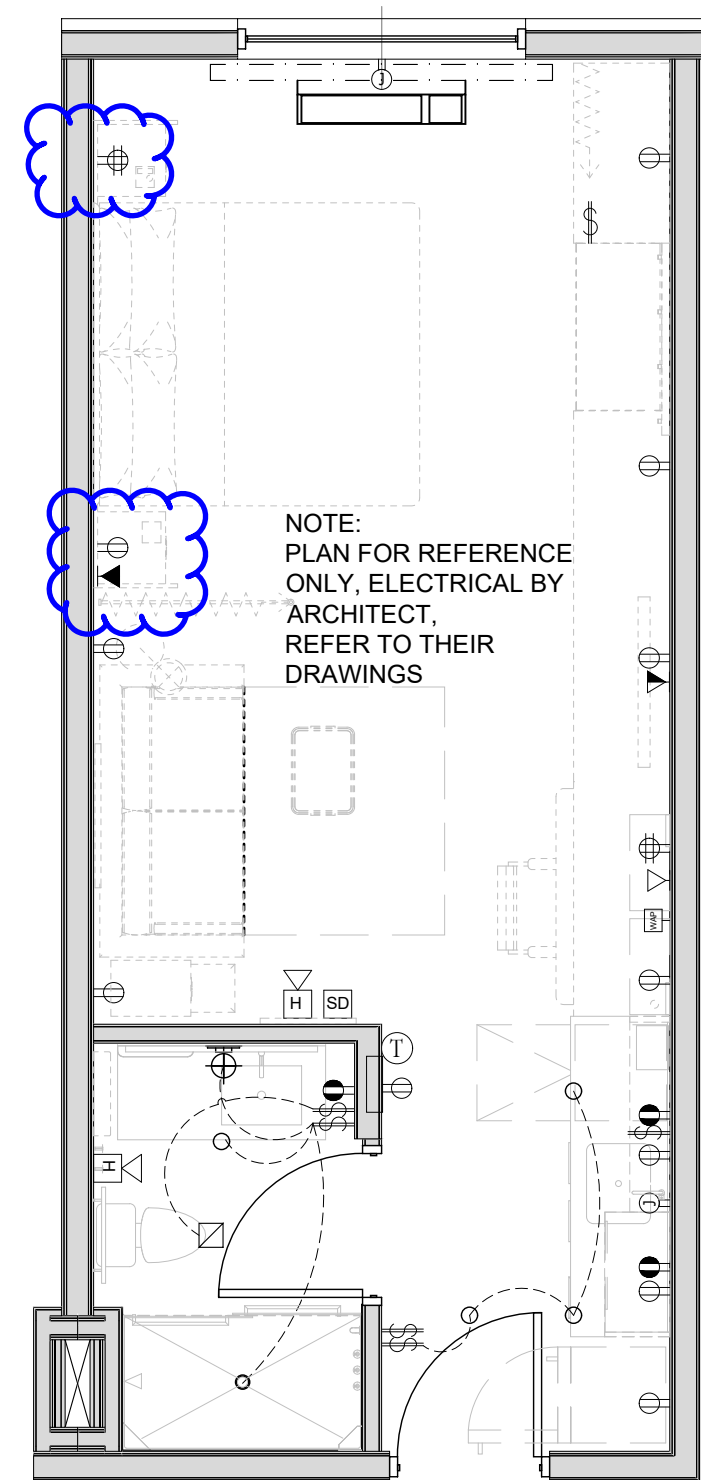


4 KING STUDIO-ELECTRICAL PLAN
1/4" = 1'-0"

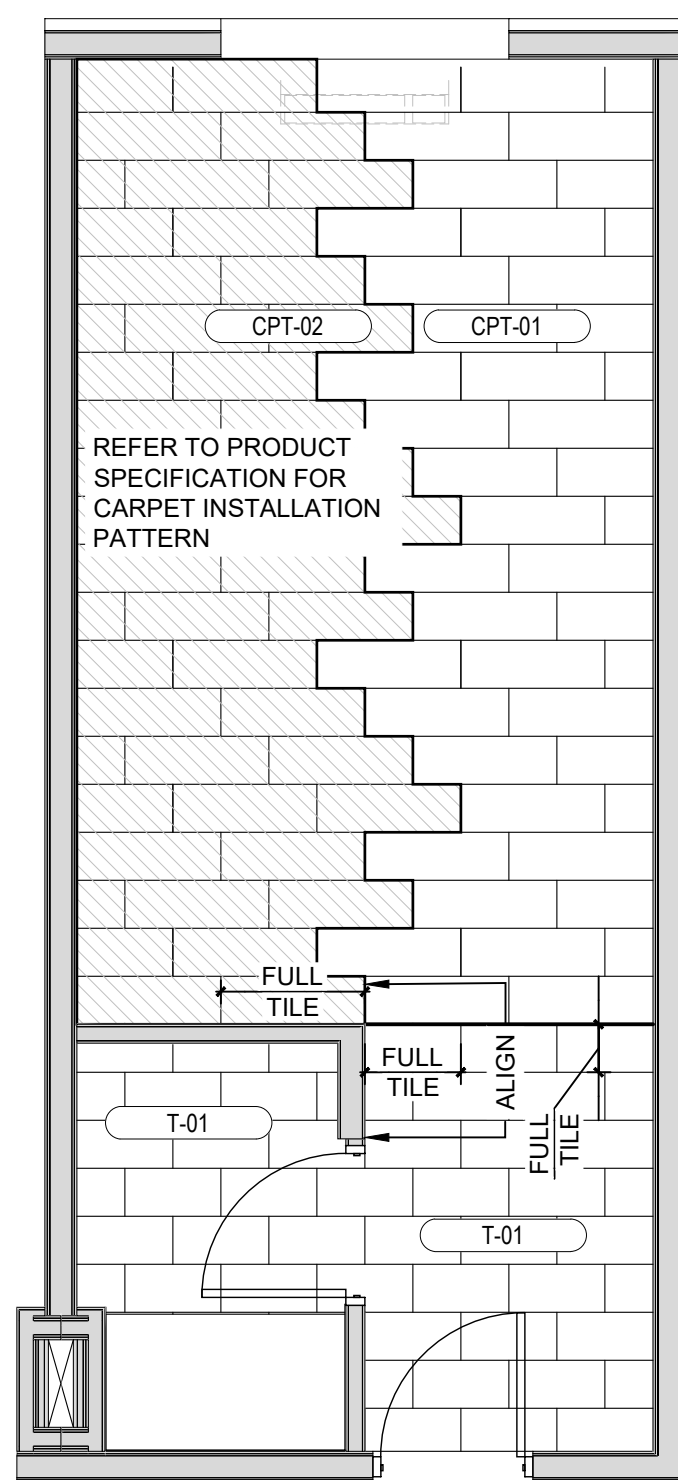


3 KING STUDIO-FINISH PLAN
1/4" = 1'-0"

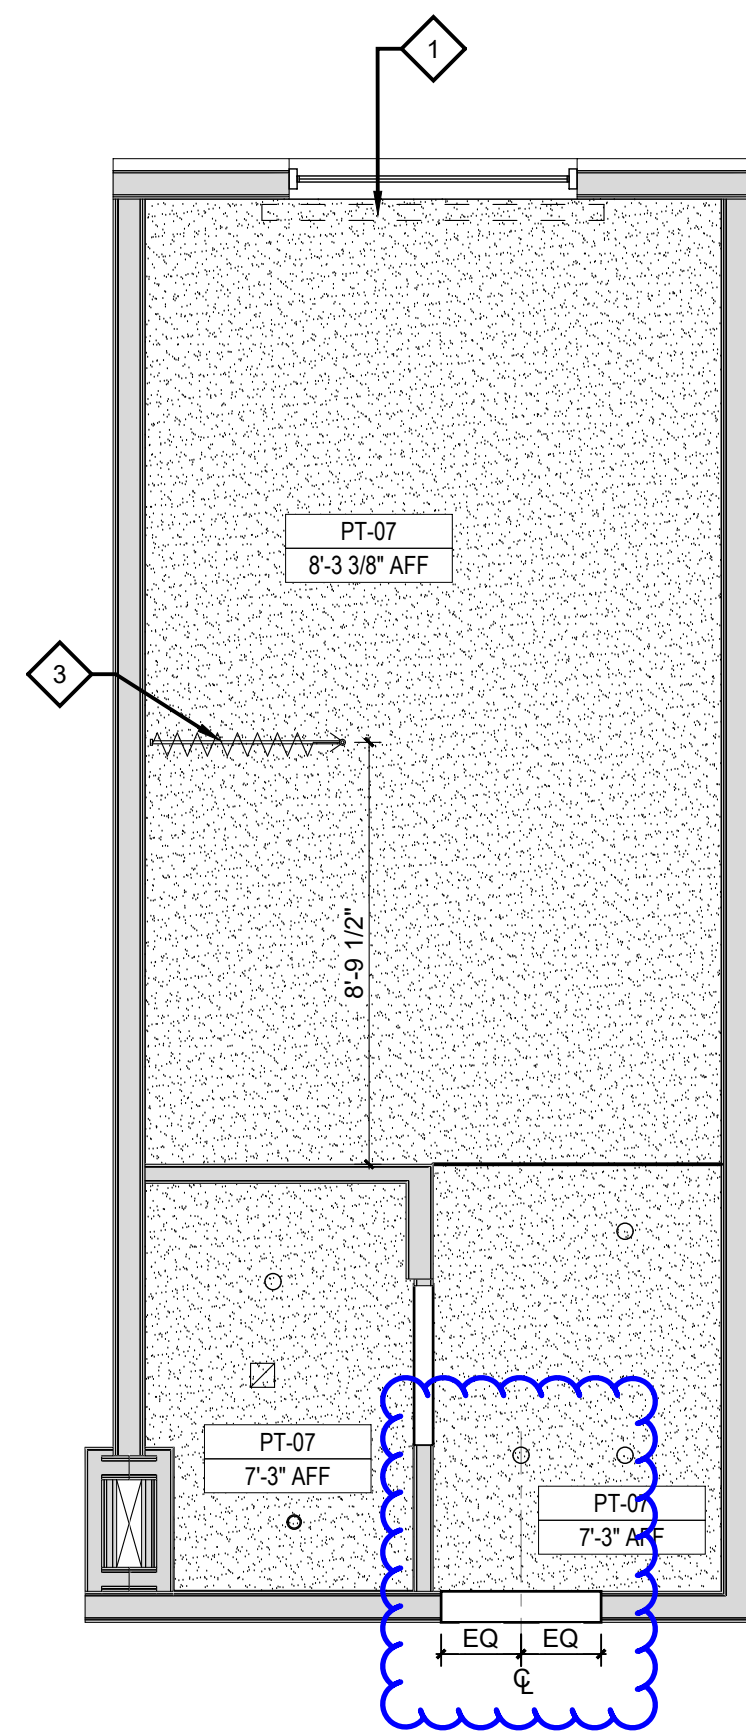

2 KING STUDIO- REFLECTED CEILING PLAN
1/4" = 1'-0"

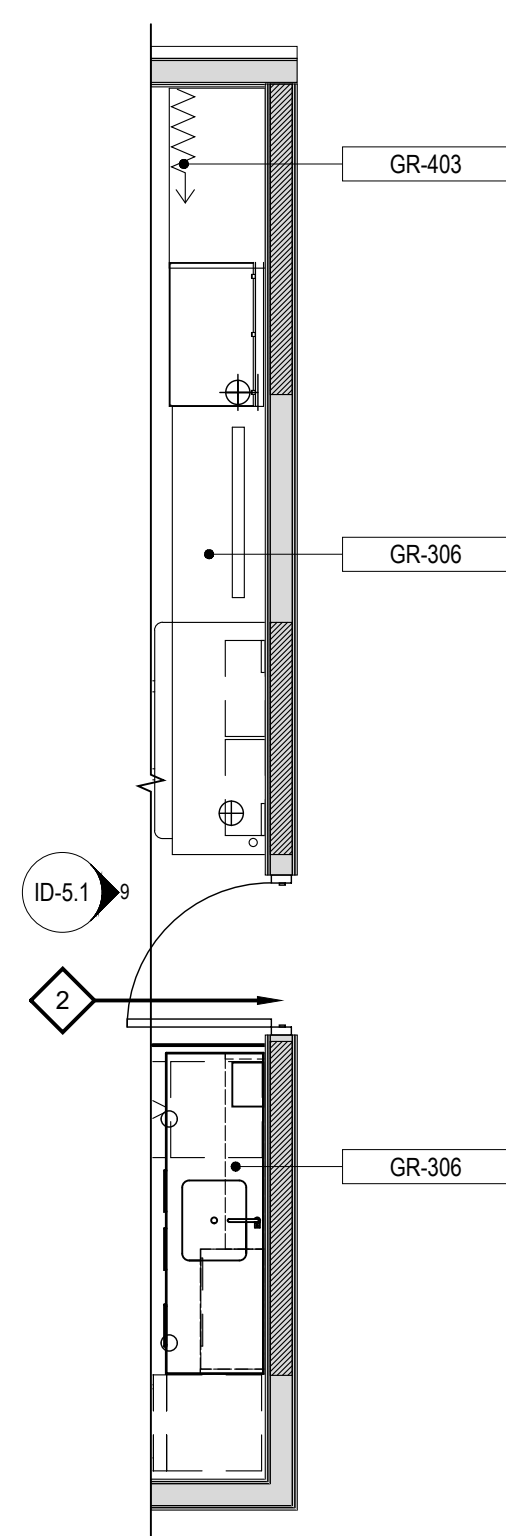

1.1 KING STUDIO CONNECTOR
1/4" = 1'-0"

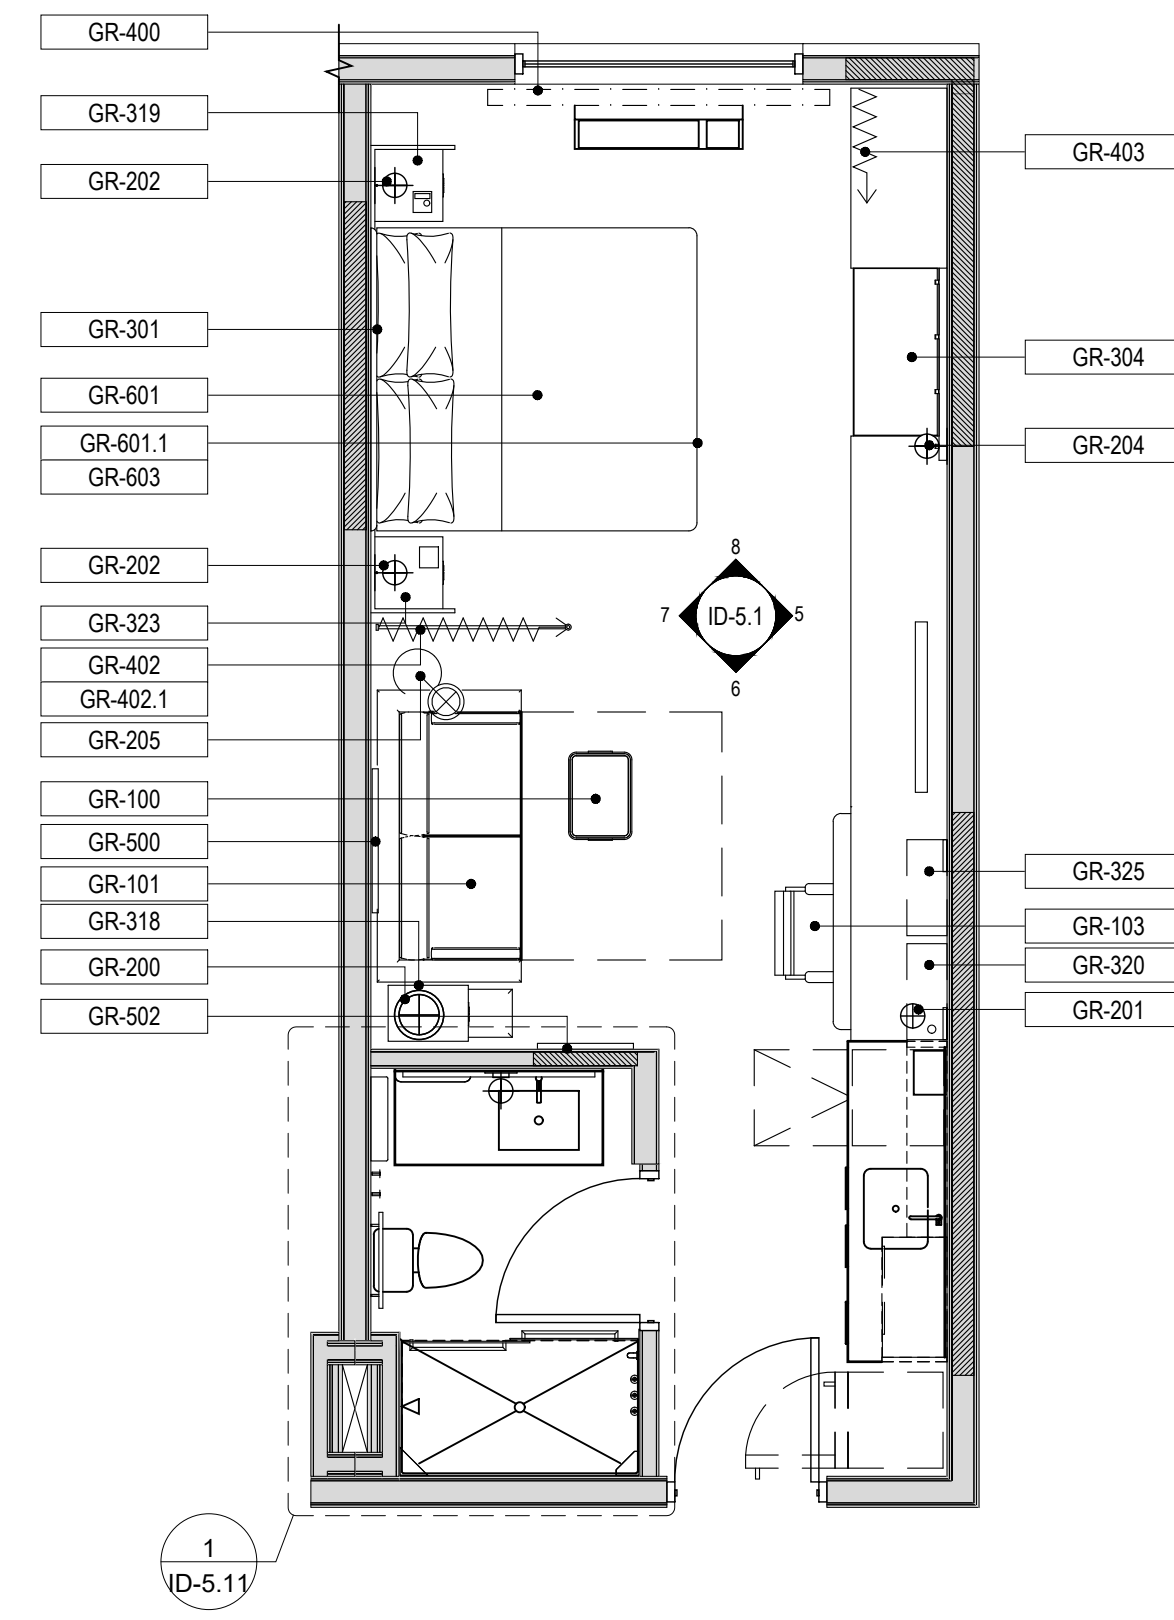

1 KING STUDIO - FFE PLAN
1/4" = 1'-0"

GENERAL NOTES	
1.	REFER TO ARCHITECTS DRAWINGS FOR ALL ARCHITECTURAL LIGHTING, EQUIPMENT, F&B, ELECTRICAL AND TRANSITION DETAILS.
2.	USE 1/3" OFFSET WHEN INSTALLING LARGE TILES TO AVOID LIPPAGE
3.	REFRAIN FROM CUTTING TILES DURING INSTALLATION. ONLY INSTALL WHOLE TILES WHEN POSSIBLE.
KEY NOTES:	
◆	BLACK OUT ROLLER SHADE TO EXTEND 6" BEYOND WINDOW OPENING. SHEER ROLLER SHADE TO BE MOUNTED INSIDE WINDOW OPENING. GR-400 IS MANUAL. GR-401 IS MOTORIZED.
◆	ALTERNATE LOCATION OF DOOR FOR CONNECTING ROOMS TO ACCESSIBLE ROOMS-REFER TO OVERALL PLANS FOR LOCATION OF ACCESSIBLE ROOMS
◆	CORRDINATE CURTAIN BLOCKING LOCATION WITH ARCHITECT DRAWINGS



6255 Corporate Center Drive
Dublin, OH 43016
(p) 614.933.0300
(e) info@rkhdesign.com
www.rkhdesign.com



HOME2 SUITES BY HILTON
EAGLEPASS, TX

H2EP LLC

ISSUE SET:
NEW CONSTRUCTION

DATE:
07/04/2025

SCALE:
AS INDICATED

REVISION:
DATE COMMENTS

SHEET TITLE:

ENLARGED GUESTROOM PLANS
& ELEVATIONS - KING STUDIO &
KING STUDIO CONNECTING

SHEET NUMBER:

ID-5.1