


- GENERAL NOTES
1.


REFER TO ARCHITECT'S DRAWINGS FOR ALL ARCHITECTURAL LIGHTING, EQUIPMENT, F&B, ELECTRICAL AND TRANSITION DETAILS.
2.

USE 1/3" OFFSET WHEN INSTALLING LARGE TILES TO AVOID LIPPAGE
3.


REFRAIN FROM CUTTING TILES DURING INSTALLATION. ONLY INSTALL WHOLE TILES WHEN POSSIBLE.

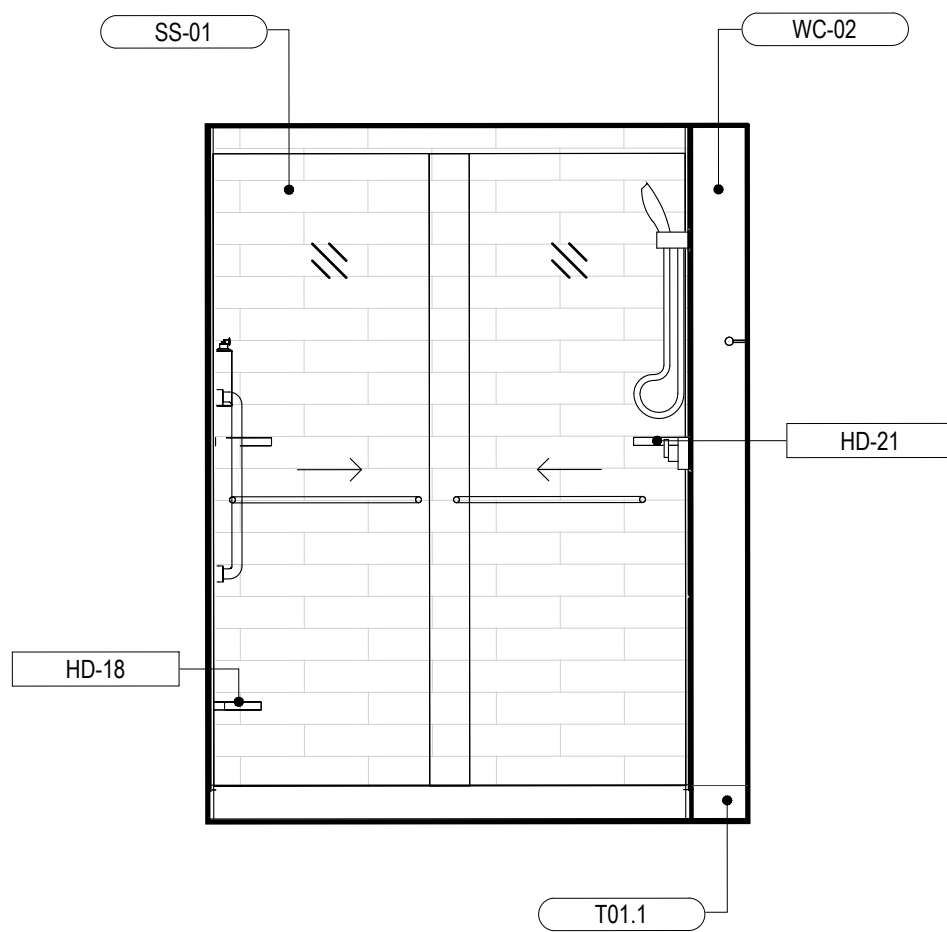


4 INTERIOR ELEVATION
1/2" = 1'-0"

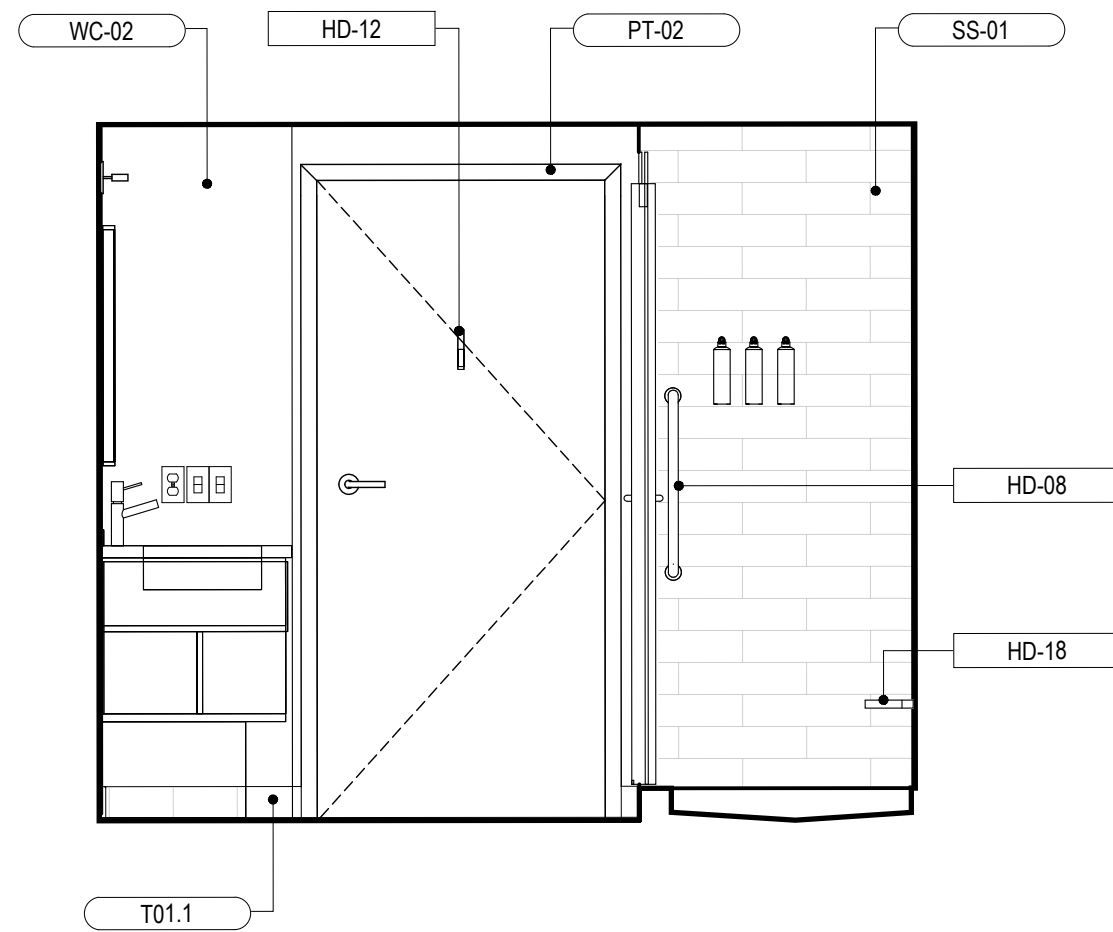


3 INTERIOR ELEVATION
1/2" = 1'-0"

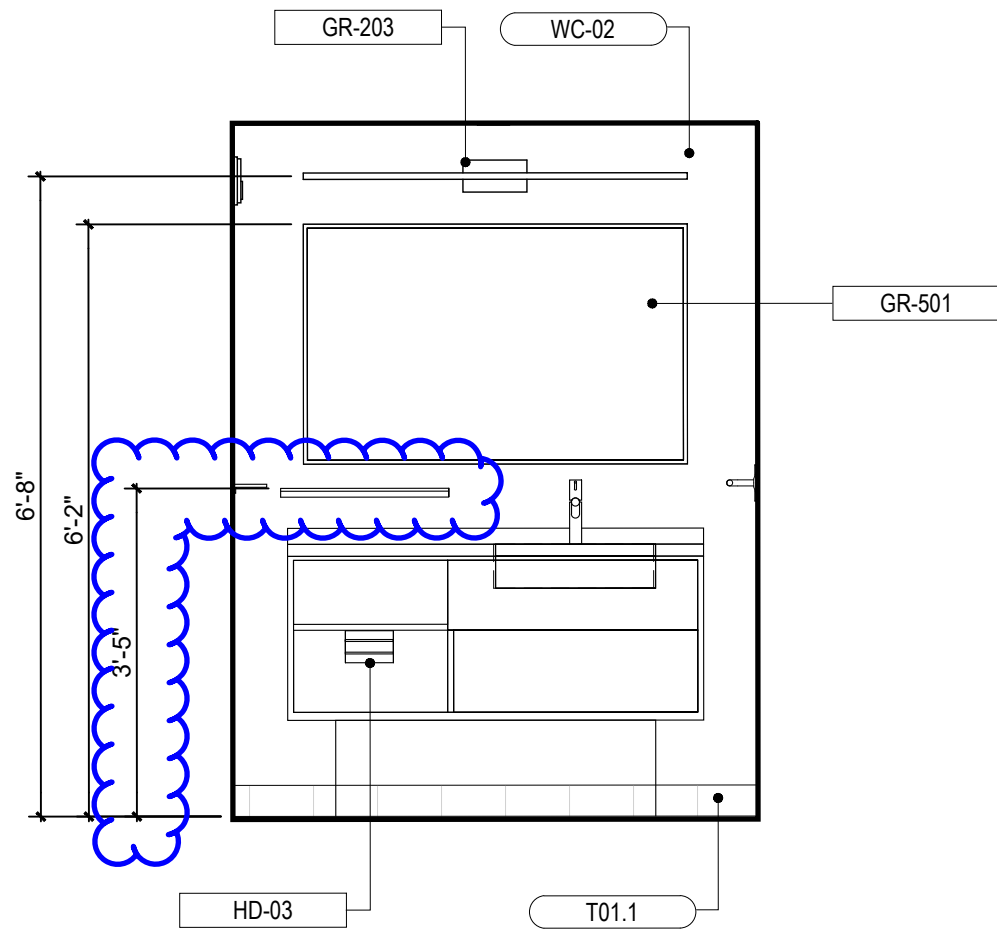

2 INTERIOR ELEVATION
1/2" = 1'-0"

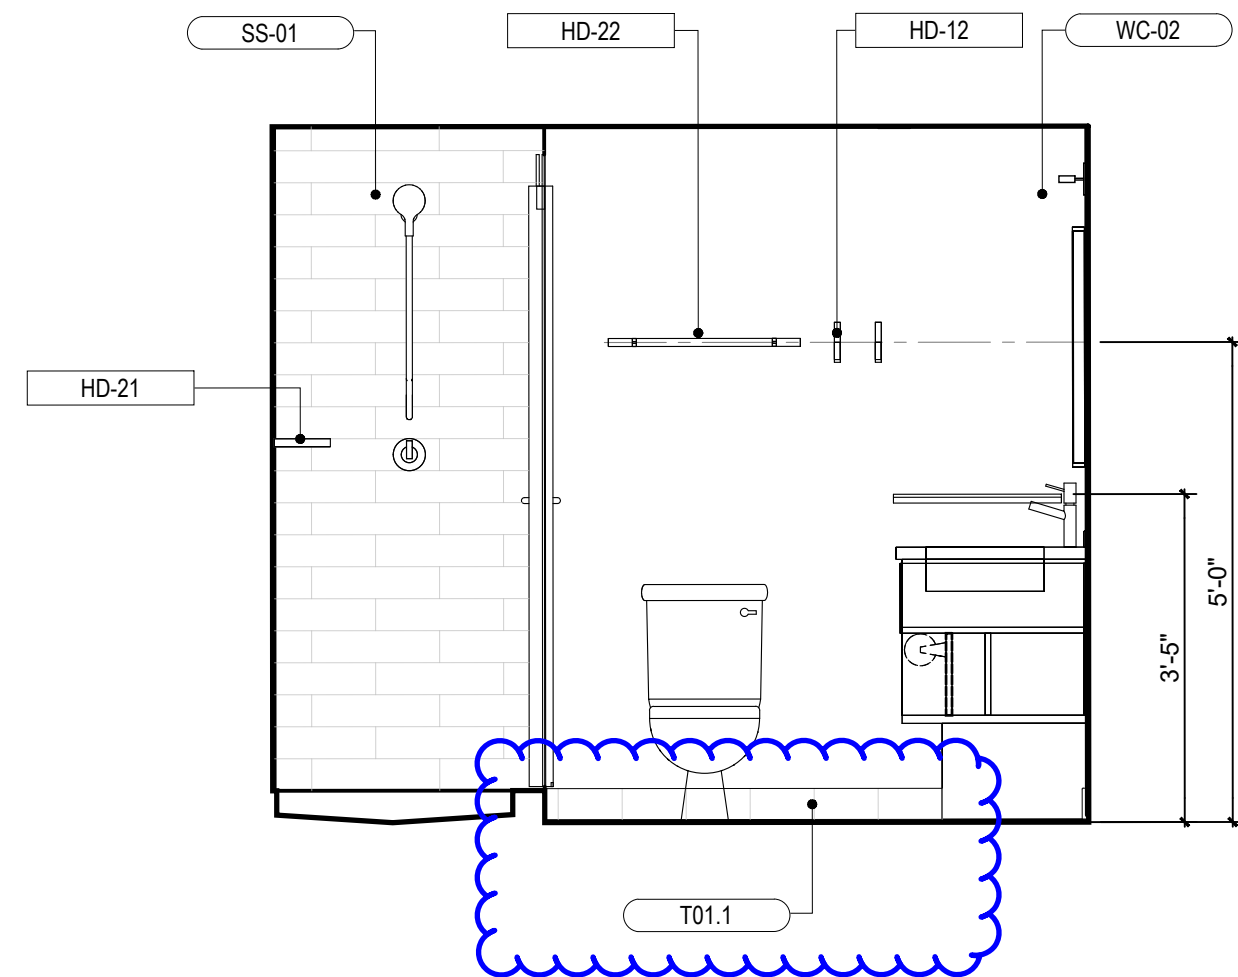

5 INTERIOR ELEVATION
1/2" = 1'-0"

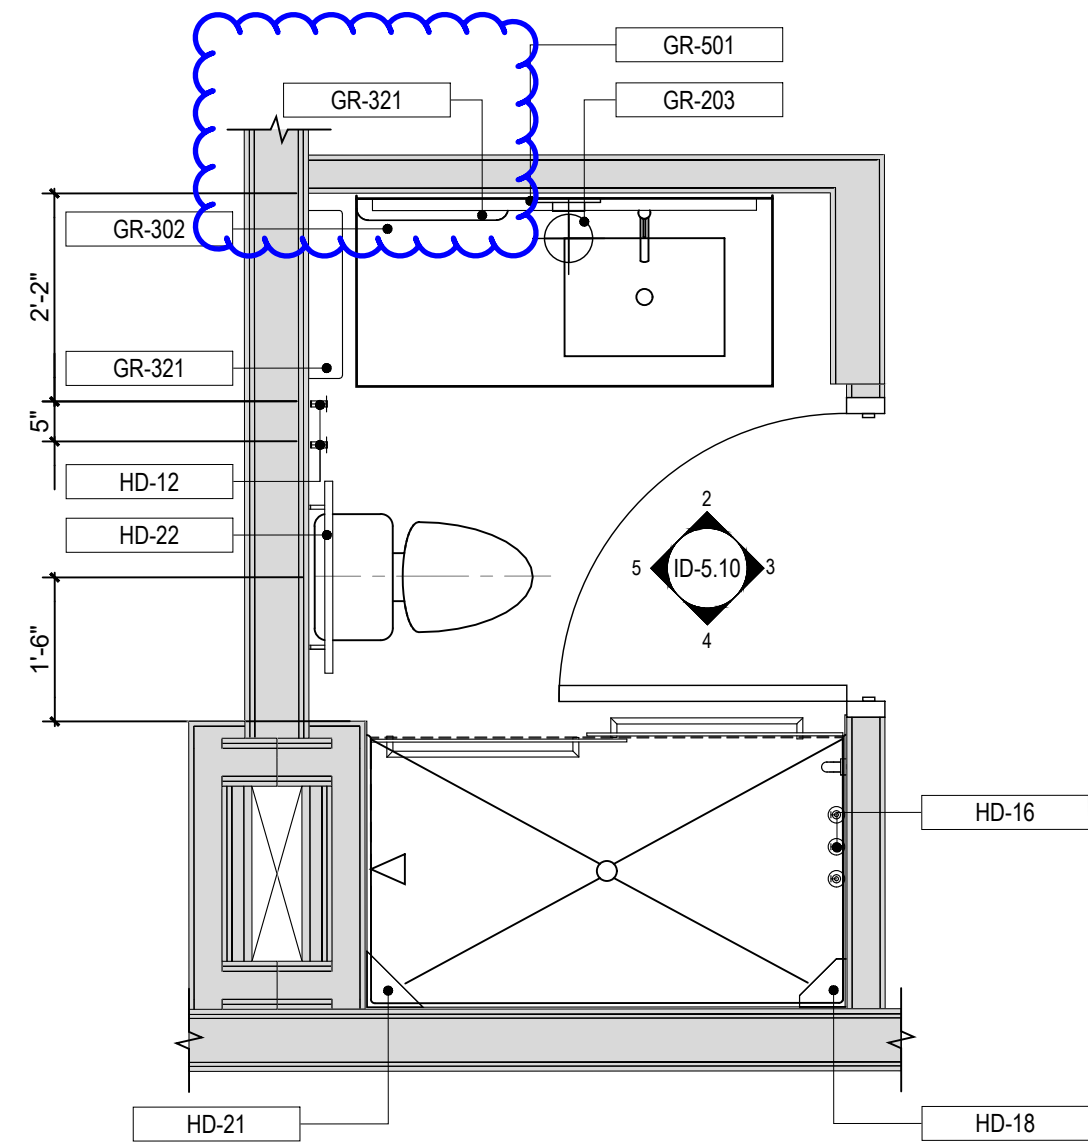

1 PLAN
1/2" = 1'-0"



6255 Corporate Center Drive
Dublin, OH 43016
(p) 614.933.0300
(e) info@rkhdesign.com
www.rkhdesign.com



HOME2 SUITES BY HILTON
EAGLEPASS, TX

H2EP LLC

ISSUE SET:
NEW CONSTRUCTION

DATE:
07/04/2025

SCALE:
AS INDICATED

REVISION:
DATE COMMENTS

SHEET TITLE:
ENLARGED BATHROOM -
KING STD., STD. CONN., QQ
STD., STD CONN., QQ WIDE &
QQ EXT.

SHEET NUMBER:

ID-5.10