



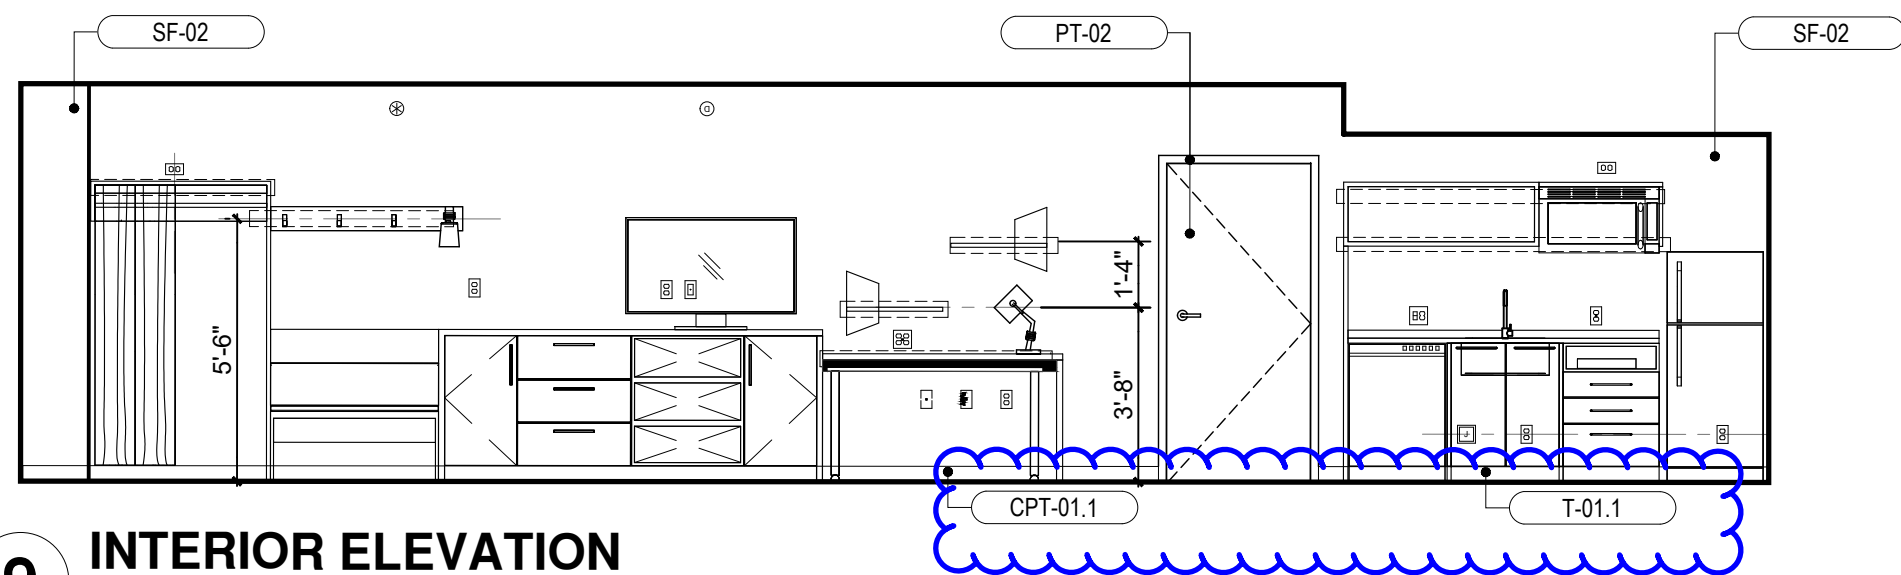

9 INTERIOR ELEVATION


1/4" = 1'-0"

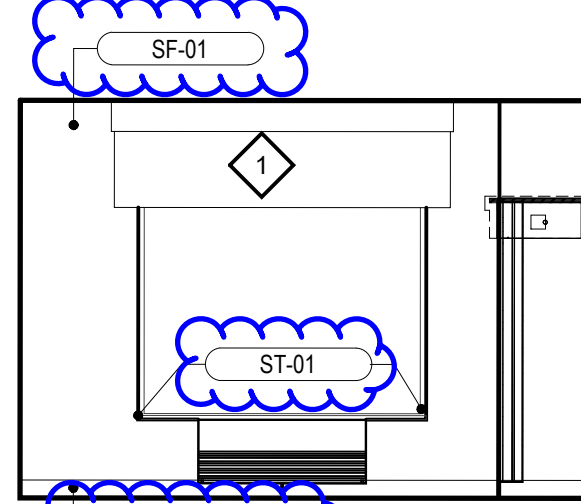

8 INTERIOR ELEVATION


1/4" = 1'-0"

* GO TO PROVIDE BLOCKING AS REQUIRED AND ENSURE CENTER SUPPORTS ARE PROVIDED AS NECESSARY PER VENDOR RECOMMENDATIONS

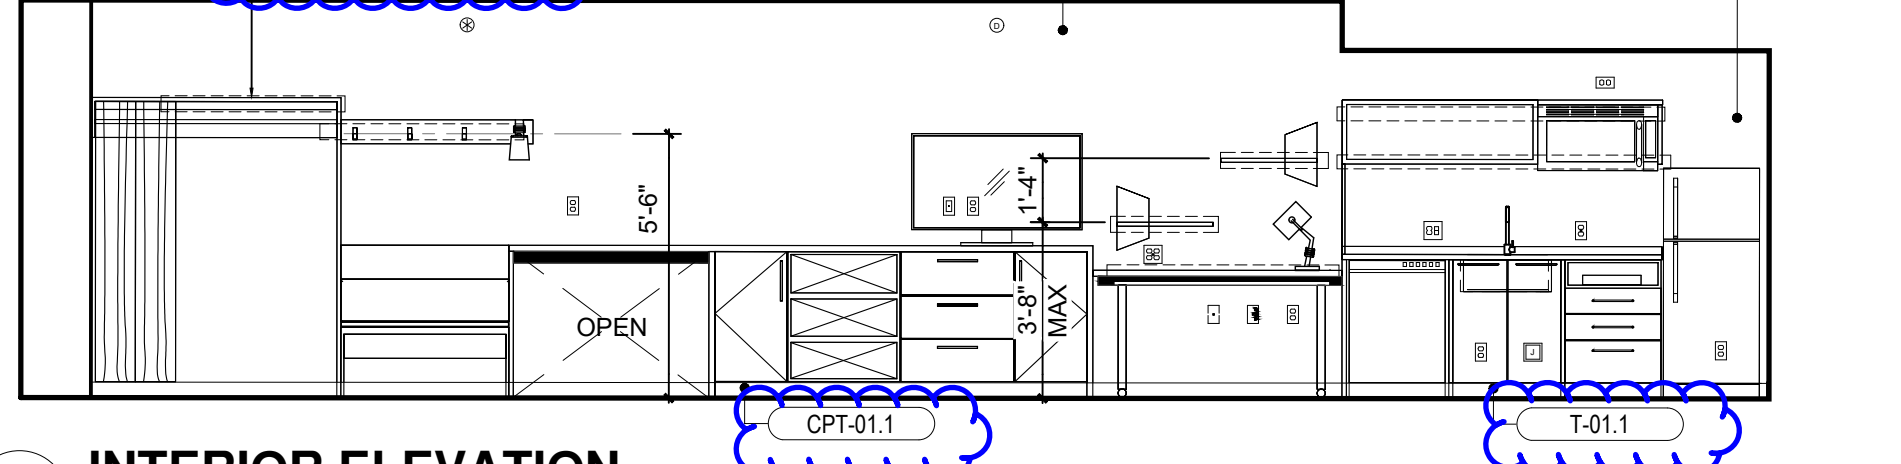


5 INTERIOR ELEVATION

1/4" = 1'-0"

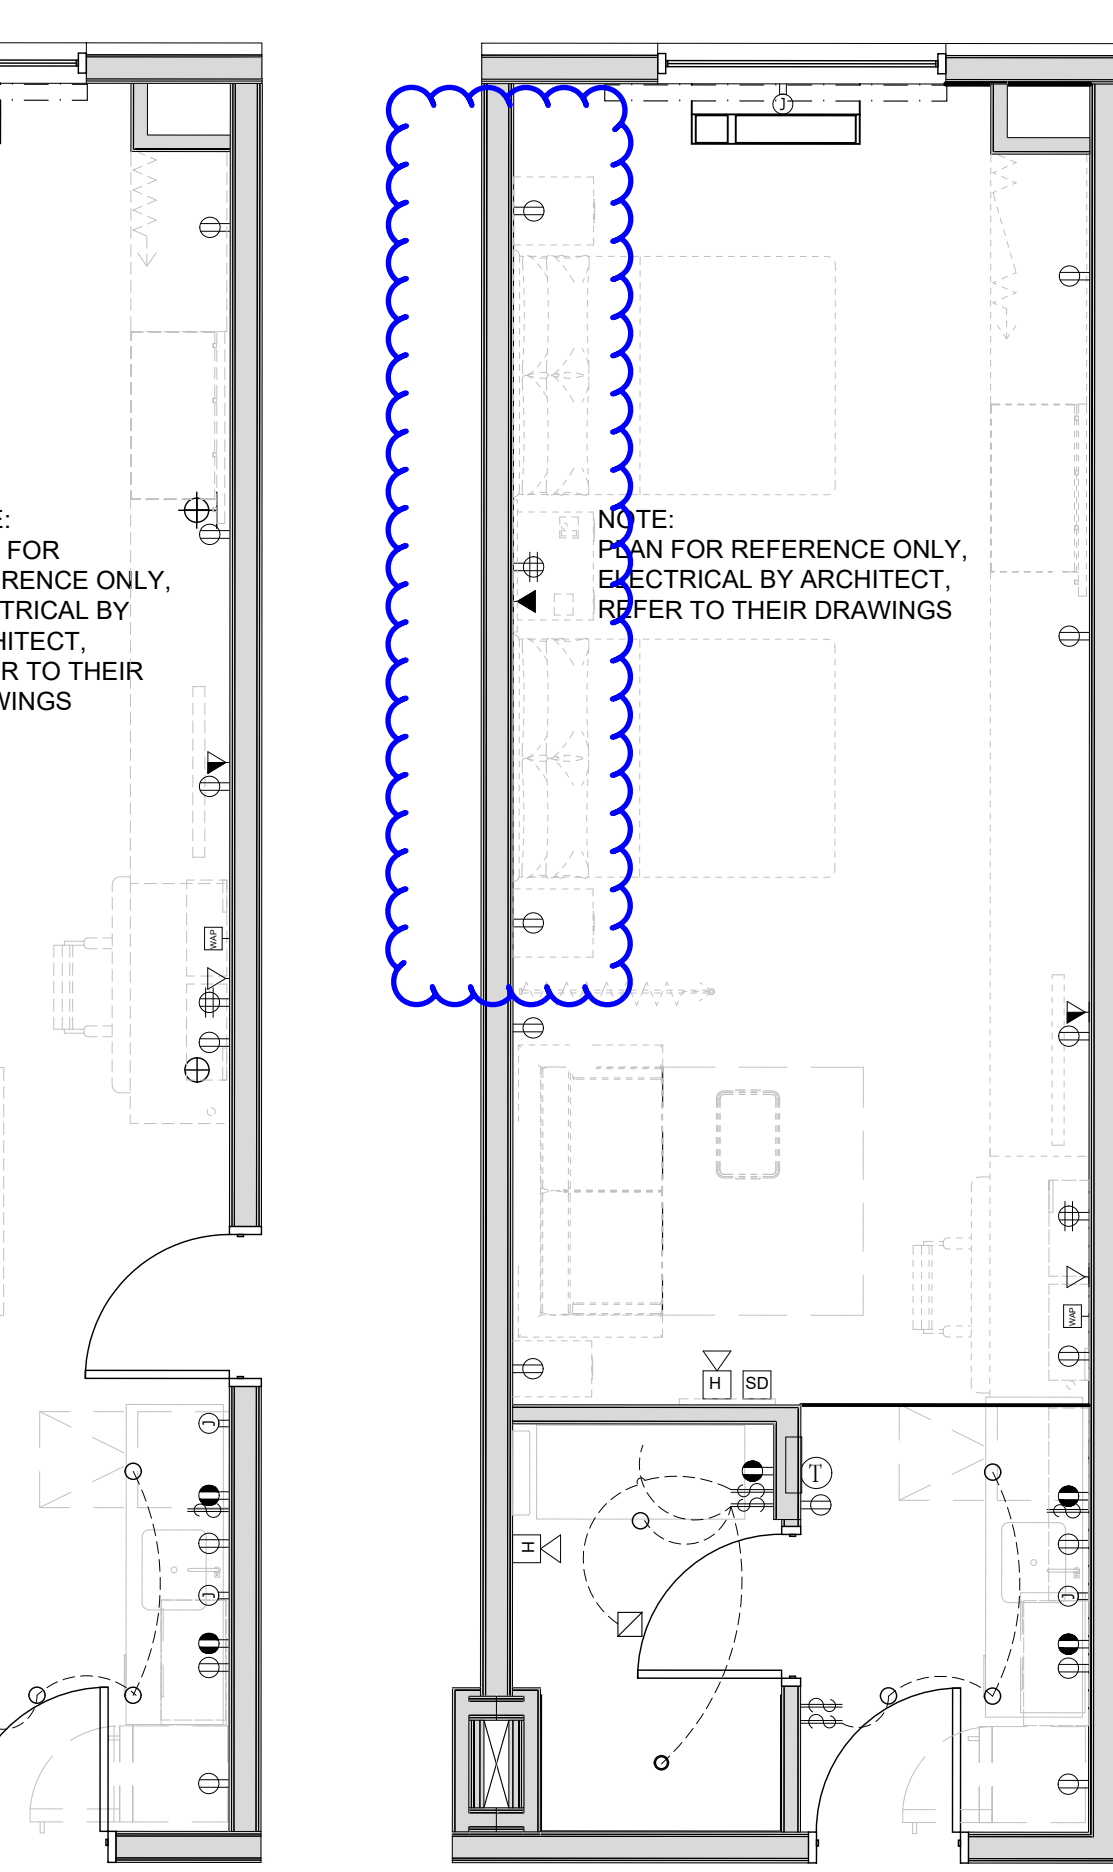


4.1 ELEC. PLAN @ QQ CONN.

1/4" = 1'-0"

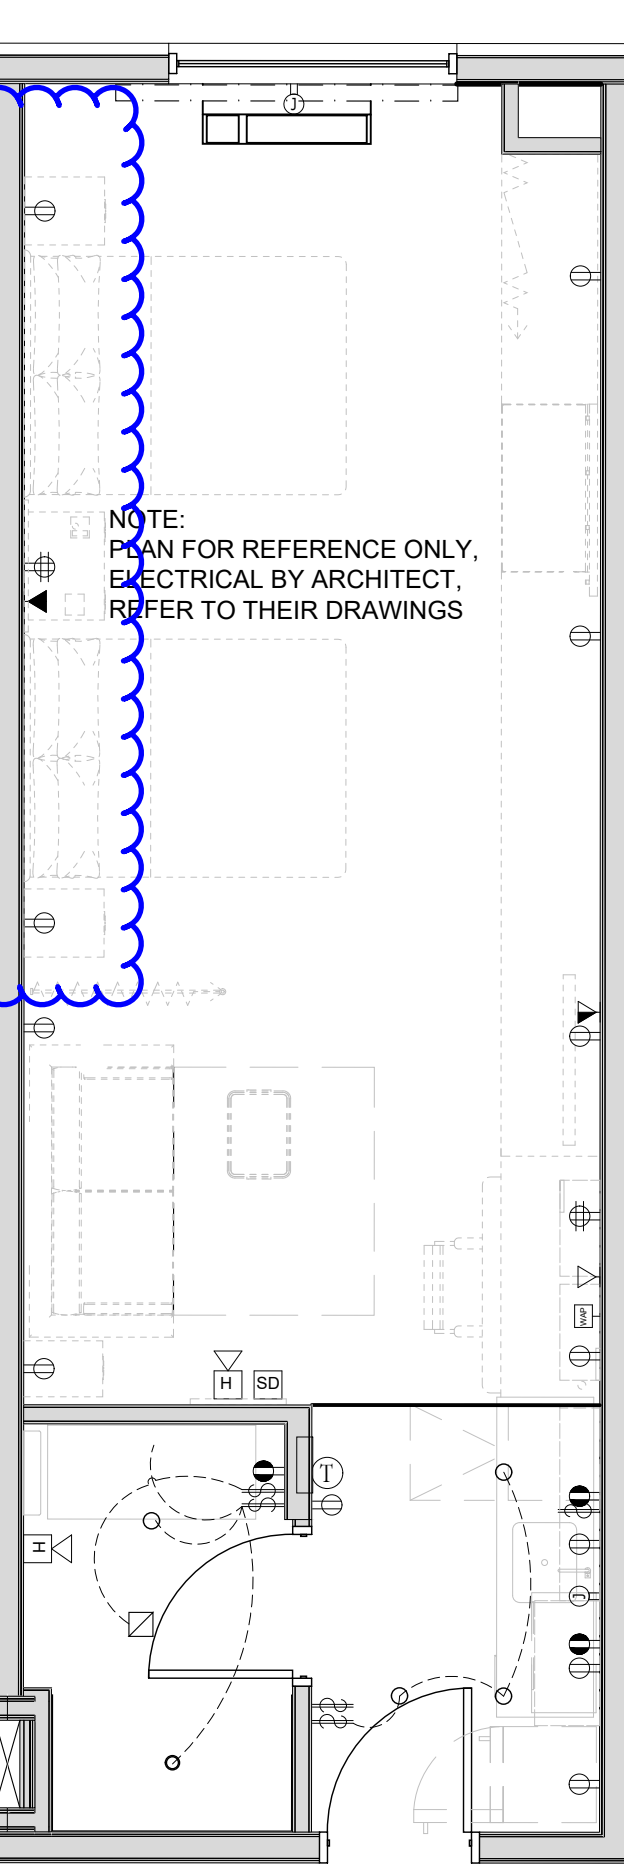


4 ELECTRICAL PLAN

1/4" = 1'-0"

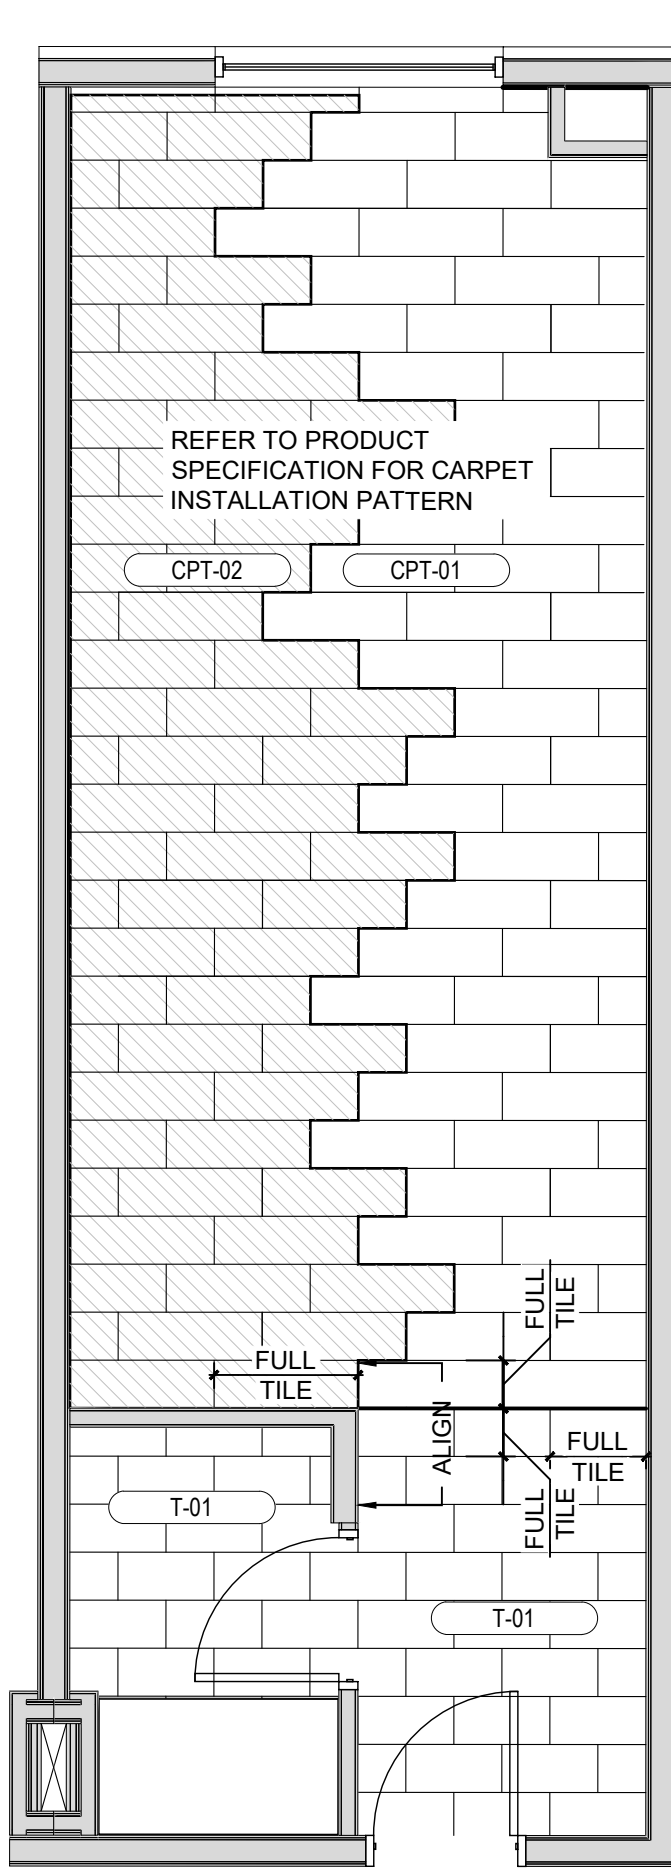


3 FINISH PLAN

1/4" = 1'-0"

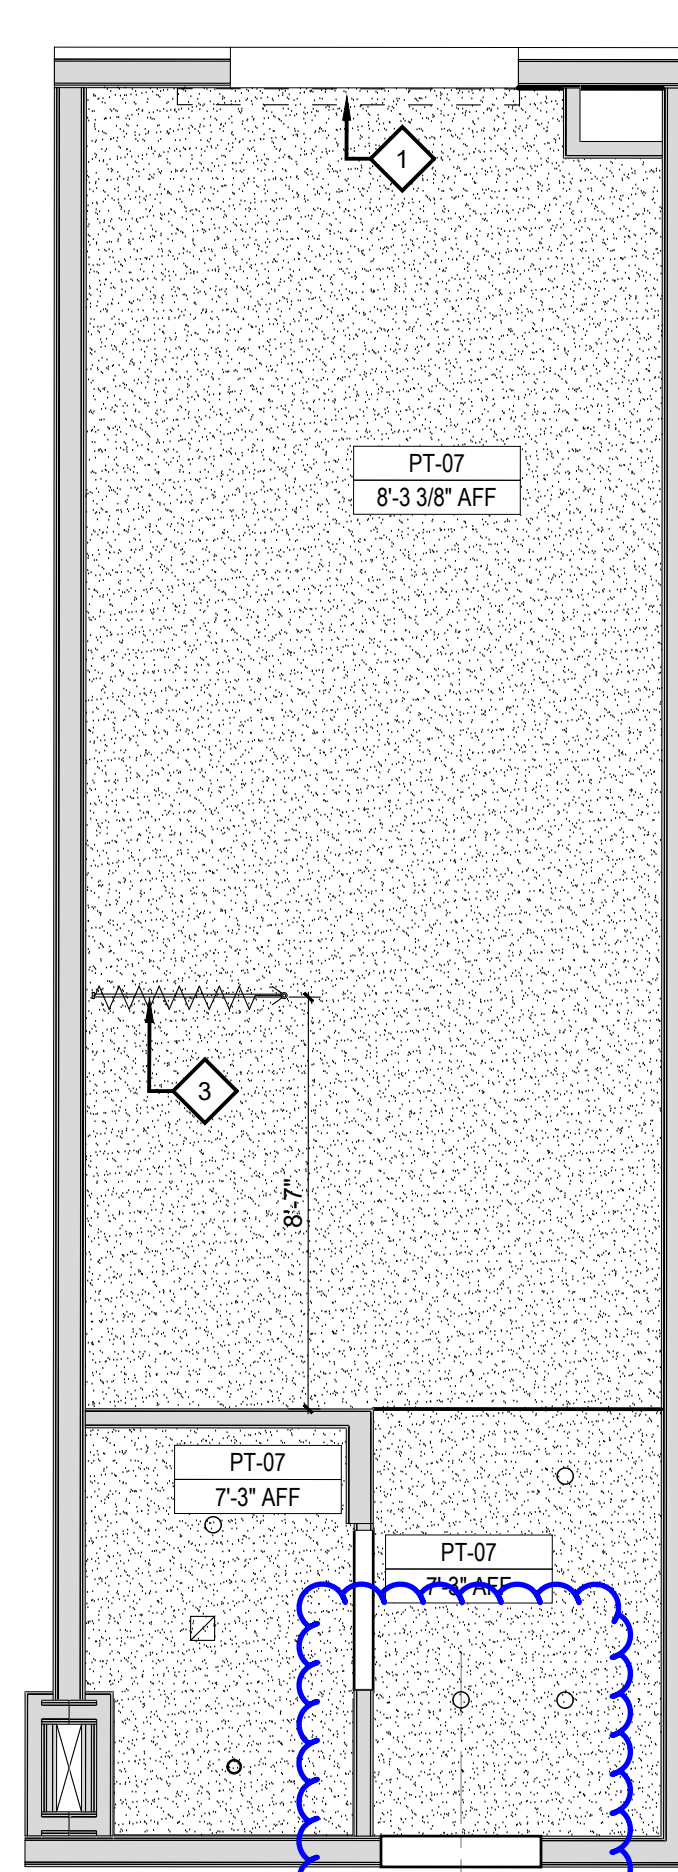


2 RCP PLAN

1/4" = 1'-0"

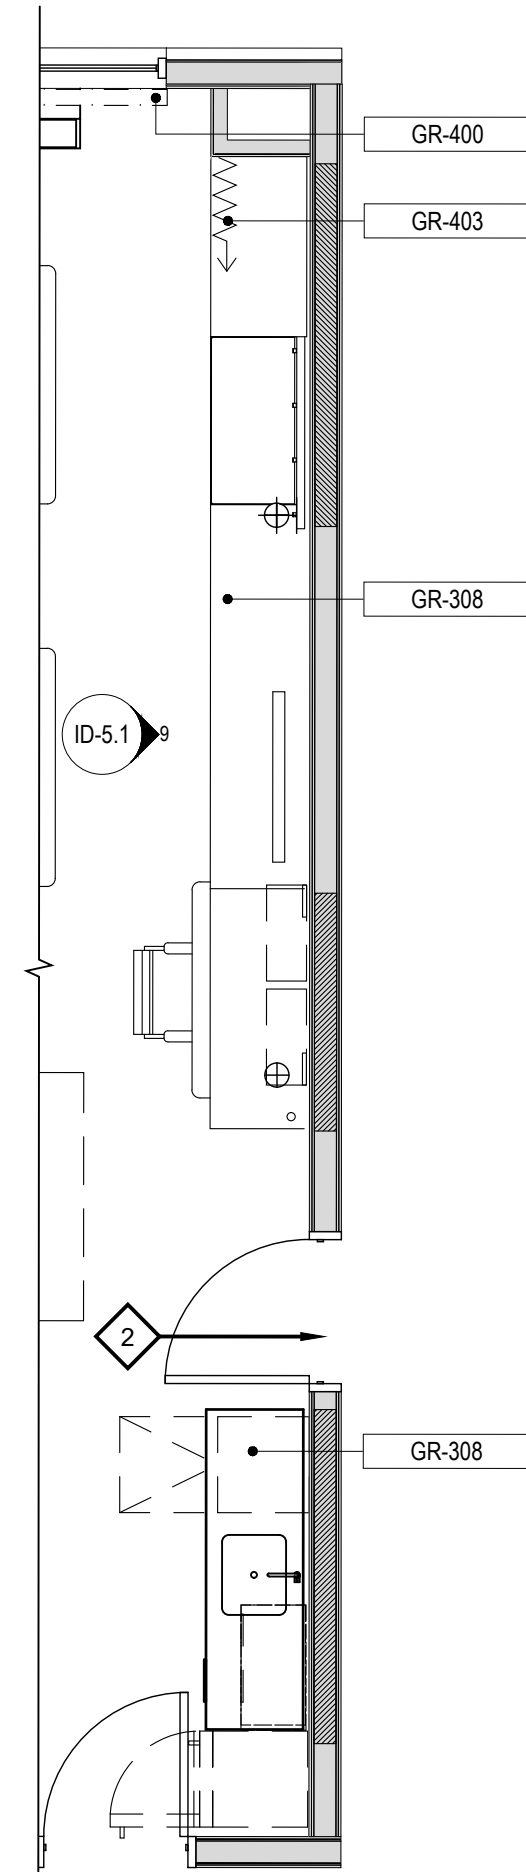

1.1 QQ STUDIO CONN. ARCHITECTURAL PLAN

1/4" = 1'-0"

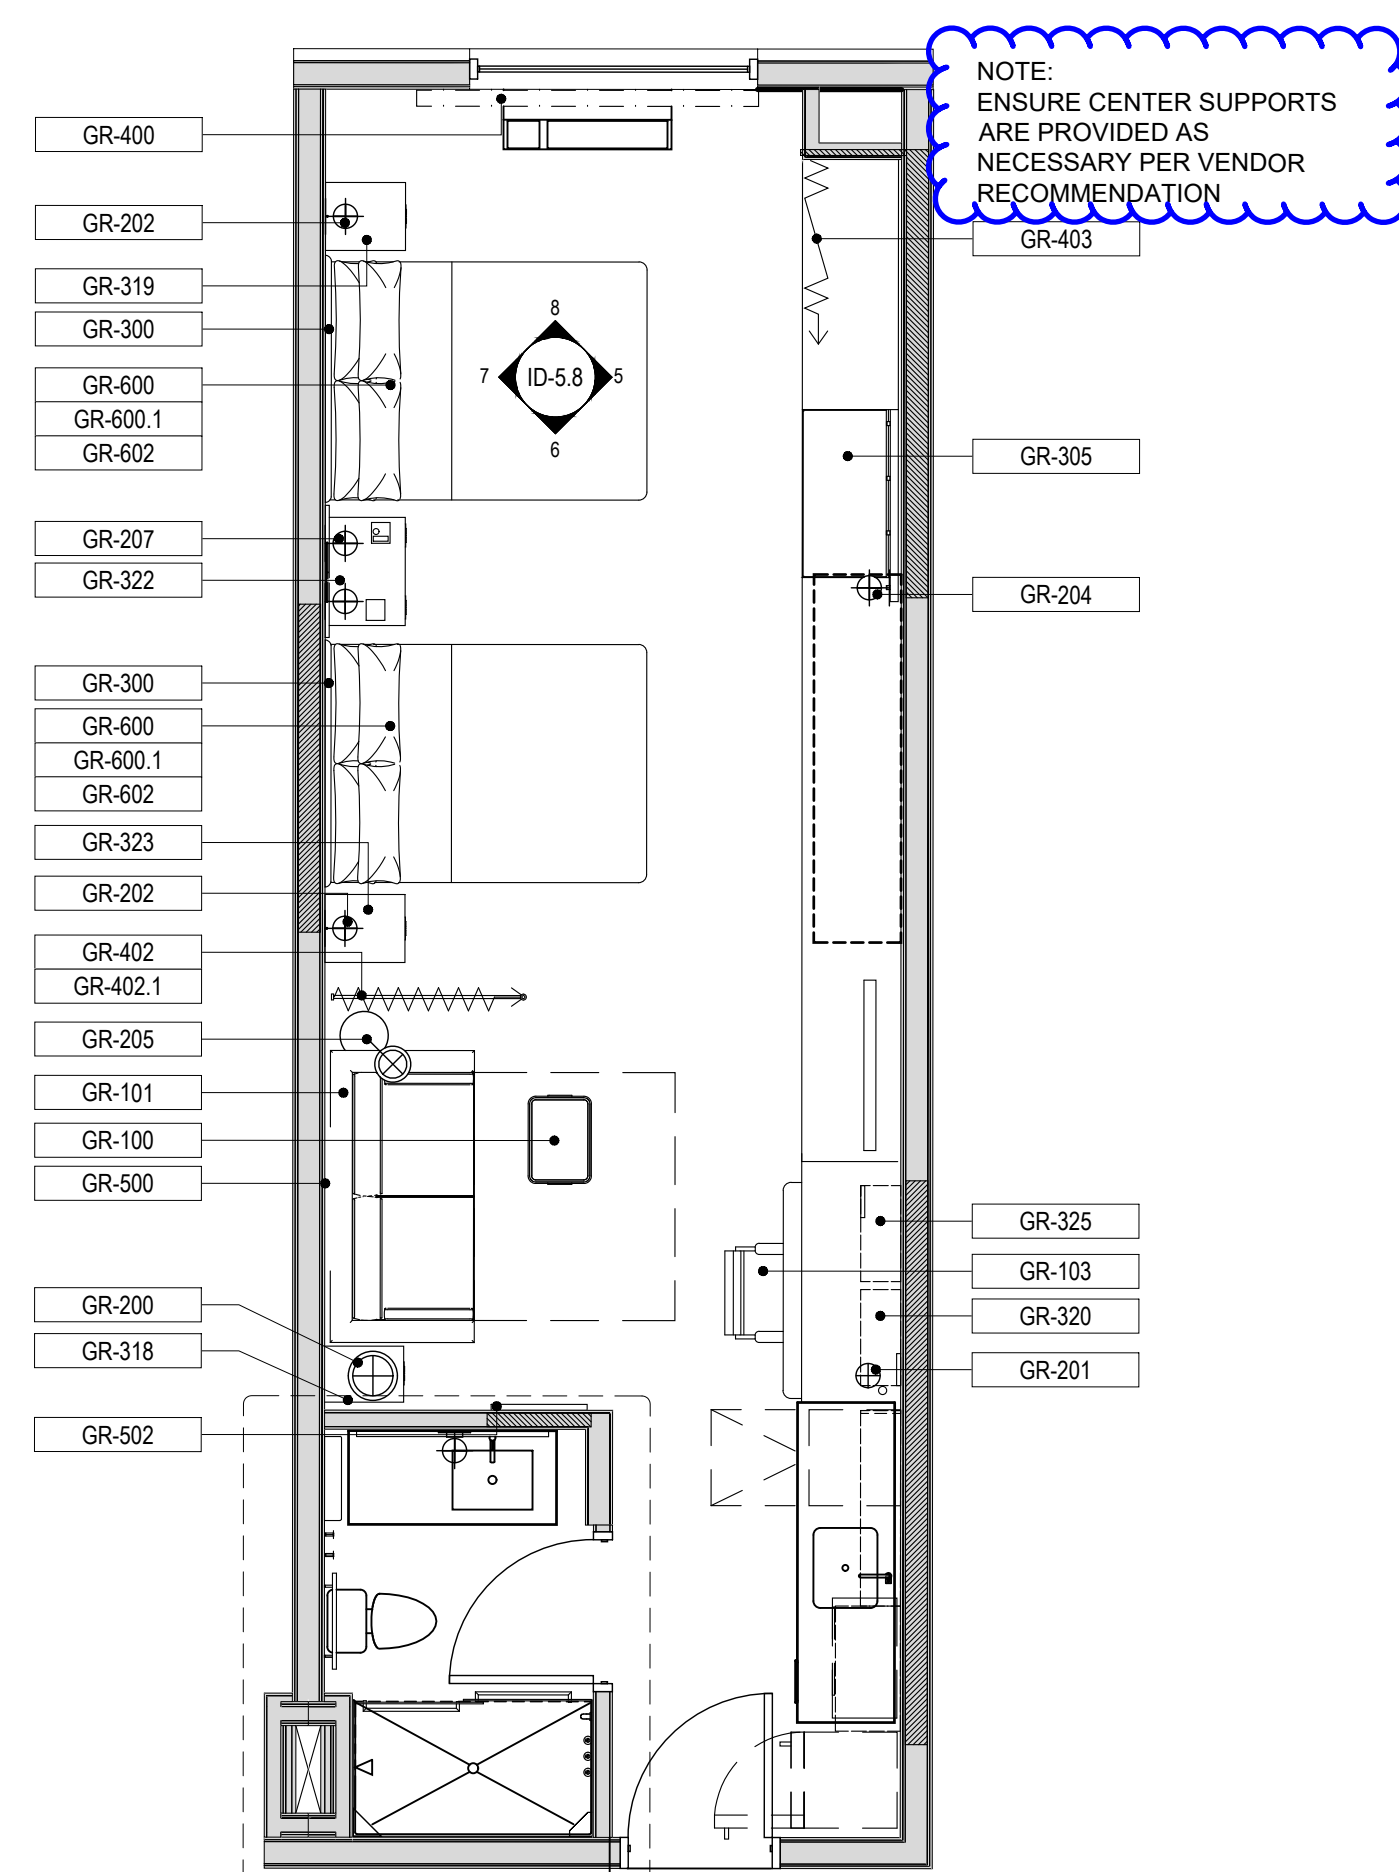

1 FFE PLAN

1/4" = 1'-0"

GENERAL NOTES	
1.	REFER TO ARCHITECTS DRAWINGS FOR ALL ARCHITECTURAL LIGHTING, EQUIPMENT, F&B, ELECTRICAL AND TRANSITION DETAILS.
2.	USE 1/3" OFFSET WHEN INSTALLING LARGE TILES TO AVOID LIPPAGE
3.	REFRAIN FROM CUTTING TILES DURING INSTALLATION. ONLY INSTALL WHOLE TILES WHEN POSSIBLE.
KEY NOTES:	
◆	BLACK OUT ROLLER SHADE TO EXTEND 6" BEYOND WINDOW OPENING. SHEER ROLLER SHADE TO BE MOUNTED INSIDE WINDOW OPENING. GR-400 IS MANUAL. GR-401 IS MOTORIZED.
◆	ALTERNATE LOCATION OF DOOR FOR CONNECTING ROOMS TO ACCESSIBLE ROOMS-REFER TO OVERALL PLANS FOR LOCATION OF ACCESSIBLE ROOMS
◆	CORRDINATE CURTAIN BLOCKING LOCATION WITH ARCHITECT DRAWINGS



6255 Corporate Center Drive
Dublin, OH 43016
(p) 614.933.0300
(e) info@rkhdesign.com
www.rkhdesign.com



HOME2 SUITES BY HILTON
EAGLEPASS, TX

H2EP LLC

ISSUE SET:
NEW CONSTRUCTION

DATE:
07/04/2025

SCALE:
AS INDICATED

REVISION:
DATE COMMENTS

SHEET TITLE:
ENLARGED GUESTROOM PLANS
& ELEVATIONS - QQ STD., QQ
EXT., & QQ STD. CONN.

SHEET NUMBER:

ID-5.8